


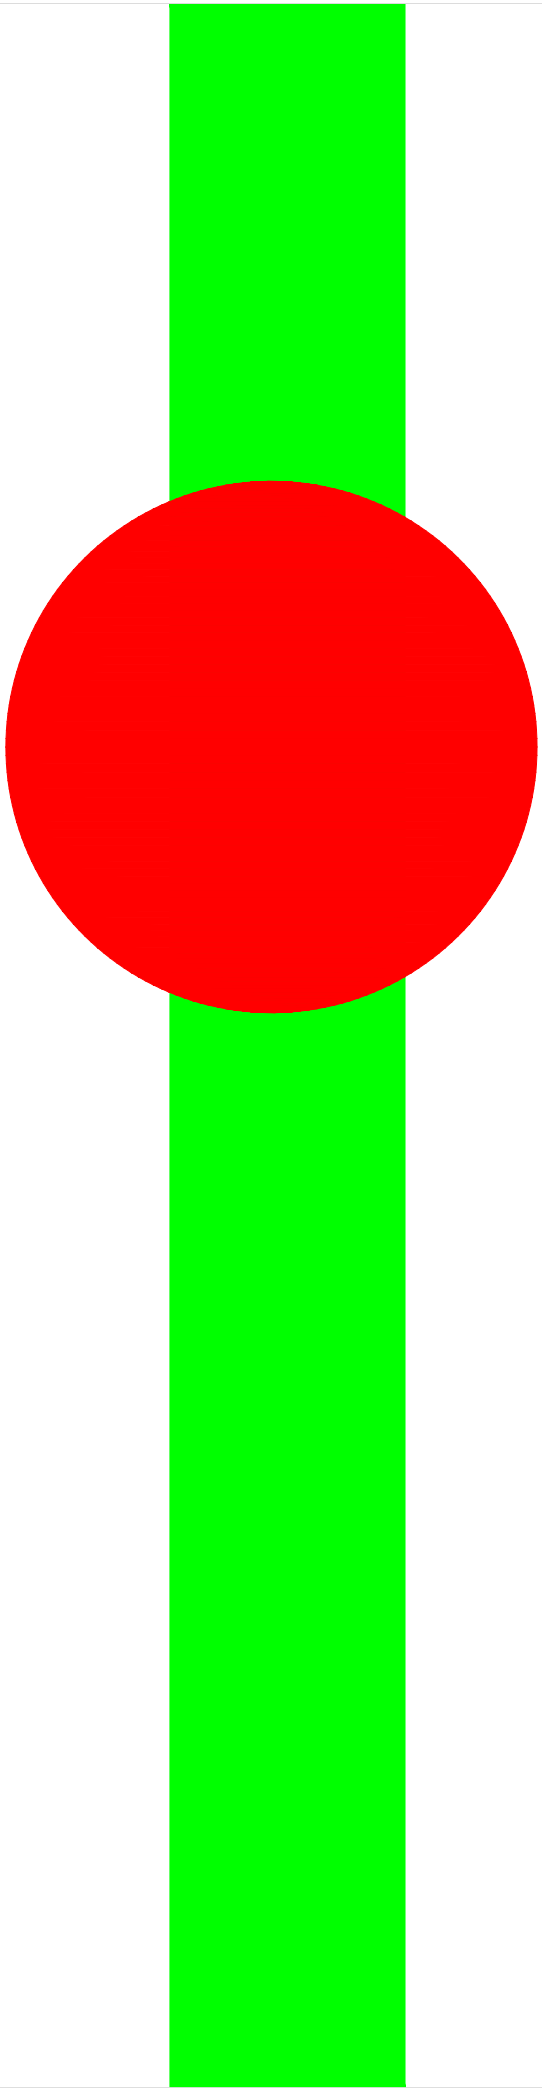

STRUCTURAL DRAWING

PROPOSED 4 STORIED RESIDENTIAL BUILDING FOR
MR. MD. REJAUL KARIM AT VILL: HARINMARI,
PALASHBARI MUNICIPALITY,GAIBANDHA

CONSULTANT:

PRODHAN DESIGN & CONSTRUCTION

Address: 94/3,LEVEL-2, TALLABAGH, INDIRA ROAD, DHAKA-1215

***SITE OFFICE: M/S. TMRR ENTERPRISE, KALIBARI BAZAR,
PALASHBARI MUNICIPALITY,GAIBANDHA.***

Email: dynamicdesign.structures@gmail.com

FOR ANY QUERY OF
STRUCTURAL DESIGN
PLEASE DISCUSS WITH
CONSULTANT

ELECTRICAL DRAWINGS LIST OF G+4- STORIED RESIDENTIAL BUILDING.					PROJECT NAME G+4 STORIED RESIDENTIAL BUILDING AT HARINMARI, PALASHBARI MUNICIPALITY, GAIBANDHA			
					CLIENT NAME MR. MD. REJAUL KARIM			
					DRAWING TITLE Electrical Layout Plan.			
					ENGINEER MD. RIYADUL ISLAM PRODHAN B. Sc in Civil Engg. NSU M.Sc in Civil Engg. AUST M.Sc in Soil Science. DU M.Sc in ESM. JU IEB. REG. NO: M-45122			
					MAHBUB KARIM B. Sc in Civil Engg. NSU M. Sc in Civil Engg. BUET M.Sc in Civil Engg. CDU (AUSTRALIA) IEB. REG. NO: M-45123			
					ABDULLAH-AL-FOYSAL B. Sc in EEE; EASTERN UNIVERSITY Diploma in Electrical; ICST IEB. REG. NO: PENDING			
					APPROVED BY			
					ELECTRICAL LAYOUT DRAWN BY			
					ABDULLAH-AL-FOYSAL			
					CONSULTANT			
					Prodhan Design & Construction Address: 94/3, LEVEL-2, TALLABAGH, INDIRA ROAD, DHAKA-1215 SITE OFFICE: M/S. TMRR ENTERPRISE, KALIBARI BAZAR, PALASHBARI MUNICIPALITY,GAIBANDHA.			
					1	22/07/26	1ST,3RD,4TH FLOOR	
					NO.	DATE	REVISION	BY
					CAD BY:		SHEET NO:	
							1	
					DATE:		SCALE:	
					11/07/2026		5":1'	

LIST OF FIXTURE	SYMBOL	HEIGHT FROM FFL	LIST OF FIXTURE	SYMBOL	HEIGHT FROM FFL
SWITCH, FAN REGULATOR	SB	1350mm	AC SPLIT SOCKET POINT	T(AC)	2250mm
WALL BRACKET & TUBE LIGHT	BA, TA	2400mm	GEYSER SOCKET POINT	T	2100mm
CEILING FAN	F	2600mm	DISTRIBUTION BOARD	DB	1500mm
05A SOCKET OUTLET	P	1350mm	TELEPHONE, LAN, INTERCOM	TEL, N	300mm
13A SOCKET OUTLET	Q	250mm	DISH ANTENNA OUTLET	TV	1200mm

SCHEDULE OF SINGLE CORE CABLES IN CONDUITS AS PER BNBC					
COPPER CONDUCTOR SIZE mm ² (TYPE-BYA)	PVC CONDUIT INNER DIAMETER (mm)				
	20mm	25mm	32mm	38mm	50mm
	MAXIMUM NUMBER OF CLABES				
1.5	6	10	14	-	-
2.5	5	10	14	-	-
4.0	3	6	10	14	-
6.0	2	5	8	11	-
10	-	4	7	9	-
16	-	2	4	5	12
25	-	-	2	2	6

ELECTRICAL GENERAL NOTES:

-  MDB MAIN DISTRIBUTION BOARD (MDB)
-  DB DISTRIBUTION BOARD (DB)
-  SB-2P SWITCH BOARD AT 1350 mm FROM FFL WITH 2 PIN SOCKET
-  SB SWITCH BOARD AT 1350 mm FROM FFL
-  Q/QWF 13A, 250V, 3-PIN SWITCHED SOCKET
-  T 20A, 250V, 3-PIN SWITCHED SOCKET FOR AC/ GEYSER
-  BA LED 1x15W WALL BRACKET LIGHT
-  TA LED 1x20W TUBE LIGHT WITH DIFFUSER
-  A LED 150x150 MM 10W LED PANEL LIGHT
-  DL LED 1x12W DOWN LIGHT
-  PM LED 300x300 12W LED PANEL LIGHT
-  BH LED 1x12W MIRROR OPTICS LIGHT
-  P HIGH BAY LIGHT FITTING 1X100W LED LAMP (TYPE-HB)
-  F 56 INCH SWEEP CEILING FAN
-  F FAN HOOK
-  F EXHAUST FAN
-  CB CALLING BELL
-  BP BELL PUSH

ELECTRICAL GENERAL NOTES:

-  CONCEALED CABLE ROUTE
-  CABLE ROUTE THROUGH FLOOR

ALL CABLE WILL GO UPWARD THROUGH ELECTRICAL DUCT

PROJECT NAME

G+4 STORIED RESIDENTIAL BUILDING AT HARINMARI, PALASHBARI MUNICIPALITY, GAIBANDHA

CLIENT NAME

MR. MD. REJAUL KARIM

DRAWING TITLE

Electrical Layout Plan.

ENGINEER

MD. RIYADUL ISLAM PRODHAN

B. Sc in Civil Engg. NSU
M.Sc in Civil Engg. AUST
M.Sc in Soil Science. DU
M.Sc in ESM. JU
IEB. REG. NO: M-45122

MAHBUB KARIM

B. Sc in Civil Engg. NSU
M. Sc in Civil Engg. BUET
M.Sc in Civil Engg. CDU (AUSTRALIA)
IEB. REG. NO: M-45123

ABDULLAH-AL-FOYSAL

B. Sc in EEE; EASTERN UNIVERSITY
Diploma in Electrical; ICST
IEB. REG. NO: PENDING

APPROVED BY

ELECTRICAL LAYOUT DRAWN BY

ABDULLAH-AL-FOYSAL

CONSULTANT

Prodhan Design & Construction

Address: 94/3, LEVEL-2, TALLABAGH, INDIRA ROAD, DHAKA-1215
SITE OFFICE: M/S. TMRR ENTERPRISE, KALIBARI BAZAR, PALASHBARI MUNICIPALITY,GAIBANDHA.

1	22/07/26	1ST,3RD,4TH FLOOR	
NO.	DATE	REVISION	BY

CAD BY:

DATE:


11/07/2026

SHEET NO:


2

SCALE:


5":1'

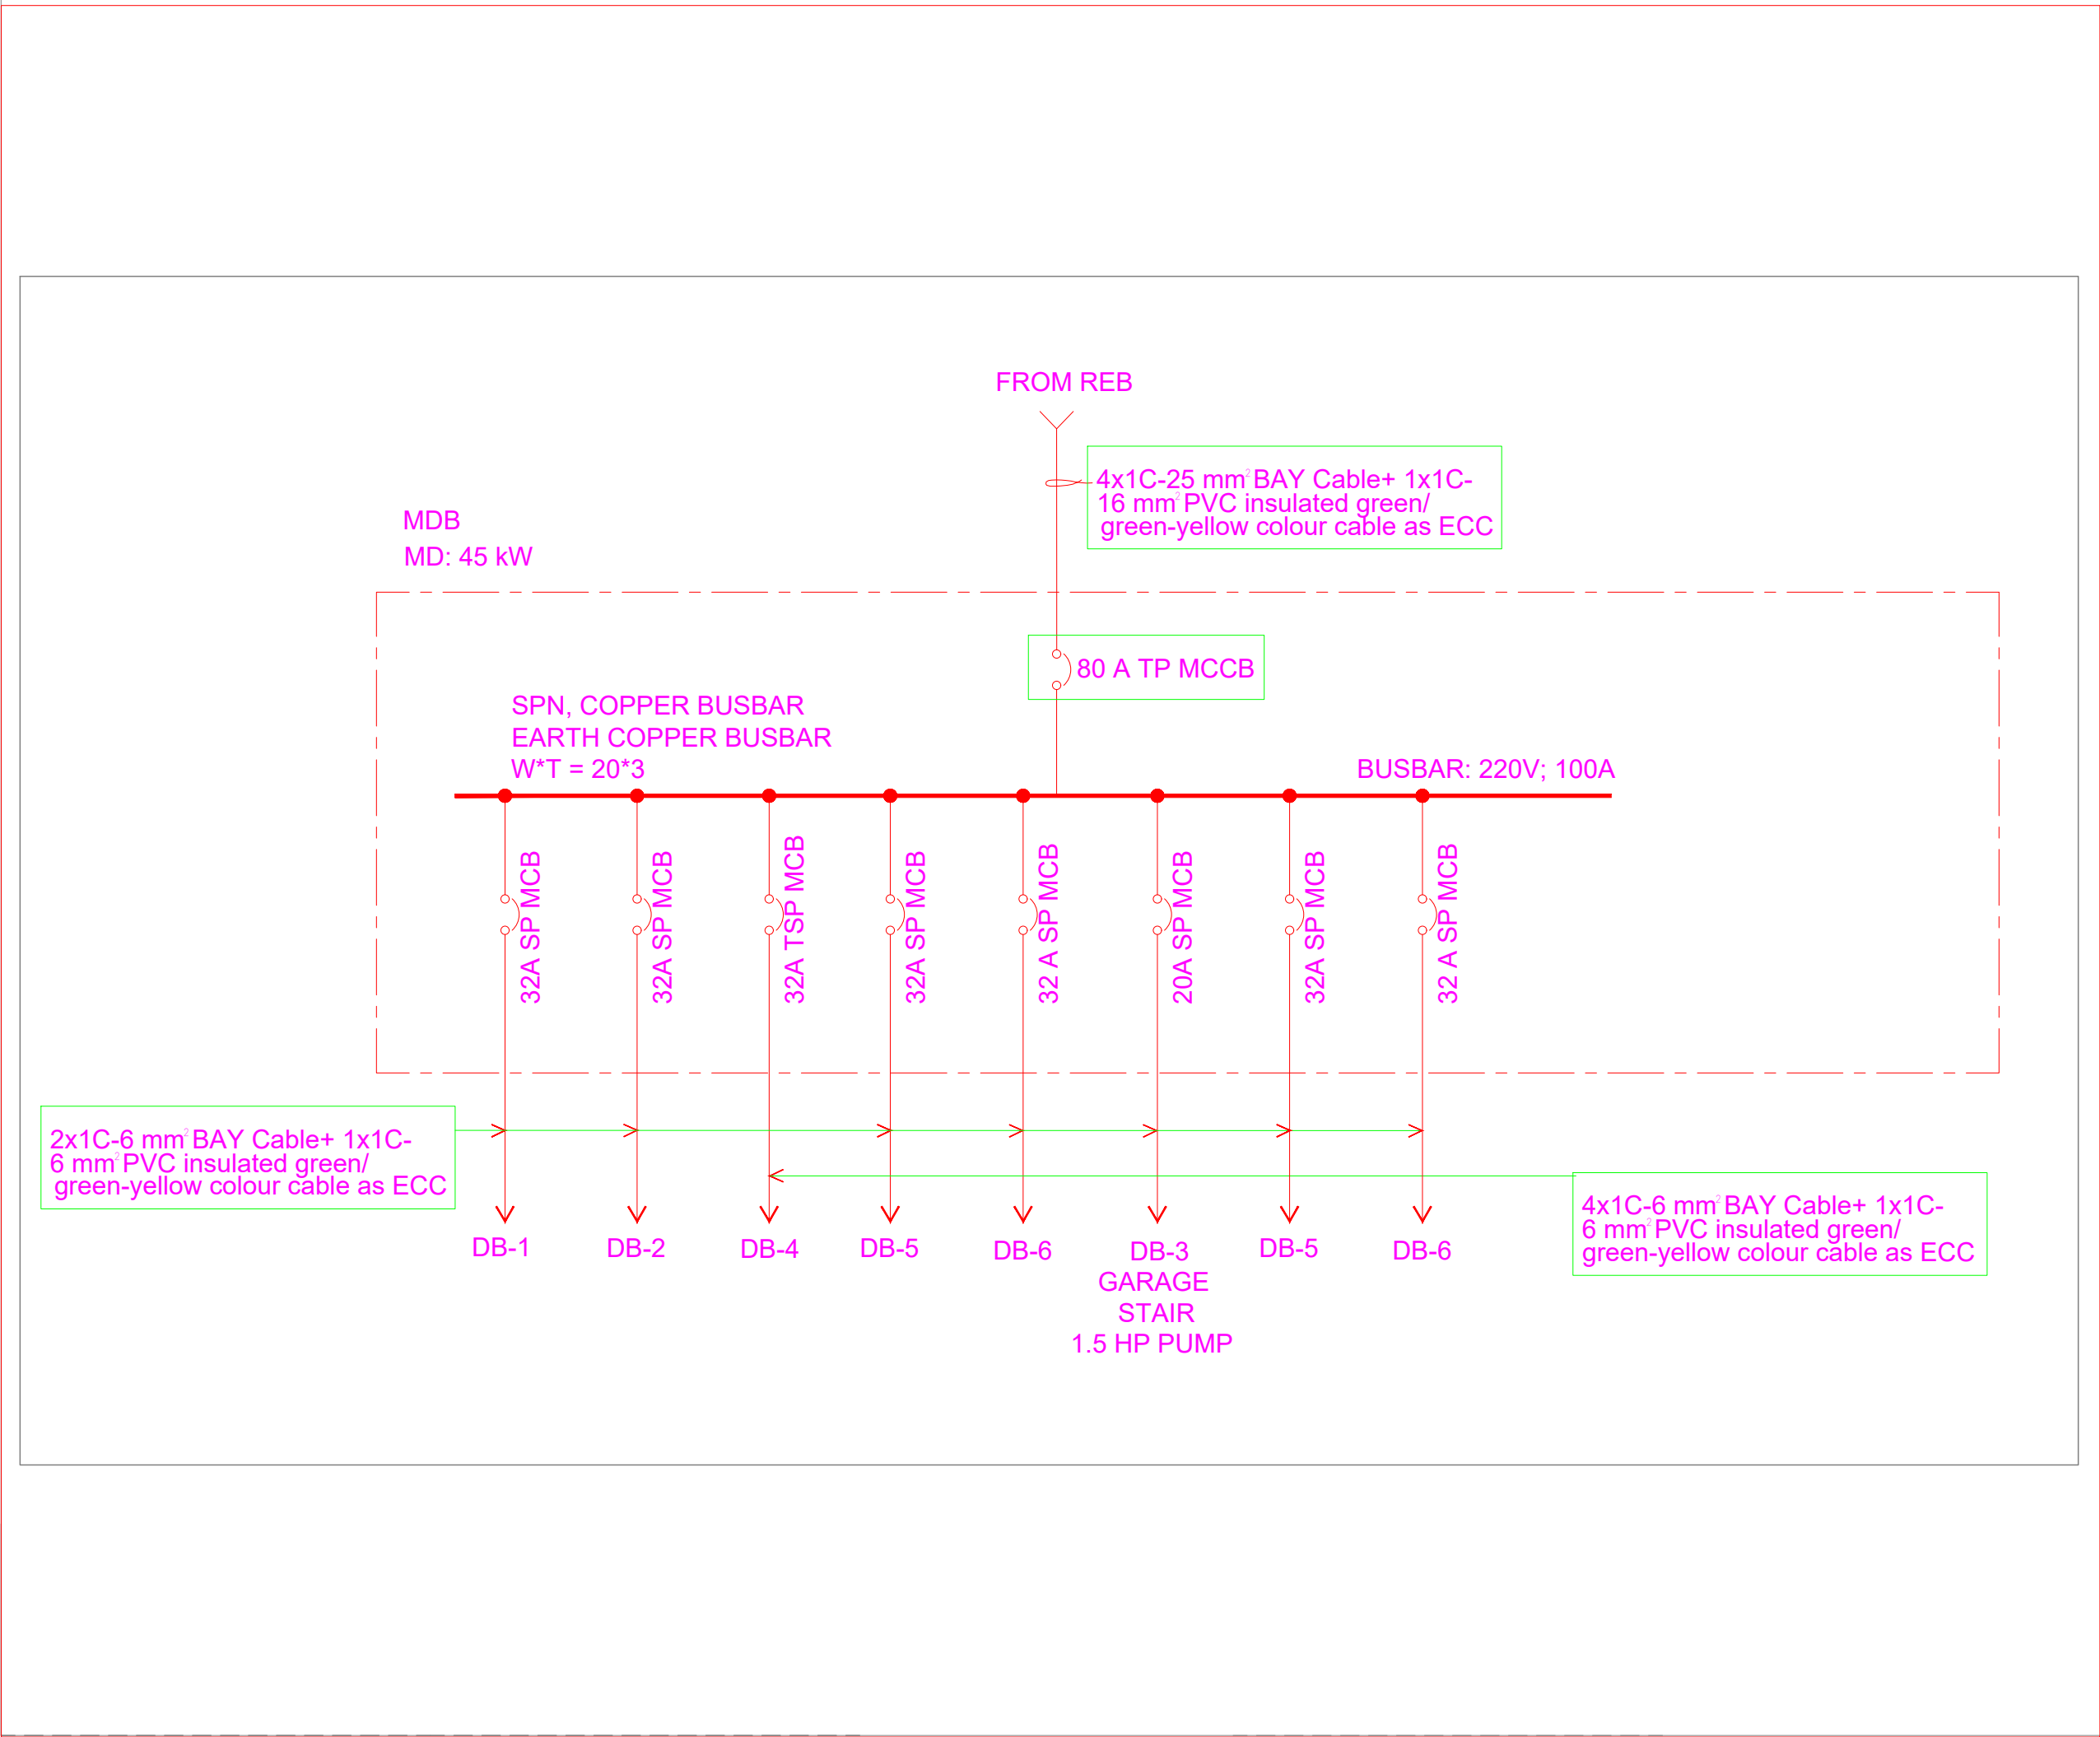

PROJECT NAME			
G+4 STORIED RESIDENTIAL BUILDING AT HARINMARI, PALASHBARI MUNICIPALITY, GAIBANDHA			
CLIENT NAME			
MR. MD. REJAUL KARIM			
DRAWING TITLE			
Electrical Layout Plan.			
ENGINEER			
MD. RIYADUL ISLAM PRODHAN			
B. Sc in Civil Engg. NSU M.Sc in Civil Engg. AUST M.Sc in Soil Science. DU M.Sc in ESM. JU IEB. REG. NO: M-45122			
MAHBUB KARIM			
B. Sc in Civil Engg. NSU M. Sc in Civil Engg. BUET M.Sc in Civil Engg. CDU (AUSTRALIA) IEB. REG. NO: M-45123			
ABDULLAH-AL-FOYSAL			
B. Sc in EEE; EASTERN UNIVERSITY Diploma in Electrical; ICST IEB. REG. NO: PENDING			
APPROVED BY			
ELECTRICAL LAYOUT DRAWN BY			
ABDULLAH-AL-FOYSAL			
CONSULTANT			
Prodhan Design & Construction			
Address: 94/3, LEVEL-2, TALLABAGH, INDIRA ROAD, DHAKA-1215 SITE OFFICE: M/S. TMRR ENTERPRISE, KALIBARI BAZAR, PALASHBARI MUNICIPALITY,GAIBANDHA.			
1	22/07/26	1ST,3RD,4TH FLOOR	
NO.	DATE	REVISION	BY
CAD BY:		SHEET NO:	
		3	
DATE:		SCALE:	
11/07/2026		5":1'	

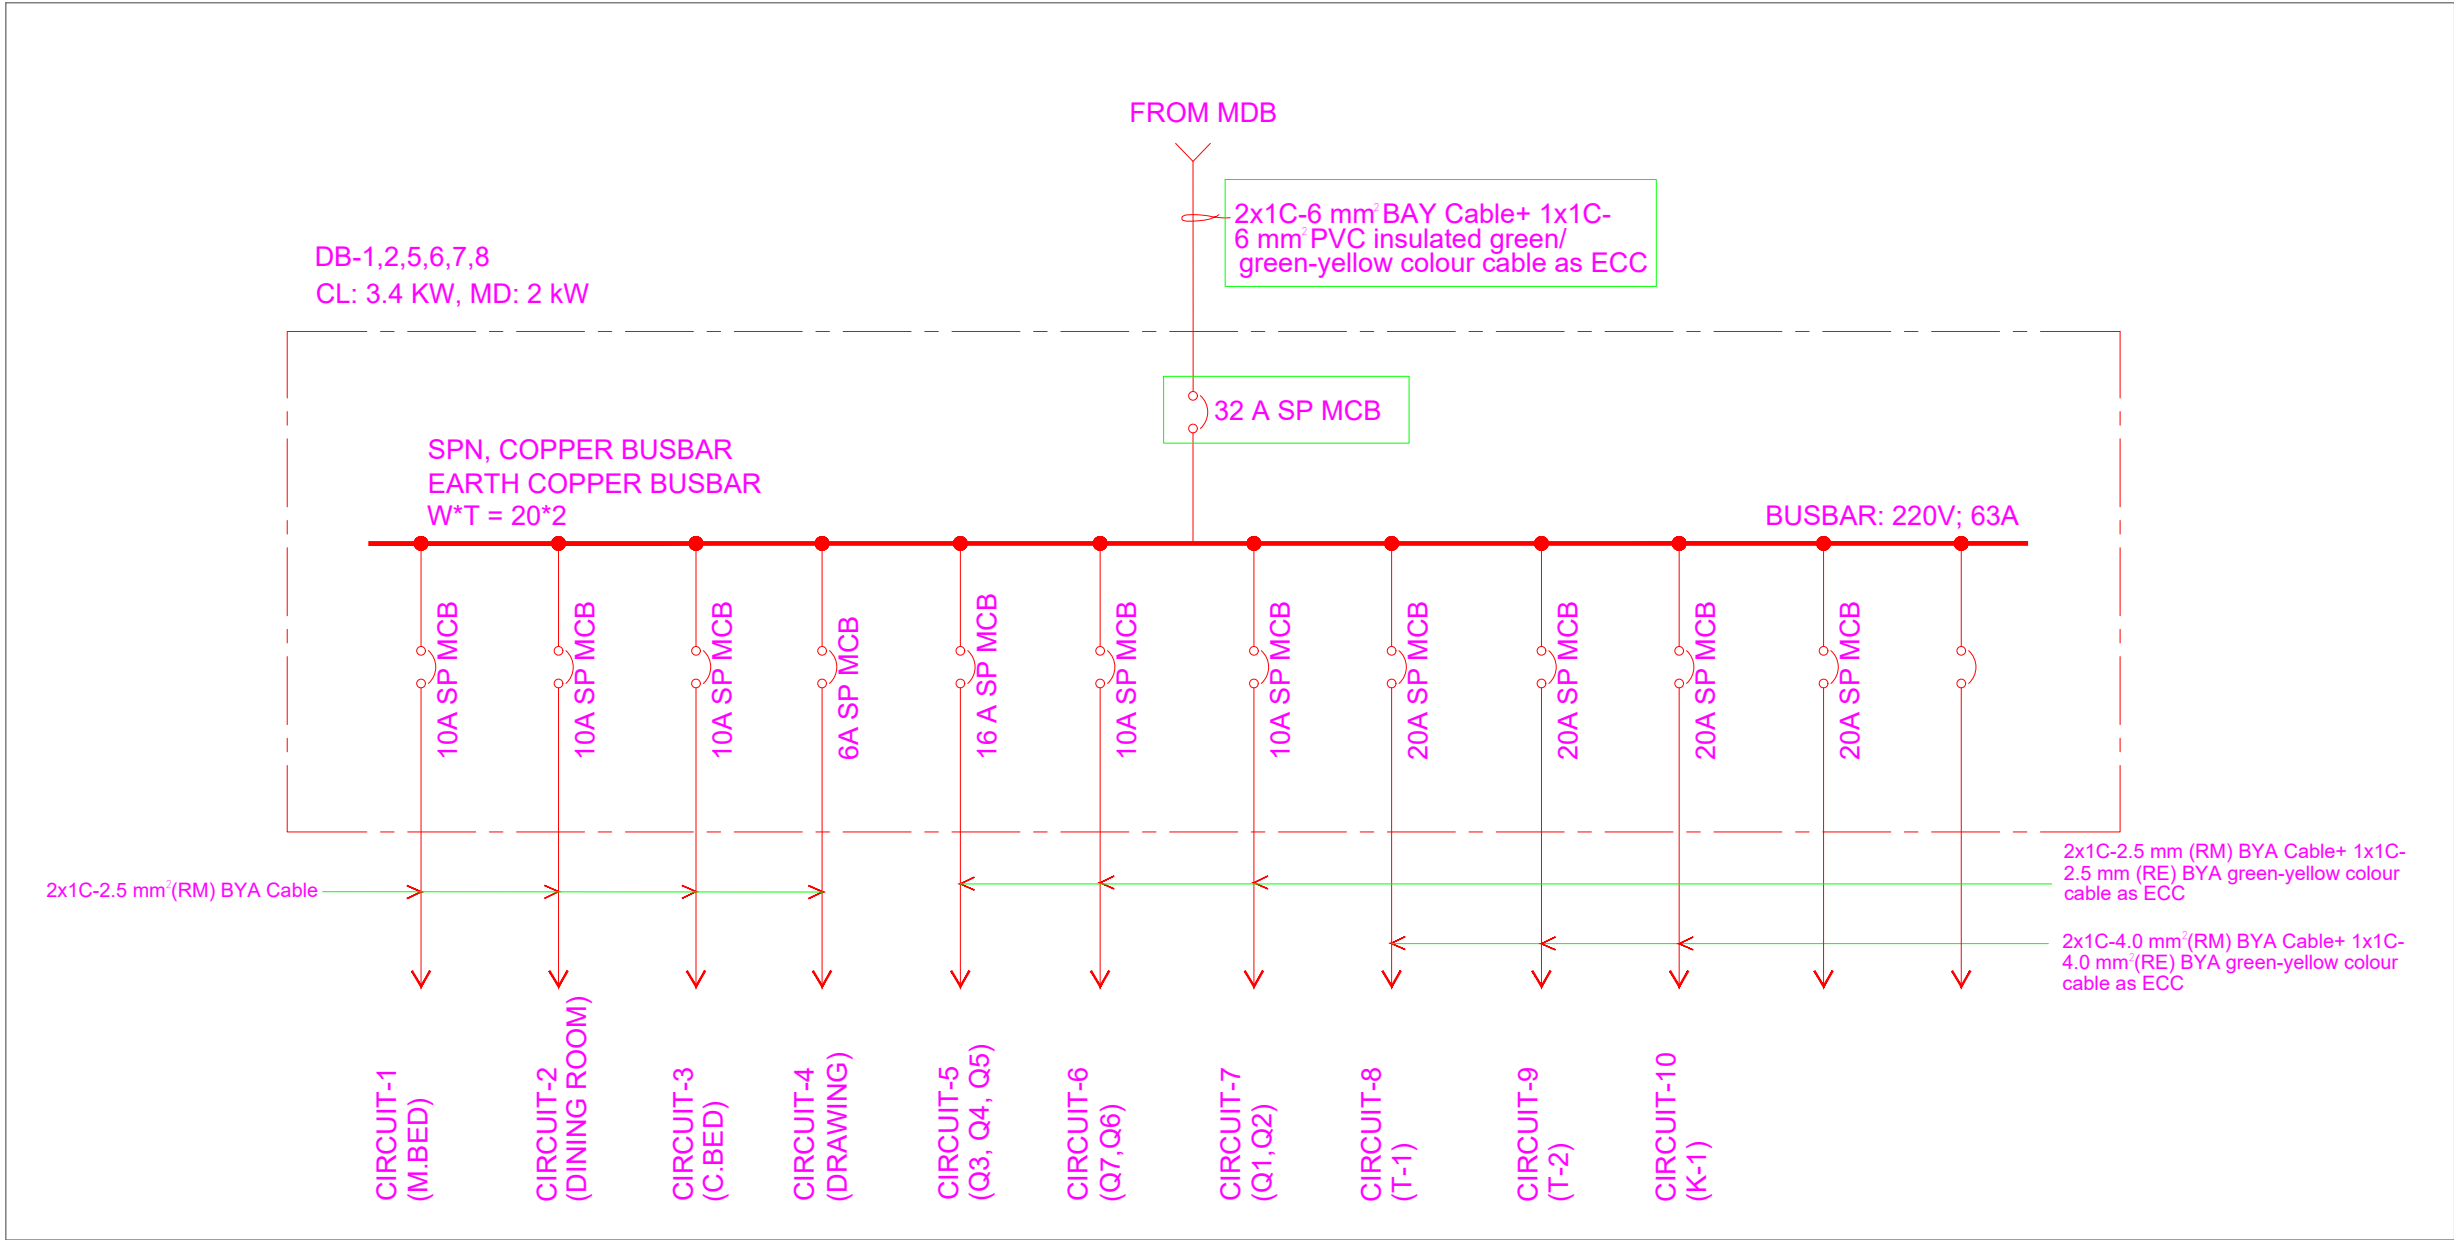

PROJECT NAME			
G+4 STORIED RESIDENTIAL BUILDING AT HARINMARI, PALASHBARI MUNICIPALITY, GAIBANDHA			
CLIENT NAME			
MR. MD. REJAUL KARIM			
DRAWING TITLE			
Electrical Layout Plan.			
ENGINEER			
MD. RIYADUL ISLAM PRODHAN			
B. Sc in Civil Engg. NSU M.Sc in Civil Engg. AUST M.Sc in Soil Science. DU M.Sc in ESM. JU IEB. REG. NO: M-45122			
MAHBUB KARIM			
B. Sc in Civil Engg. NSU M. Sc in Civil Engg. BUET M.Sc in Civil Engg. CDU (AUSTRALIA) IEB. REG. NO: M-45123			
ABDULLAH-AL-FOYSAL			
B. Sc in EEE; EASTERN UNIVERSITY Diploma in Electrical; ICST IEB. REG. NO: PENDING			
APPROVED BY			
ELECTRICAL LAYOUT DRAWN BY			
ABDULLAH-AL-FOYSAL			
CONSULTANT			
Prodhan Design & Construction			
Address: 94/3, LEVEL-2, TALLABAGH, INDIRA ROAD, DHAKA-1215 SITE OFFICE: M/S. TMRR ENTERPRISE, KALIBARI BAZAR, PALASHBARI MUNICIPALITY,GAIBANDHA.			
1	22/07/26	1ST,3RD,4TH FLOOR	
NO.	DATE	REVISION	BY
CAD BY:		SHEET NO:	
		4	
DATE:		SCALE:	
11/07/2026		5":1'	

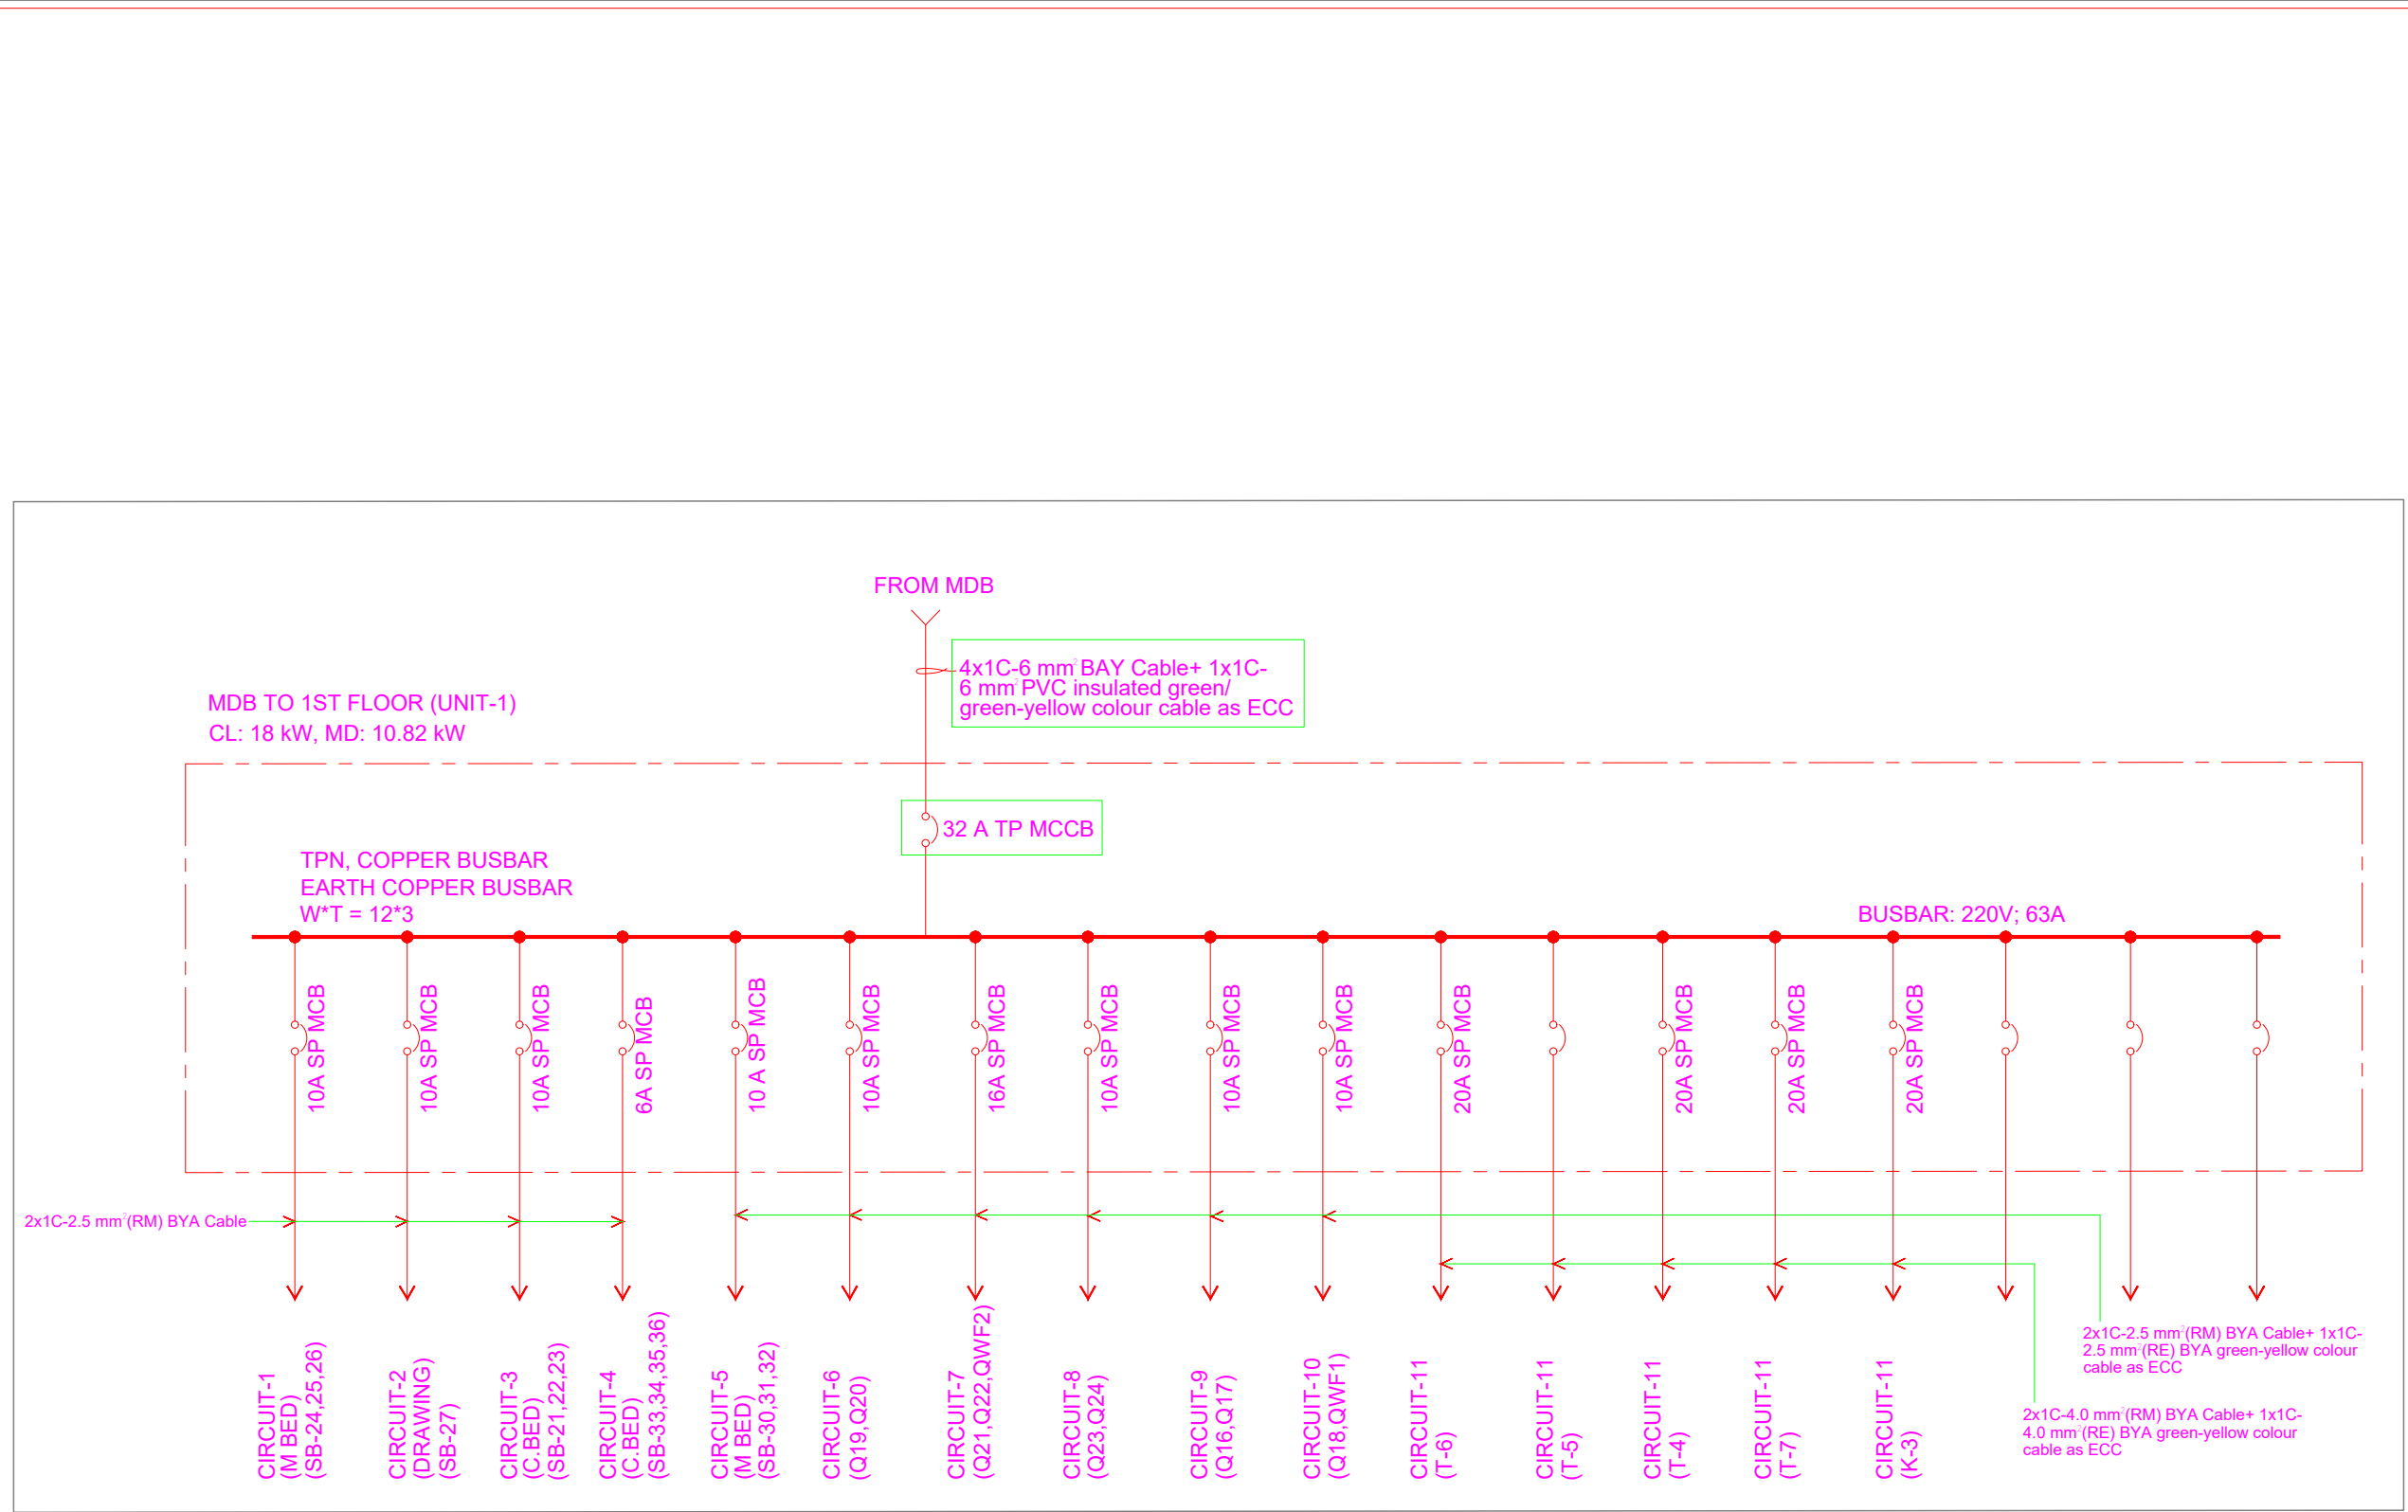

PROJECT NAME

G+4 STORIED RESIDENTIAL BUILDING AT HARINMARI, PALASHBARI MUNICIPALITY, GAIBANDHA

CLIENT NAME

MR. MD. REJAUL KARIM

DRAWING TITLE

Electrical Layout Plan.

ENGINEER

MD. RIYADUL ISLAM
PRODHAN

B. Sc in Civil Engg. NSU
M.Sc in Civil Engg. AUST
M.Sc in Soil Science. DU
M.Sc in ESM. JU
IEB. REG. NO: M-45122

MAHBUB KARIM

B. Sc in Civil Engg. NSU
M. Sc in Civil Engg. BUET
M.Sc in Civil Engg. CDU (AUSTRALIA)
IEB. REG. NO: M-45123

ABDULLAH-AL-FOYSAL

B. Sc in EEE; EASTERN UNIVERSITY
Diploma in Electrical; ICST
IEB. REG. NO: PENDING

APPROVED BY

ELECTRICAL LAYOUT DRAWN BY


ABDULLAH-AL-FOYSAL

CONSULTANT

Prodhan Design & Construction

Address: 94/3, LEVEL-2, TALLABAGH, INDIRA ROAD, DHAKA-1215
SITE OFFICE: M/S. TMRR ENTERPRISE, KALIBARI BAZAR, PALASHBARI MUNICIPALITY,GAIBANDHA.

1	22/07/26	1ST,3RD,4TH FLOOR	
NO.	DATE	REVISION	BY
CAD BY:		SHEET NO:	
		5	
DATE:		SCALE:	
11/07/2026		5":1'	

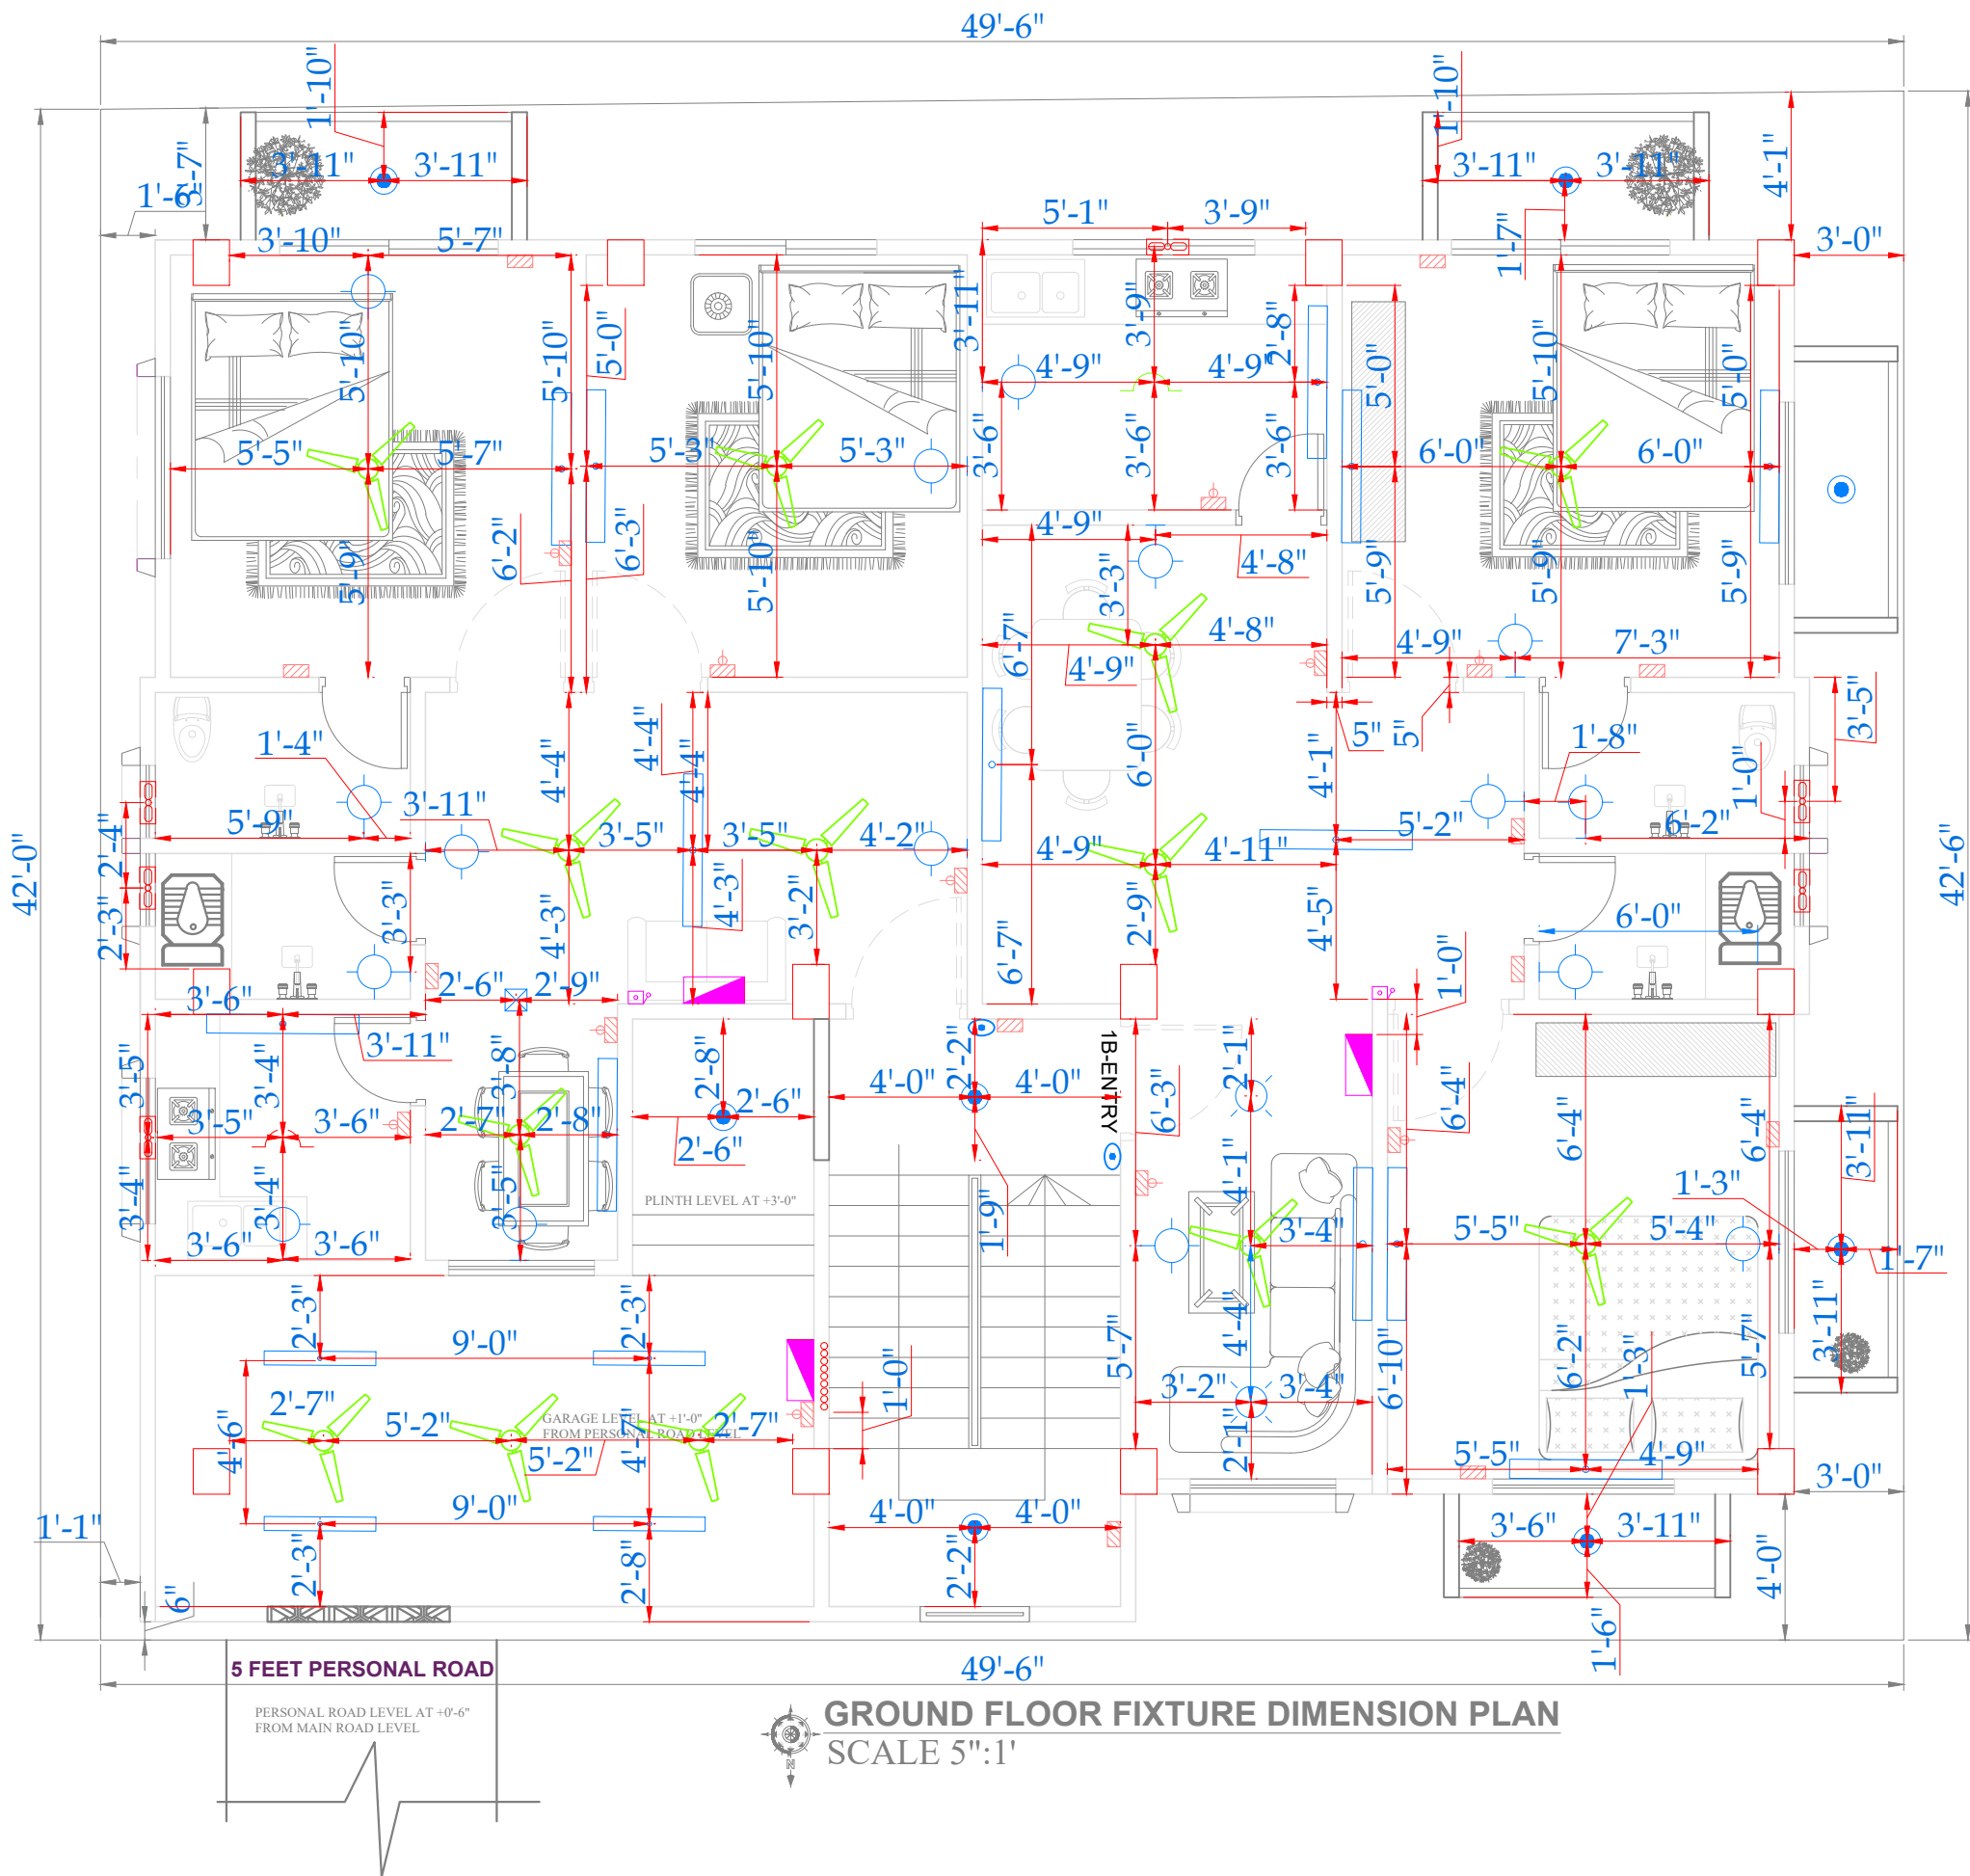

PROJECT NAME
G+4 STORIED RESIDENTIAL BUILDING AT
HARINMARI, PALASHBARI MUNICIPALITY,
GAIBANDHA

CLIENT NAME
MR. MD. REJAUL KARIM

DRAWING TITLE
Electrical Layout Plan.

ENGINEER
**MD. RIYADUL ISLAM
PRODHAN**
B. Sc in Civil Engg. NSU
M.Sc in Civil Engg. AUST
M.Sc in Soil Science. DU
M.Sc in ESM. JU
IEB. REG. NO: M-45122

MAHBUB KARIM
B. Sc in Civil Engg. NSU
M. Sc in Civil Engg. BUET
M.Sc in Civil Engg. CDU (AUSTRALIA)
IEB. REG. NO: M-45123

ABDULLAH-AL-FOYSAL
B. Sc in EEE; EASTERN UNIVERSITY
Diploma in Electrical; ICST
IEB. REG. NO: PENDING

APPROVED BY


ELECTRICAL LAYOUT DRAWN BY

ABDULLAH-AL-FOYSAL

CONSULTANT

Prodhan Design & Construction
Address: 94/3, LEVEL-2, TALLABAGH,
INDIRA ROAD, DHAKA-1215
SITE OFFICE: M/S. TMRR ENTERPRISE,
KALIBARI BAZAR, PALASHBARI
MUNICIPALITY,GAIBANDHA.

1	22/07/26	1ST,3RD,4TH FLOOR	
NO.	DATE	REVISION	BY
CAD BY:		SHEET NO: 7	
DATE: 11/07/2026		SCALE: 5":1'	

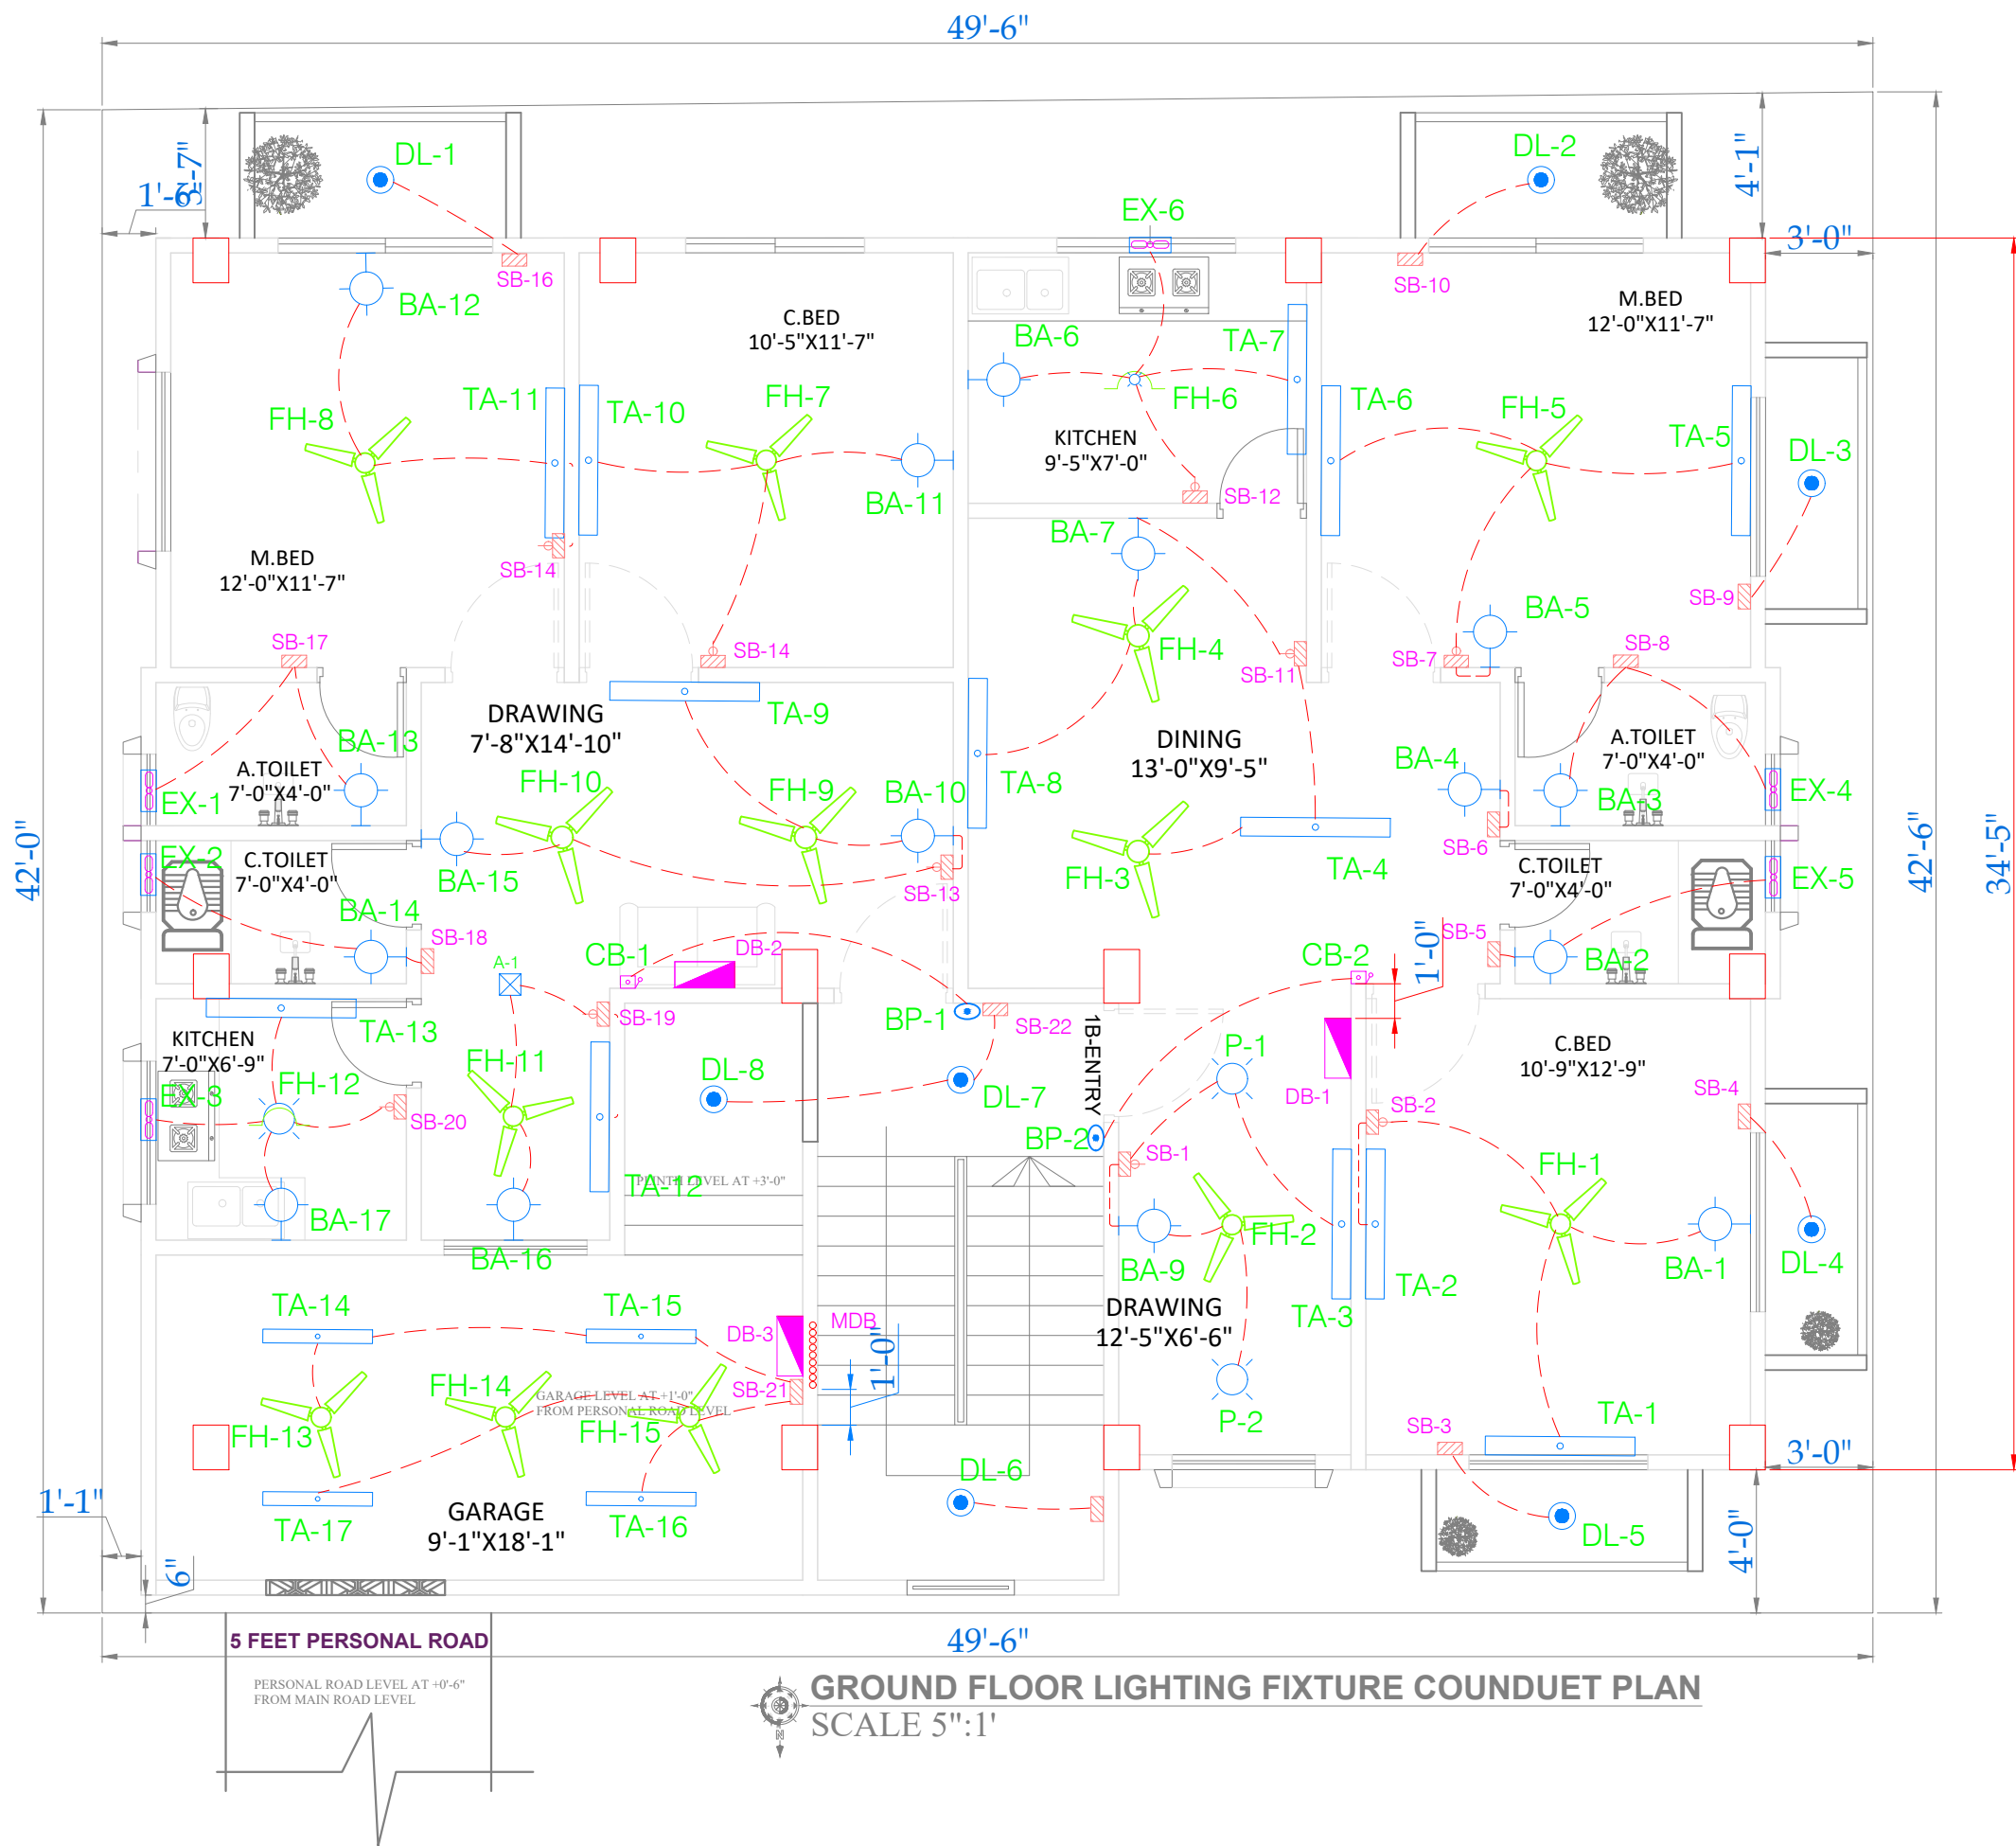

GROUND FLOOR LIGHTING FIXTURE COUNDUET PLAN
SCALE 5":1'

PROJECT NAME
G+4 STORIED RESIDENTIAL BUILDING AT
HARINMARI, PALASHBARI MUNICIPALITY,
GAIBANDHA

CLIENT NAME
MR. MD. REJAUL KARIM

DRAWING TITLE
Electrical Layout Plan.

ENGINEER
**MD. RIYADUL ISLAM
PRODHAN**
B. Sc in Civil Engg. NSU
M.Sc in Civil Engg. AUST
M.Sc in Soil Science. DU
M.Sc in ESM. JU
IEB. REG. NO: M-45122

MAHBUB KARIM
B. Sc in Civil Engg. NSU
M. Sc in Civil Engg. BUET
M.Sc in Civil Engg. CDU (AUSTRALIA)
IEB. REG. NO: M-45123


ABDULLAH-AL-FOYSAL
B. Sc in EEE; EASTERN UNIVERSITY
Diploma in Electrical; ICST
IEB. REG. NO: PENDING

APPROVED BY


ELECTRICAL LAYOUT DRAWN BY
ABDULLAH-AL-FOYSAL

CONSULTANT
Prodhan Design & Construction
Address: 94/3, LEVEL-2, TALLABAGH,
INDIRA ROAD, DHAKA-1215
SITE OFFICE: M/S. TMRR ENTERPRISE,
KALIBARI BAZAR, PALASHBARI
MUNICIPALITY,GAIBANDHA.

1	22/07/26	1ST,3RD,4TH FLOOR	
NO.	DATE	REVISION	BY
CAD BY:		SHEET NO: 8	
DATE: 11/07/2026		SCALE: 5":1'	

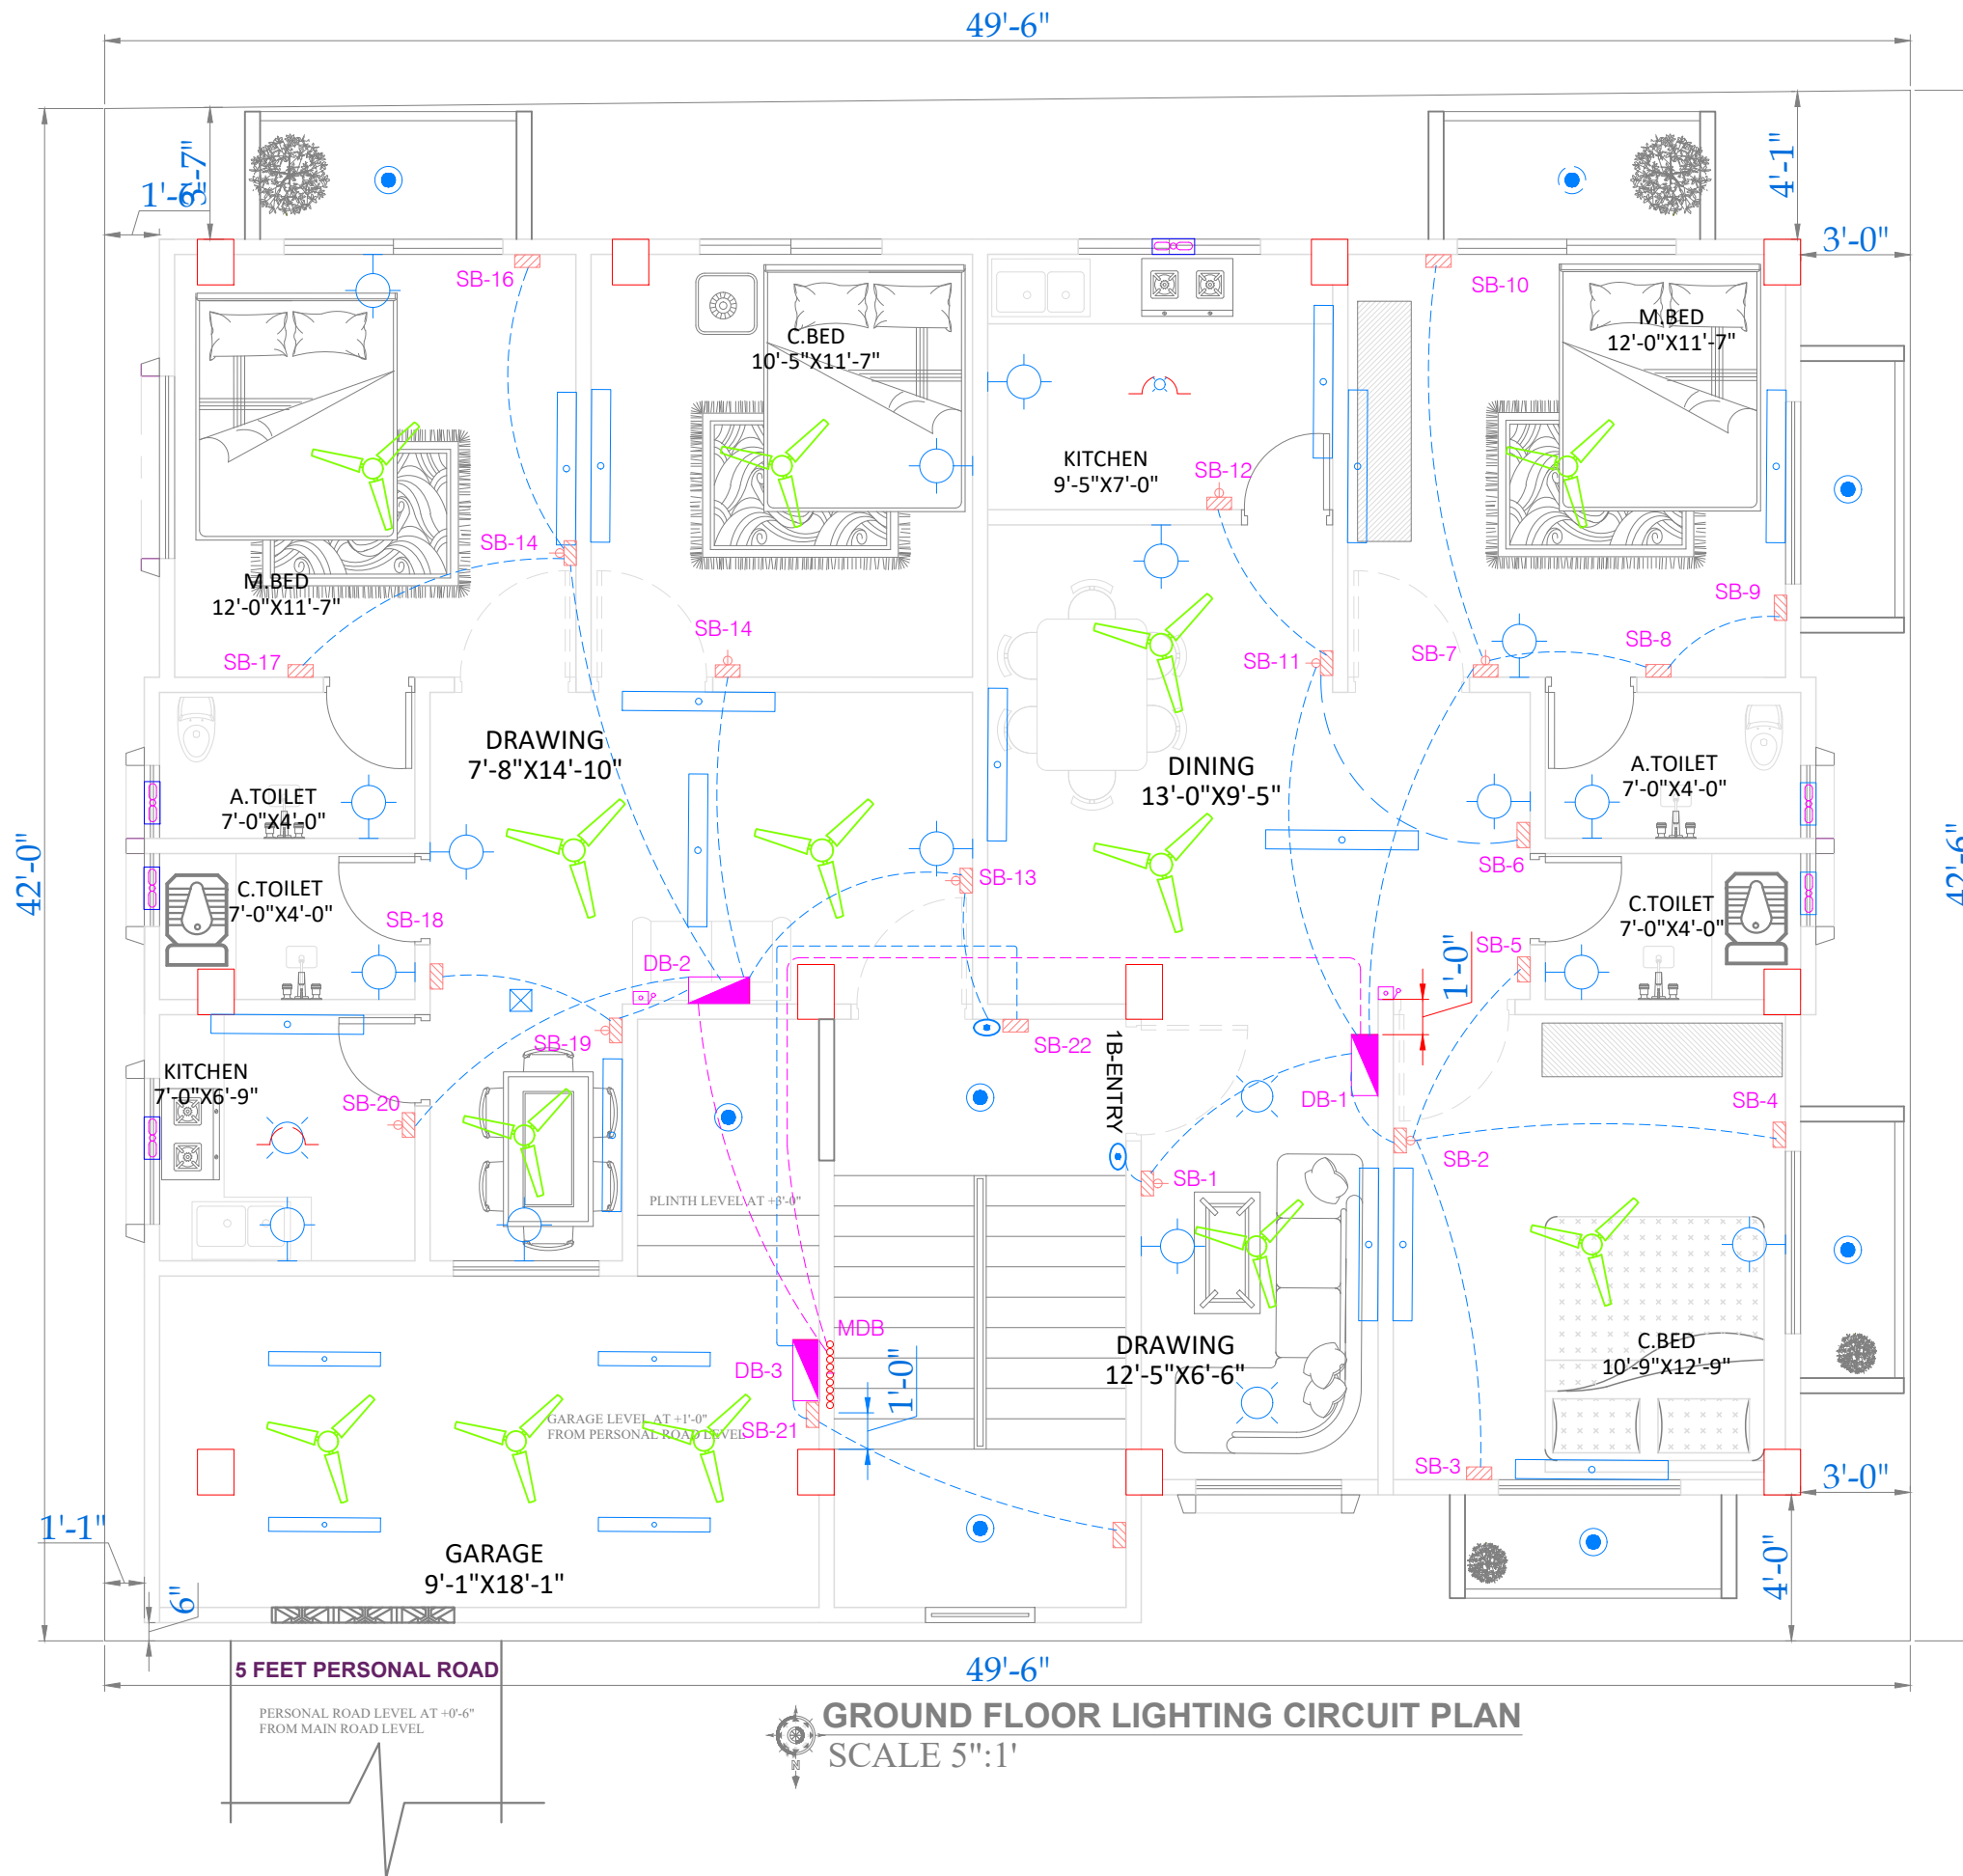


PROJECT NAME			
G+4 STORIED RESIDENTIAL BUILDING AT HARINMARI, PALASHBARI MUNICIPALITY, GAIBANDHA			
CLIENT NAME			
MR. MD. REJAUL KARIM			
DRAWING TITLE			
Electrical Layout Plan.			
ENGINEER			
MD. RIYADUL ISLAM PRODHAN			
B. Sc in Civil Engg. NSU			
M.Sc in Civil Engg. AUST			
M.Sc in Soil Science. DU			
M.Sc in ESM. JU			
IEB. REG. NO: M-45122			
MAHBUB KARIM			
B. Sc in Civil Engg. NSU			
M. Sc in Civil Engg. BUET			
M.Sc in Civil Engg. CDU (AUSTRALIA)			
IEB. REG. NO: M-45123			
ABDULLAH-AL-FOYSAL			
B. Sc in EEE; EASTERN UNIVERSITY			
Diploma in Electrical; ICST			
IEB. REG. NO: PENDING			
APPROVED BY			
ELECTRICAL LAYOUT DRAWN BY			
ABDULLAH-AL-FOYSAL			
CONSULTANT			
Prodhan Design & Construction			
Address: 94/3, LEVEL-2, TALLABAGH, INDIRA ROAD, DHAKA-1215			
SITE OFFICE: M/S. TMRR ENTERPRISE, KALIBARI BAZAR, PALASHBARI MUNICIPALITY,GAIBANDHA.			
1	22/07/26	1ST,3RD,4TH FLOOR	
NO.	DATE	REVISION	BY
CAD BY:		SHEET NO:	
		9	
DATE:		SCALE:	
11/07/2026		5":1'	

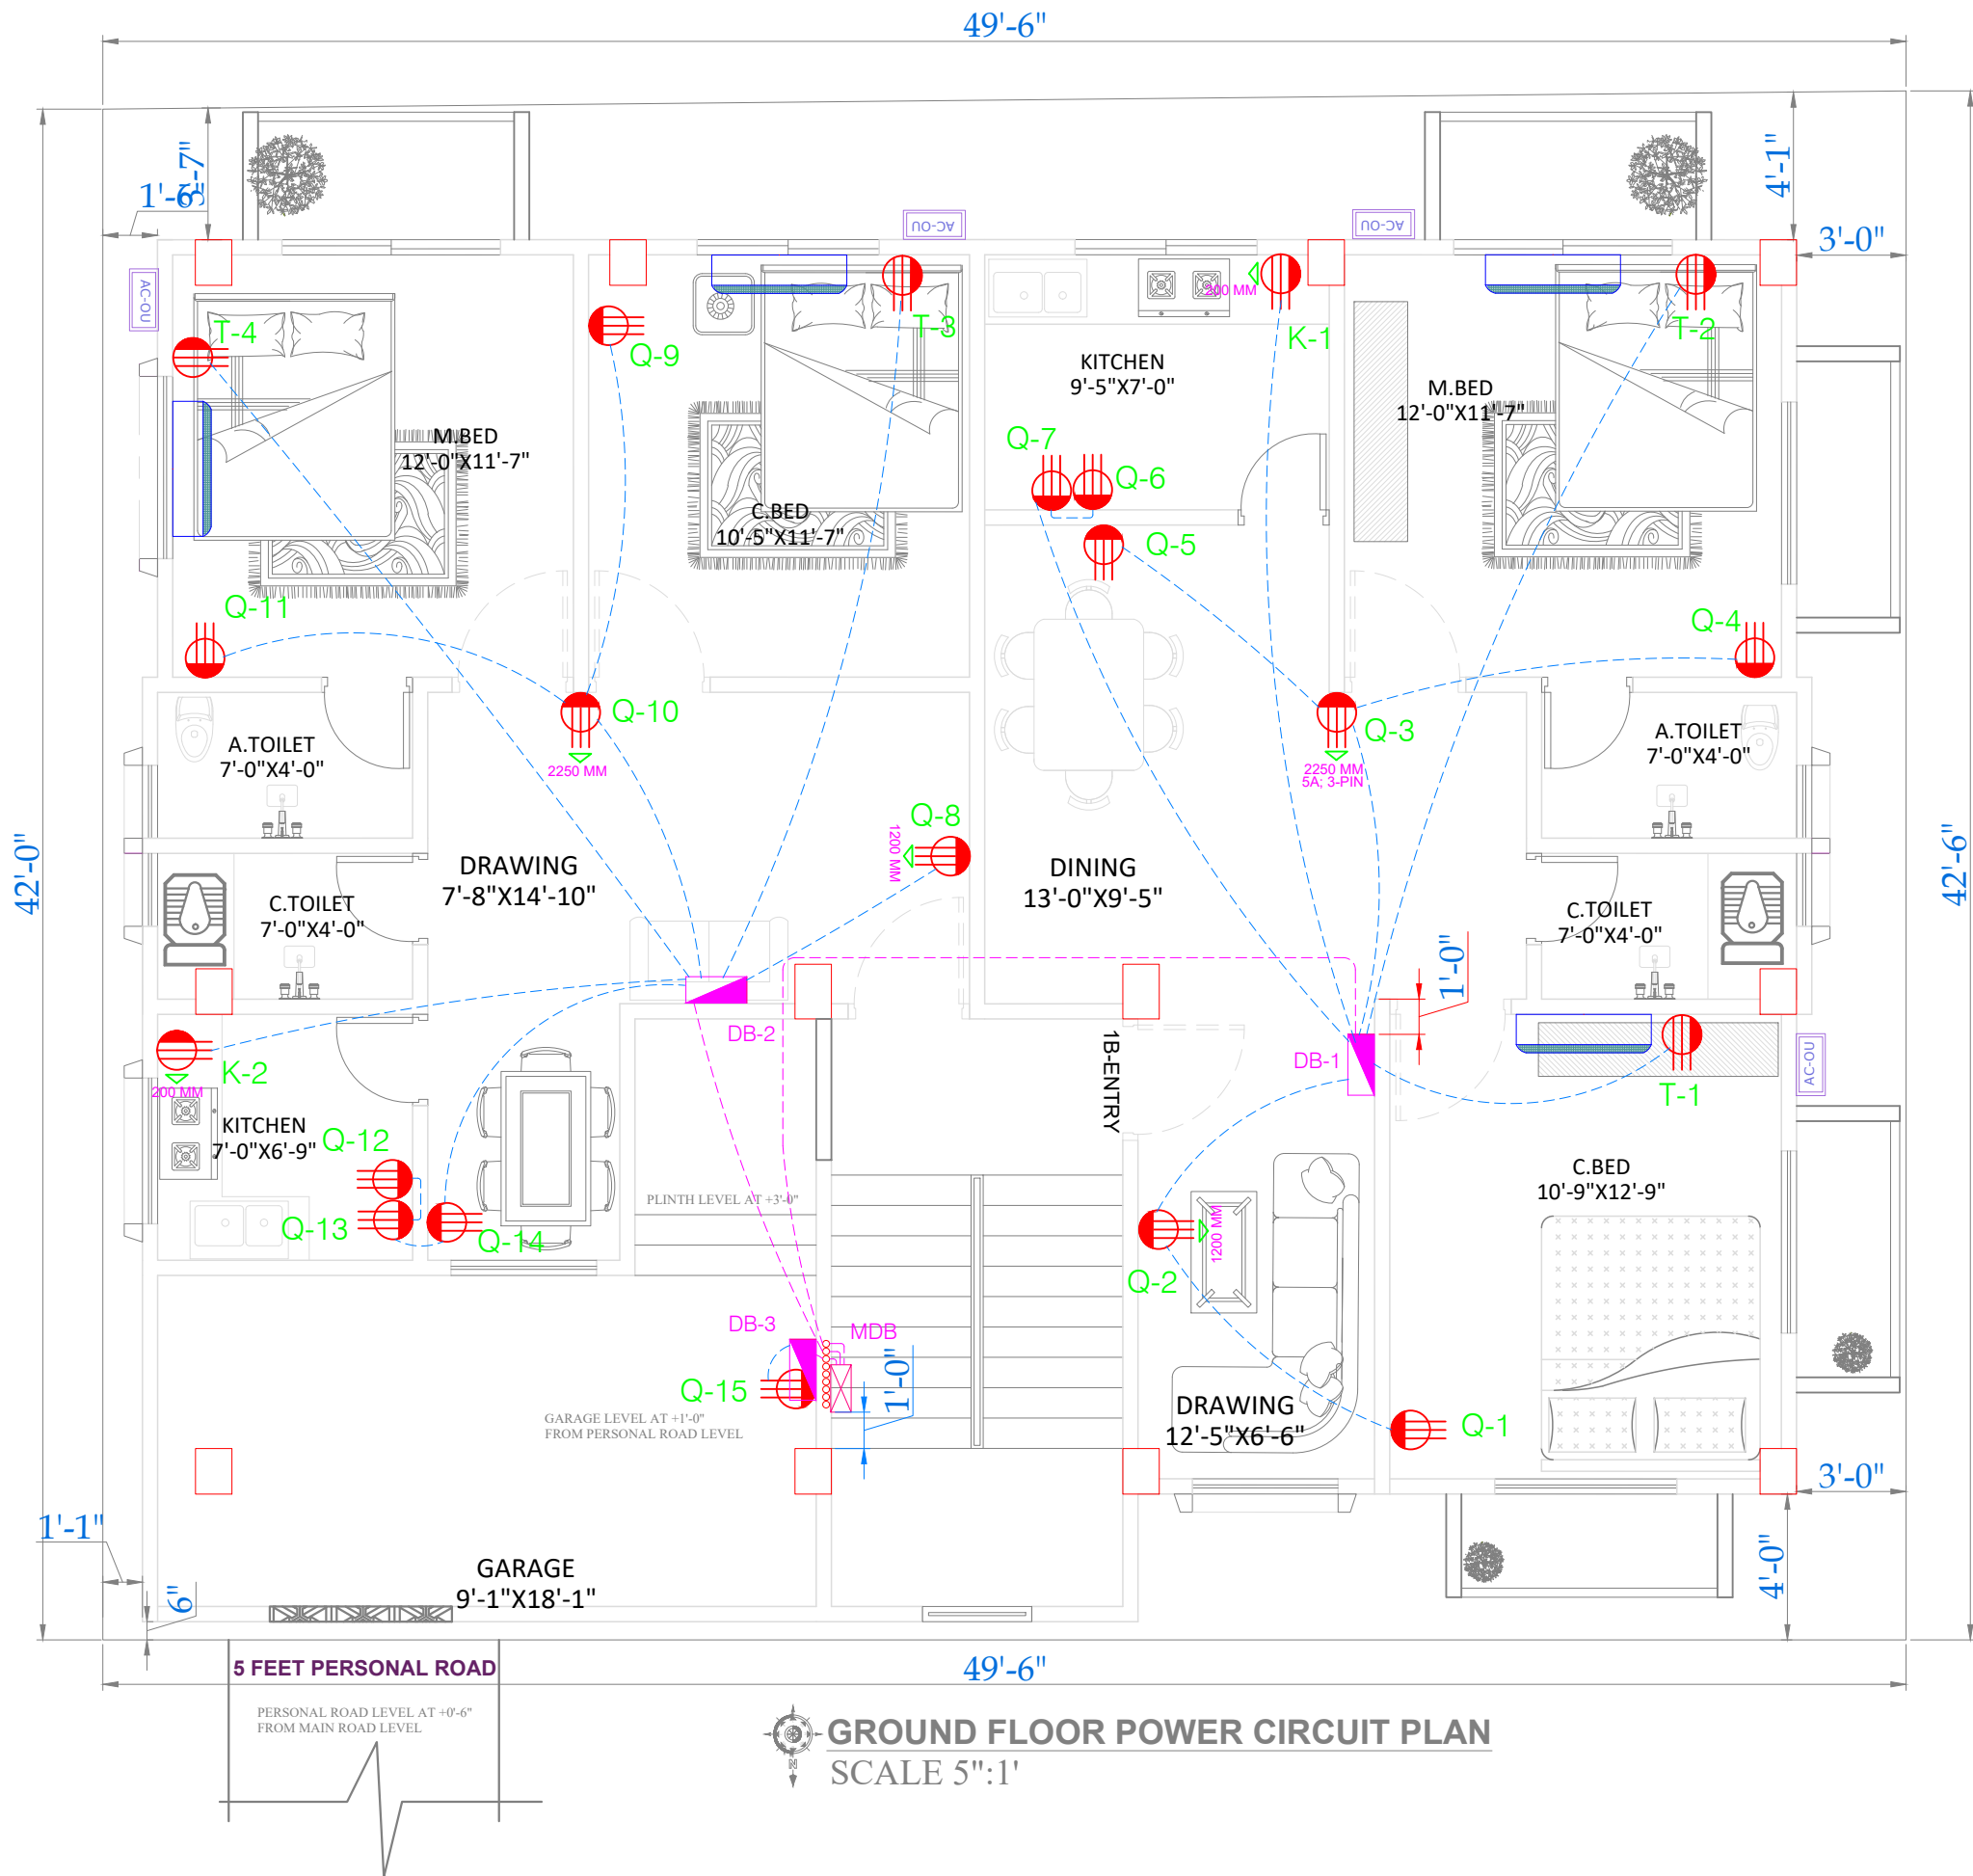

GROUND FLOOR POWER CIRCUIT PLAN
SCALE 5":1'

PROJECT NAME			
G+4 STORIED RESIDENTIAL BUILDING AT HARINMARI, PALASHBARI MUNICIPALITY, GAIBANDHA			
CLIENT NAME			
MR. MD. REJAUL KARIM			
DRAWING TITLE			
Electrical Layout Plan.			
ENGINEER			
MD. RIYADUL ISLAM PRODHAN			
B. Sc in Civil Engg. NSU			
M.Sc in Civil Engg. AUST			
M.Sc in Soil Science. DU			
M.Sc in ESM. JU			
IEB. REG. NO: M-45122			
MAHBUB KARIM			
B. Sc in Civil Engg. NSU			
M. Sc in Civil Engg. BUET			
M.Sc in Civil Engg. CDU (AUSTRALIA)			
IEB. REG. NO: M-45123			
ABDULLAH-AL-FOYSAL			
B. Sc in EEE; EASTERN UNIVERSITY			
Diploma in Electrical; ICST			
IEB. REG. NO: PENDING			
APPROVED BY			
ELECTRICAL LAYOUT DRAWN BY			
ABDULLAH-AL-FOYSAL			
CONSULTANT			
Prodhan Design & Construction			
Address: 94/3, LEVEL-2, TALLABAGH, INDIRA ROAD, DHAKA-1215			
SITE OFFICE: M/S. TMRR ENTERPRISE, KALIBARI BAZAR, PALASHBARI MUNICIPALITY,GAIBANDHA.			
1	22/07/26	1ST,3RD,4TH FLOOR	
NO.	DATE	REVISION	BY
CAD BY:		SHEET NO: 10	
DATE: 11/07/2026		SCALE: 5":1'	

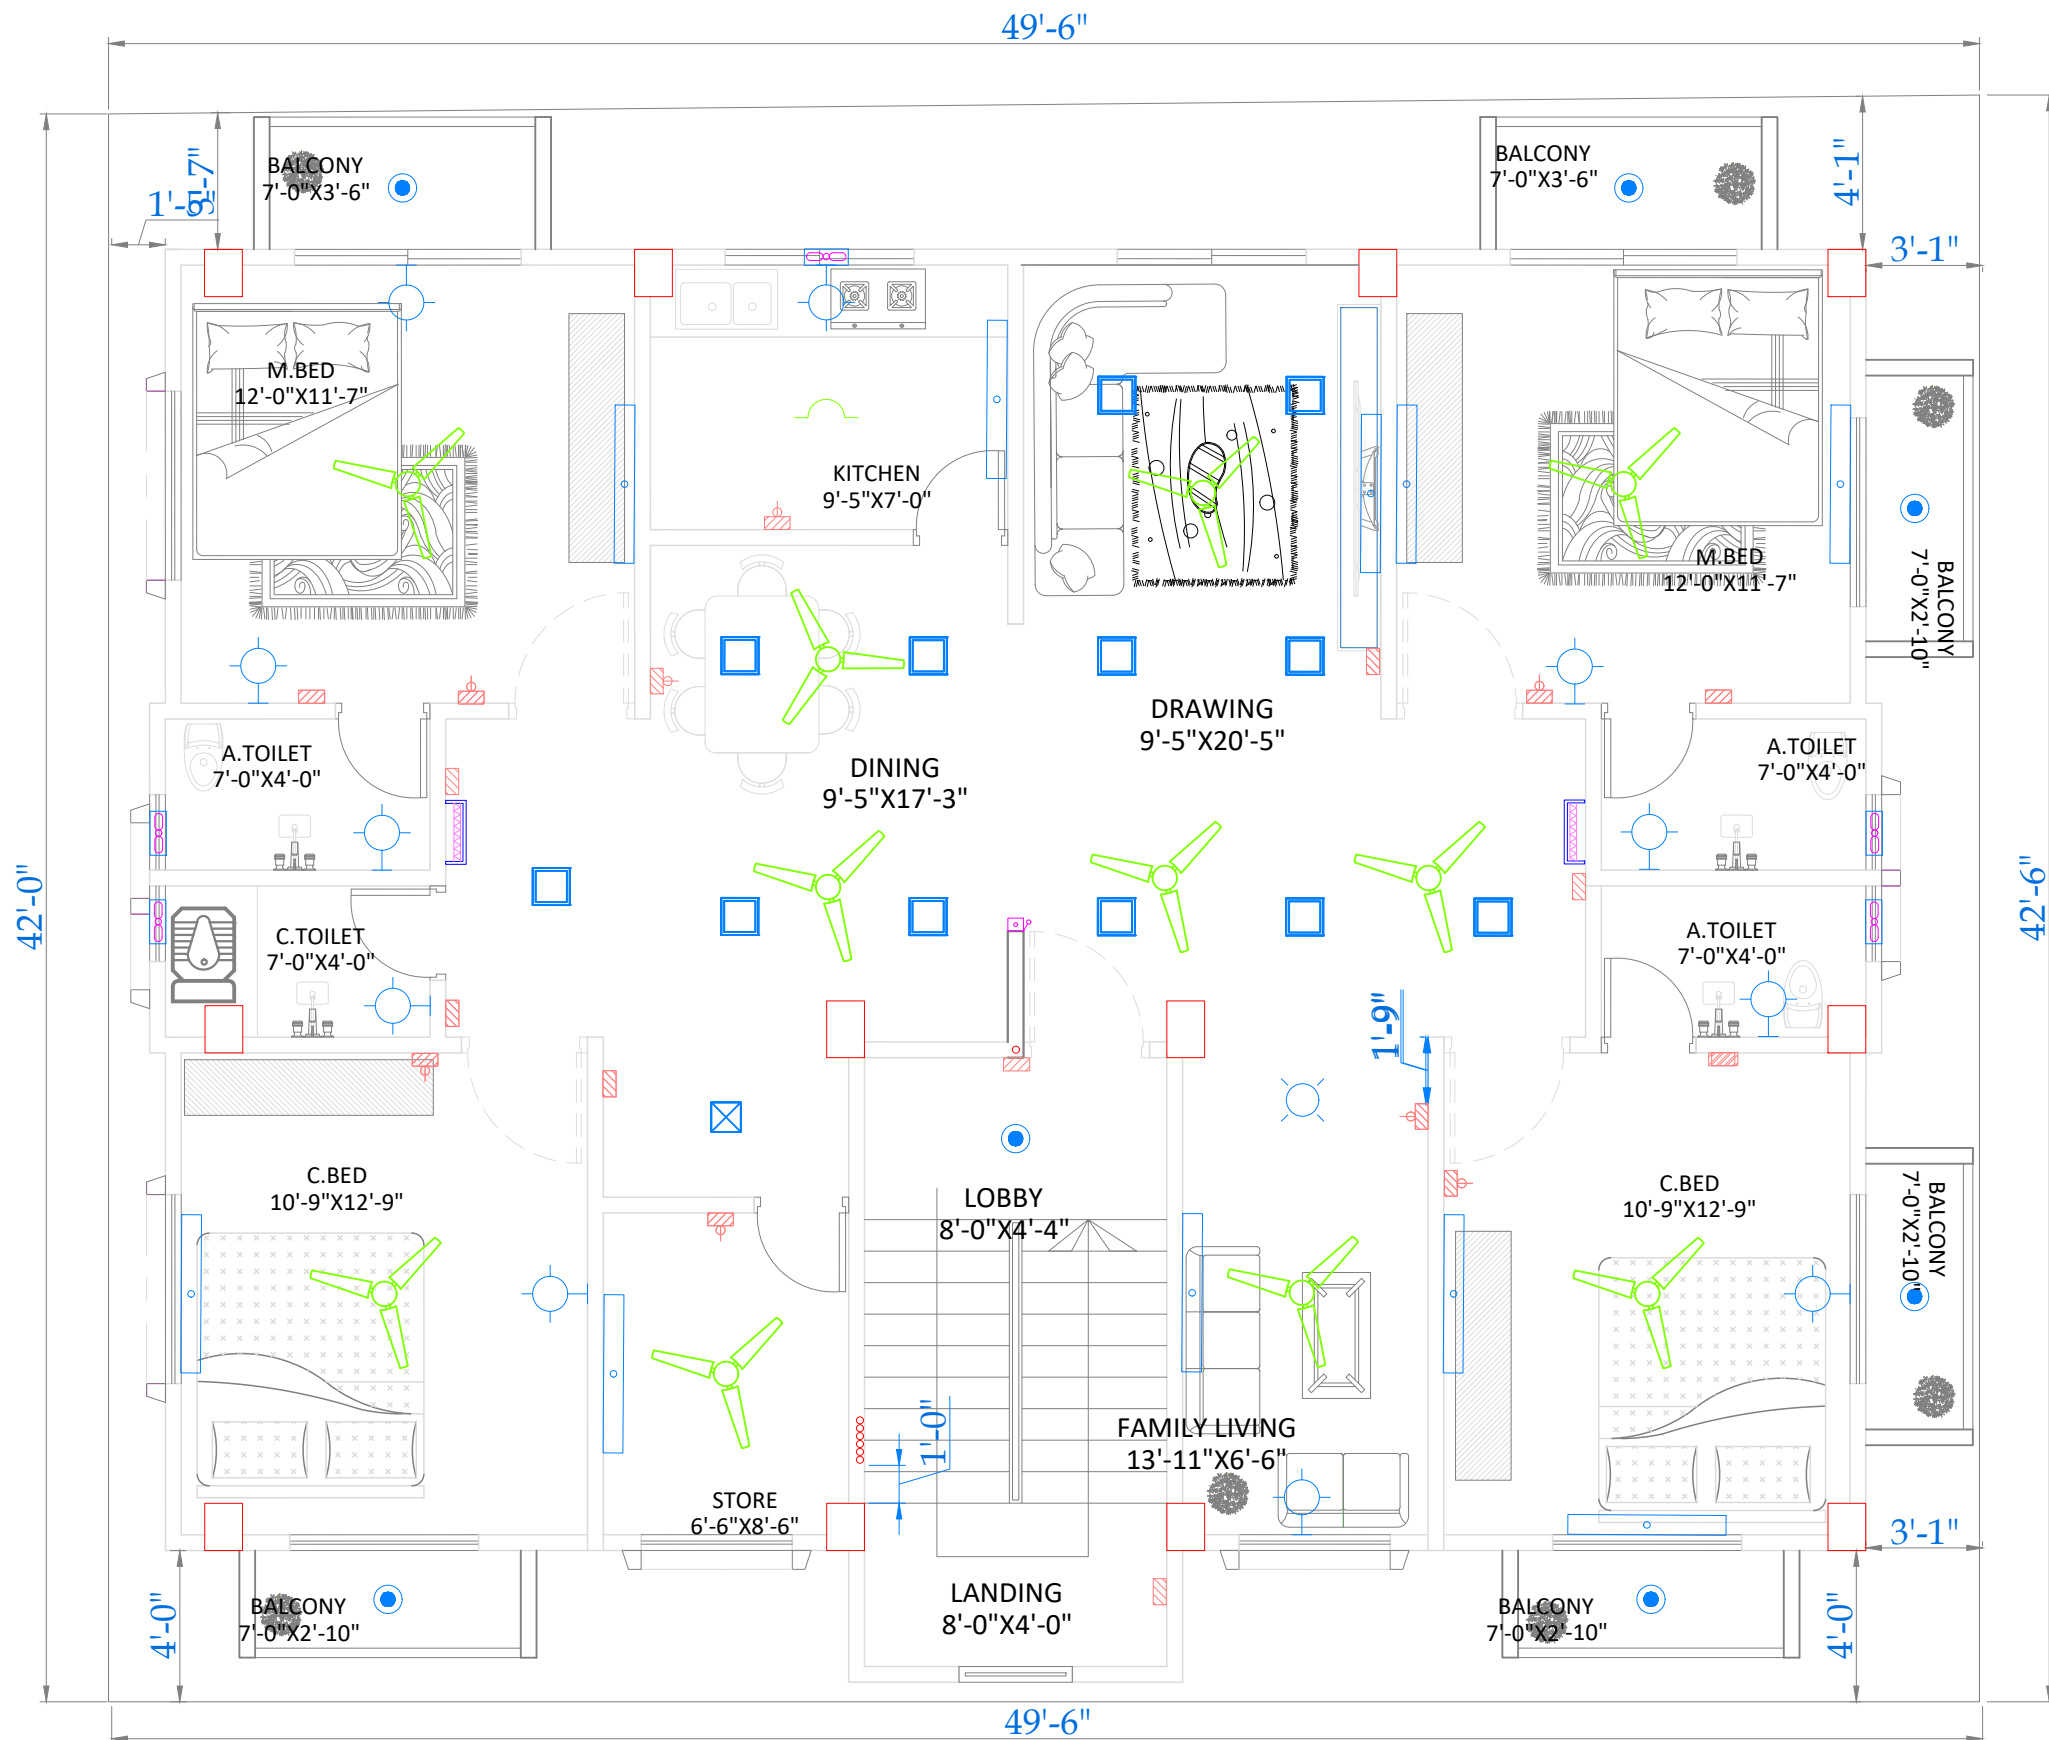

 **1ST FLOOR (1 UNIT) FIXTURE PLAN**
SCALE 5":1'

PROJECT NAME			
G+4 STORIED RESIDENTIAL BUILDING AT HARINMARI, PALASHBARI MUNICIPALITY, GAIBANDHA			
CLIENT NAME			
MR. MD. REJAUL KARIM			
DRAWING TITLE			
Electrical Layout Plan.			
ENGINEER			
MD. RIYADUL ISLAM PRODHAN B. Sc in Civil Engg. NSU M.Sc in Civil Engg. AUST M.Sc in Soil Science. DU M.Sc in ESM. JU IEB. REG. NO: M-45122			
MAHBUB KARIM B. Sc in Civil Engg. NSU M. Sc in Civil Engg. BUET M.Sc in Civil Engg. CDU (AUSTRALIA) IEB. REG. NO: M-45123			
ABDULLAH-AL-FOYSAL B. Sc in EEE; EASTERN UNIVERSITY Diploma in Electrical; ICST IEB. REG. NO: PENDING			
APPROVED BY			
ELECTRICAL LAYOUT DRAWN BY			
ABDULLAH-AL-FOYSAL			
CONSULTANT			
Prodhan Design & Construction Address: 94/3, LEVEL-2, TALLABAGH, INDIRA ROAD, DHAKA-1215 SITE OFFICE: M/S. TMRR ENTERPRISE, KALIBARI BAZAR, PALASHBARI MUNICIPALITY,GAIBANDHA.			
1	22/07/26	1ST,3RD,4TH FLOOR	
NO.	DATE	REVISION	BY
CAD BY:		SHEET NO: 11	
DATE: 11/07/2026		SCALE: 5":1'	

PROJECT NAME
G+4 STORIED RESIDENTIAL BUILDING AT
HARINMARI, PALASHBARI MUNICIPALITY,
GAIBANDHA

CLIENT NAME
MR. MD. REJAUL KARIM

DRAWING TITLE
Electrical Layout Plan.

ENGINEER
**MD. RIYADUL ISLAM
PRODHAN**
B. Sc in Civil Engg. NSU
M.Sc in Civil Engg. AUST
M.Sc in Soil Science. DU
M.Sc in ESM. JU
IEB. REG. NO: M-45122

MAHBUB KARIM
B. Sc in Civil Engg. NSU
M. Sc in Civil Engg. BUET
M.Sc in Civil Engg. CDU (AUSTRALIA)
IEB. REG. NO: M-45123


ABDULLAH-AL-FOYSAL
B. Sc in EEE; EASTERN UNIVERSITY
Diploma in Electrical; ICST
IEB. REG. NO: PENDING

APPROVED BY


ELECTRICAL LAYOUT DRAWN BY
ABDULLAH-AL-FOYSAL

CONSULTANT
Prodhan Design & Construction
Address: 94/3, LEVEL-2, TALLABAGH,
INDIRA ROAD, DHAKA-1215
SITE OFFICE: M/S. TMRR ENTERPRISE,
KALIBARI BAZAR, PALASHBARI
MUNICIPALITY,GAIBANDHA.

1	22/07/26	1ST,3RD,4TH FLOOR	
NO.	DATE	REVISION	BY
CAD BY:		SHEET NO: 12	
DATE: 11/07/2026		SCALE: 5":1'	

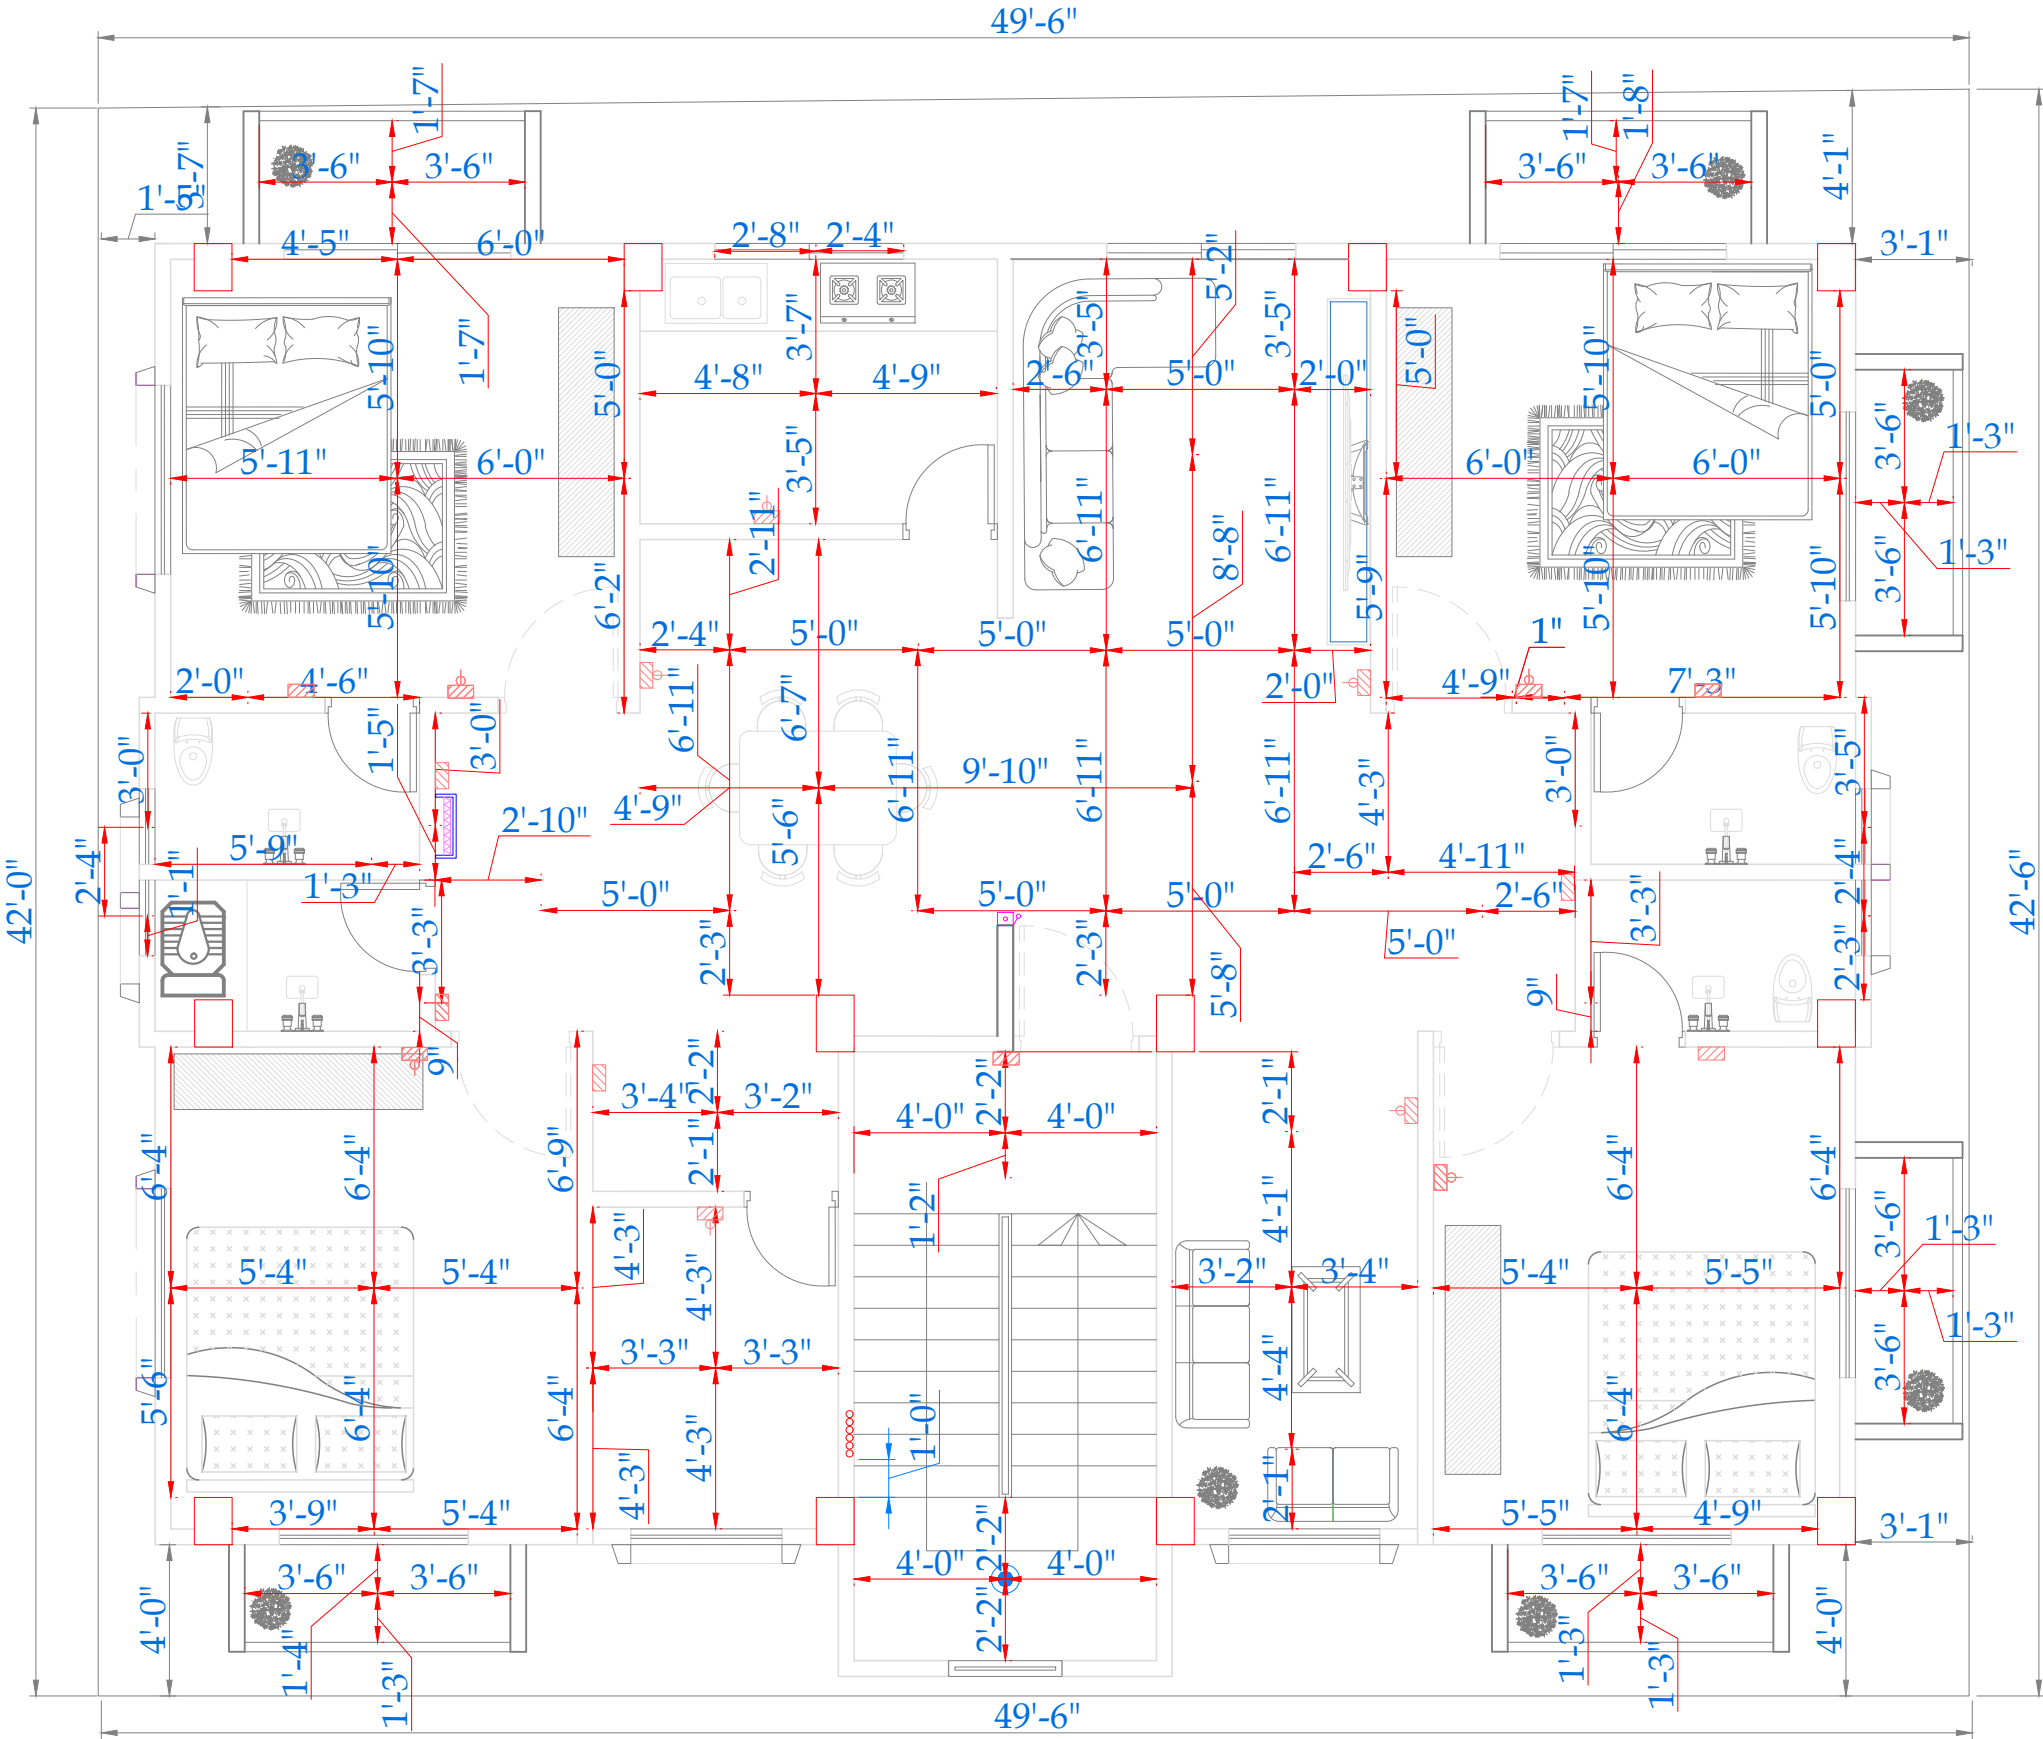


1ST FLOOR (1 UNIT) FIXTURE DIMENSION PLAN
SCALE 5":1'

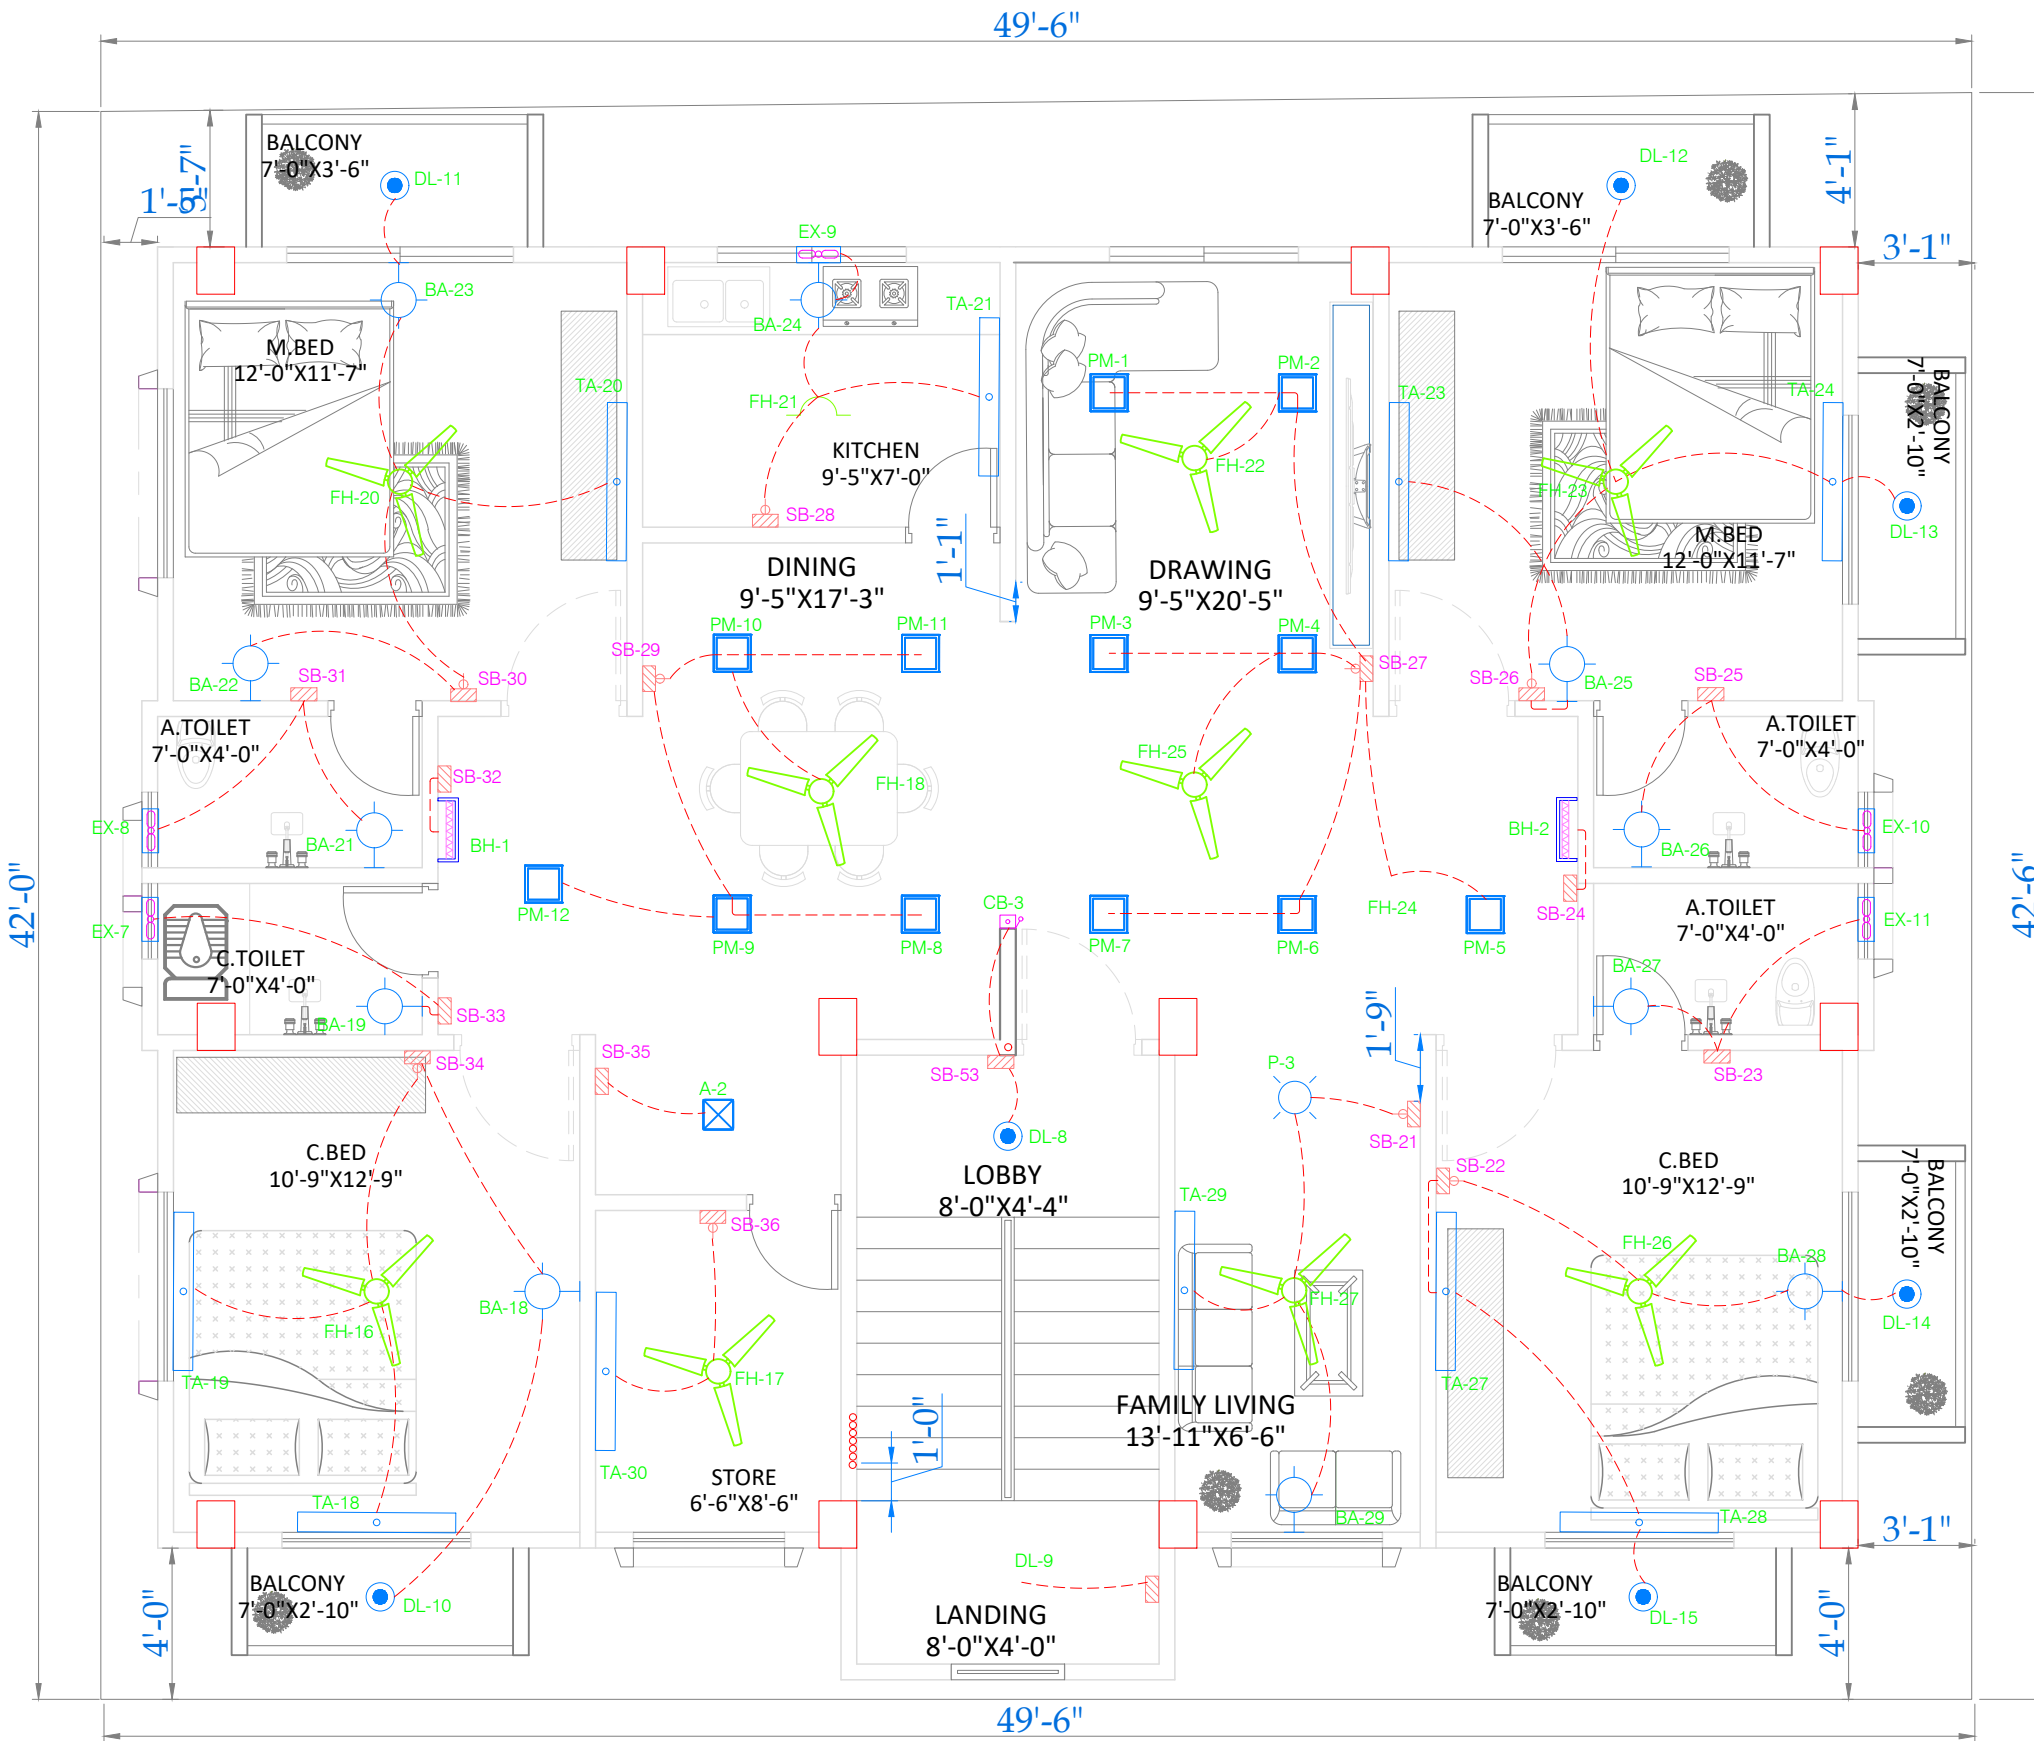

1ST FLOOR (1 UNIT) LIGHTING FIXTURE COUNDUET PLAN
SCALE 5":1'

PROJECT NAME			
G+4 STORIED RESIDENTIAL BUILDING AT HARINMARI, PALASHBARI MUNICIPALITY, GAIBANDHA			
CLIENT NAME			
MR. MD. REJAUL KARIM			
DRAWING TITLE			
Electrical Layout Plan.			
ENGINEER			
MD. RIYADUL ISLAM PRODHAN			
B. Sc in Civil Engg. NSU			
M.Sc in Civil Engg. AUST			
M.Sc in Soil Science. DU			
M.Sc in ESM. JU			
IEB. REG. NO: M-45122			
MAHBUB KARIM			
B. Sc in Civil Engg. NSU			
M. Sc in Civil Engg. BUET			
M.Sc in Civil Engg. CDU (AUSTRALIA)			
IEB. REG. NO: M-45123			
ABDULLAH-AL-FOYSAL			
B. Sc in EEE; EASTERN UNIVERSITY			
Diploma in Electrical; ICST			
IEB. REG. NO: PENDING			
APPROVED BY			
ELECTRICAL LAYOUT DRAWN BY			
ABDULLAH-AL-FOYSAL			
CONSULTANT			
Prodhan Design & Construction			
Address: 94/3, LEVEL-2, TALLABAGH, INDIRA ROAD, DHAKA-1215			
SITE OFFICE: M/S. TMRR ENTERPRISE, KALIBARI BAZAR, PALASHBARI MUNICIPALITY,GAIBANDHA.			
1	22/07/26	1ST,3RD,4TH FLOOR	
NO.	DATE	REVISION	BY
CAD BY:		SHEET NO:	
		13	
DATE:		SCALE:	
11/07/2026		5":1'	

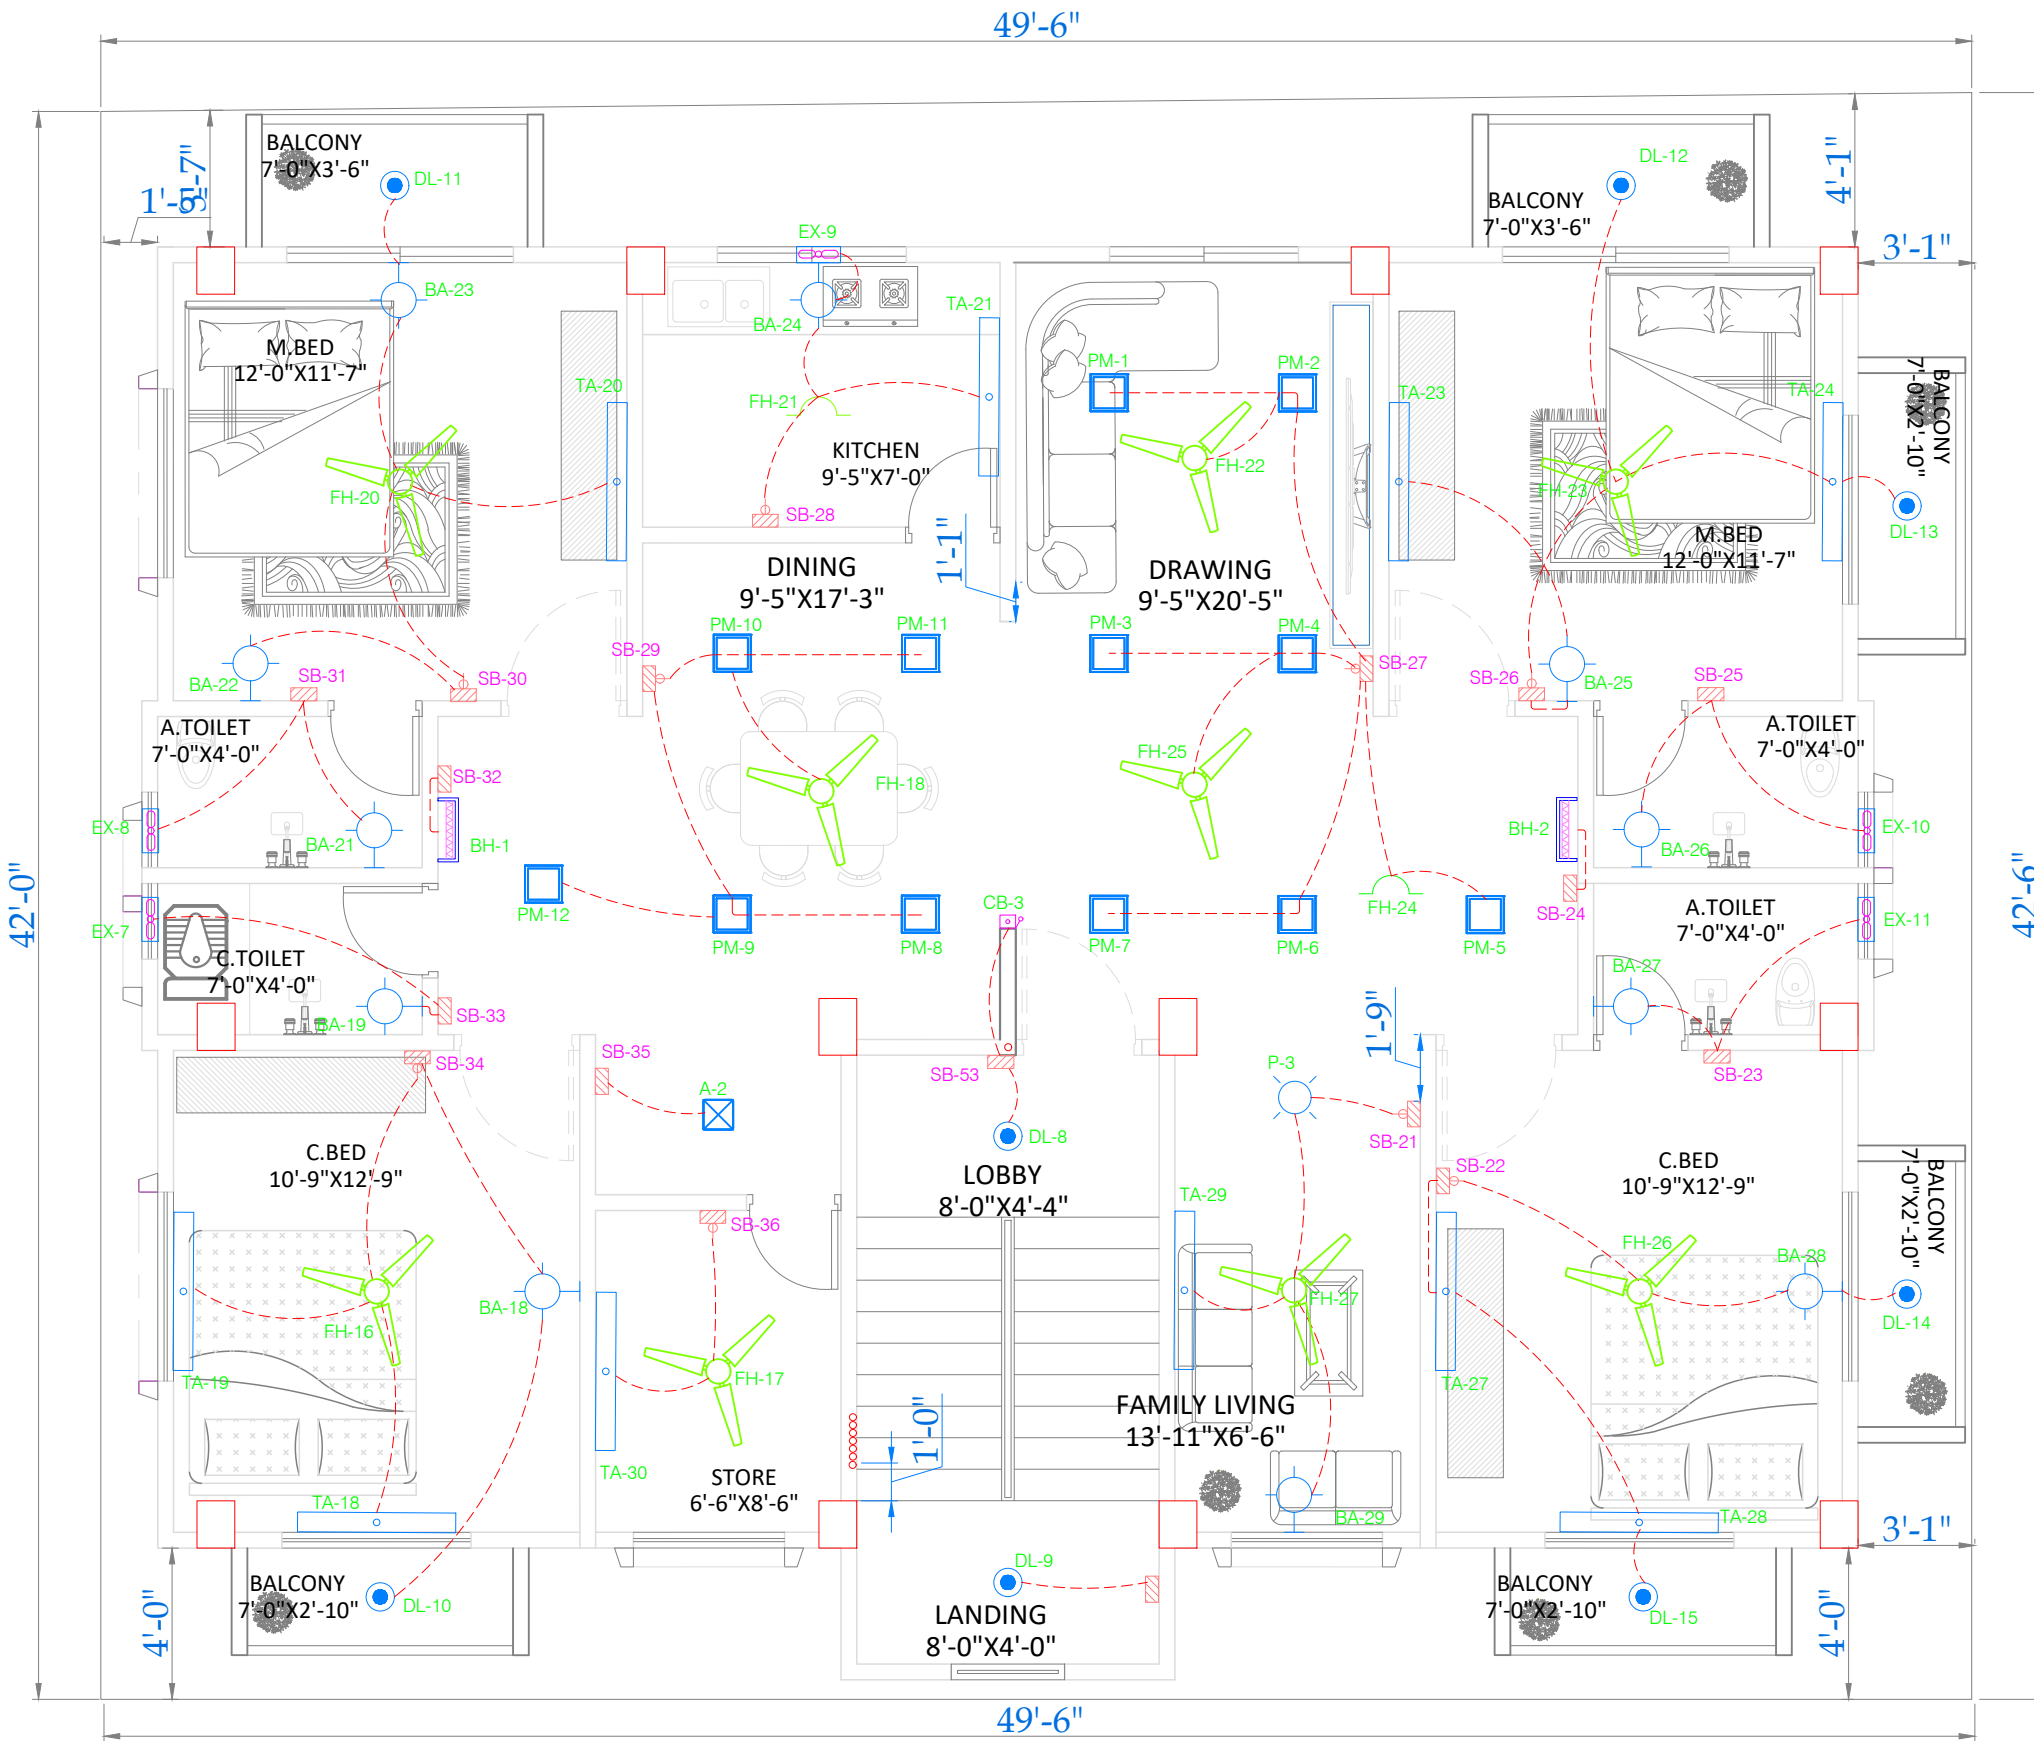

1ST FLOOR (1 UNIT) LIGHTING FIXTURE COUNDUET PLAN
SCALE 5":1'

PROJECT NAME
G+4 STORIED RESIDENTIAL BUILDING AT
HARINMARI, PALASHBARI MUNICIPALITY,
GAIBANDHA

CLIENT NAME
MR. MD. REJAUL KARIM

DRAWING TITLE
Electrical Layout Plan.

ENGINEER
**MD. RIYADUL ISLAM
PRODHAN**
B. Sc in Civil Engg. NSU
M.Sc in Civil Engg. AUST
M.Sc in Soil Science. DU
M.Sc in ESM. JU
IEB. REG. NO: M-45122

MAHBUB KARIM
B. Sc in Civil Engg. NSU
M. Sc in Civil Engg. BUET
M.Sc in Civil Engg. CDU (AUSTRALIA)
IEB. REG. NO: M-45123


ABDULLAH-AL-FOYSAL
B. Sc in EEE; EASTERN UNIVERSITY
Diploma in Electrical; ICST
IEB. REG. NO: PENDING

APPROVED BY

ELECTRICAL LAYOUT DRAWN BY
ABDULLAH-AL-FOYSAL


CONSULTANT
Prodhan Design & Construction
Address: 94/3, LEVEL-2, TALLABAGH,
INDIRA ROAD, DHAKA-1215
SITE OFFICE: M/S. TMRR ENTERPRISE,
KALIBARI BAZAR, PALASHBARI
MUNICIPALITY,GAIBANDHA.

1	22/07/26	1ST,3RD,4TH FLOOR	
NO.	DATE	REVISION	BY
CAD BY:		SHEET NO: 14	
DATE: 11/07/2026		SCALE: 5":1'	

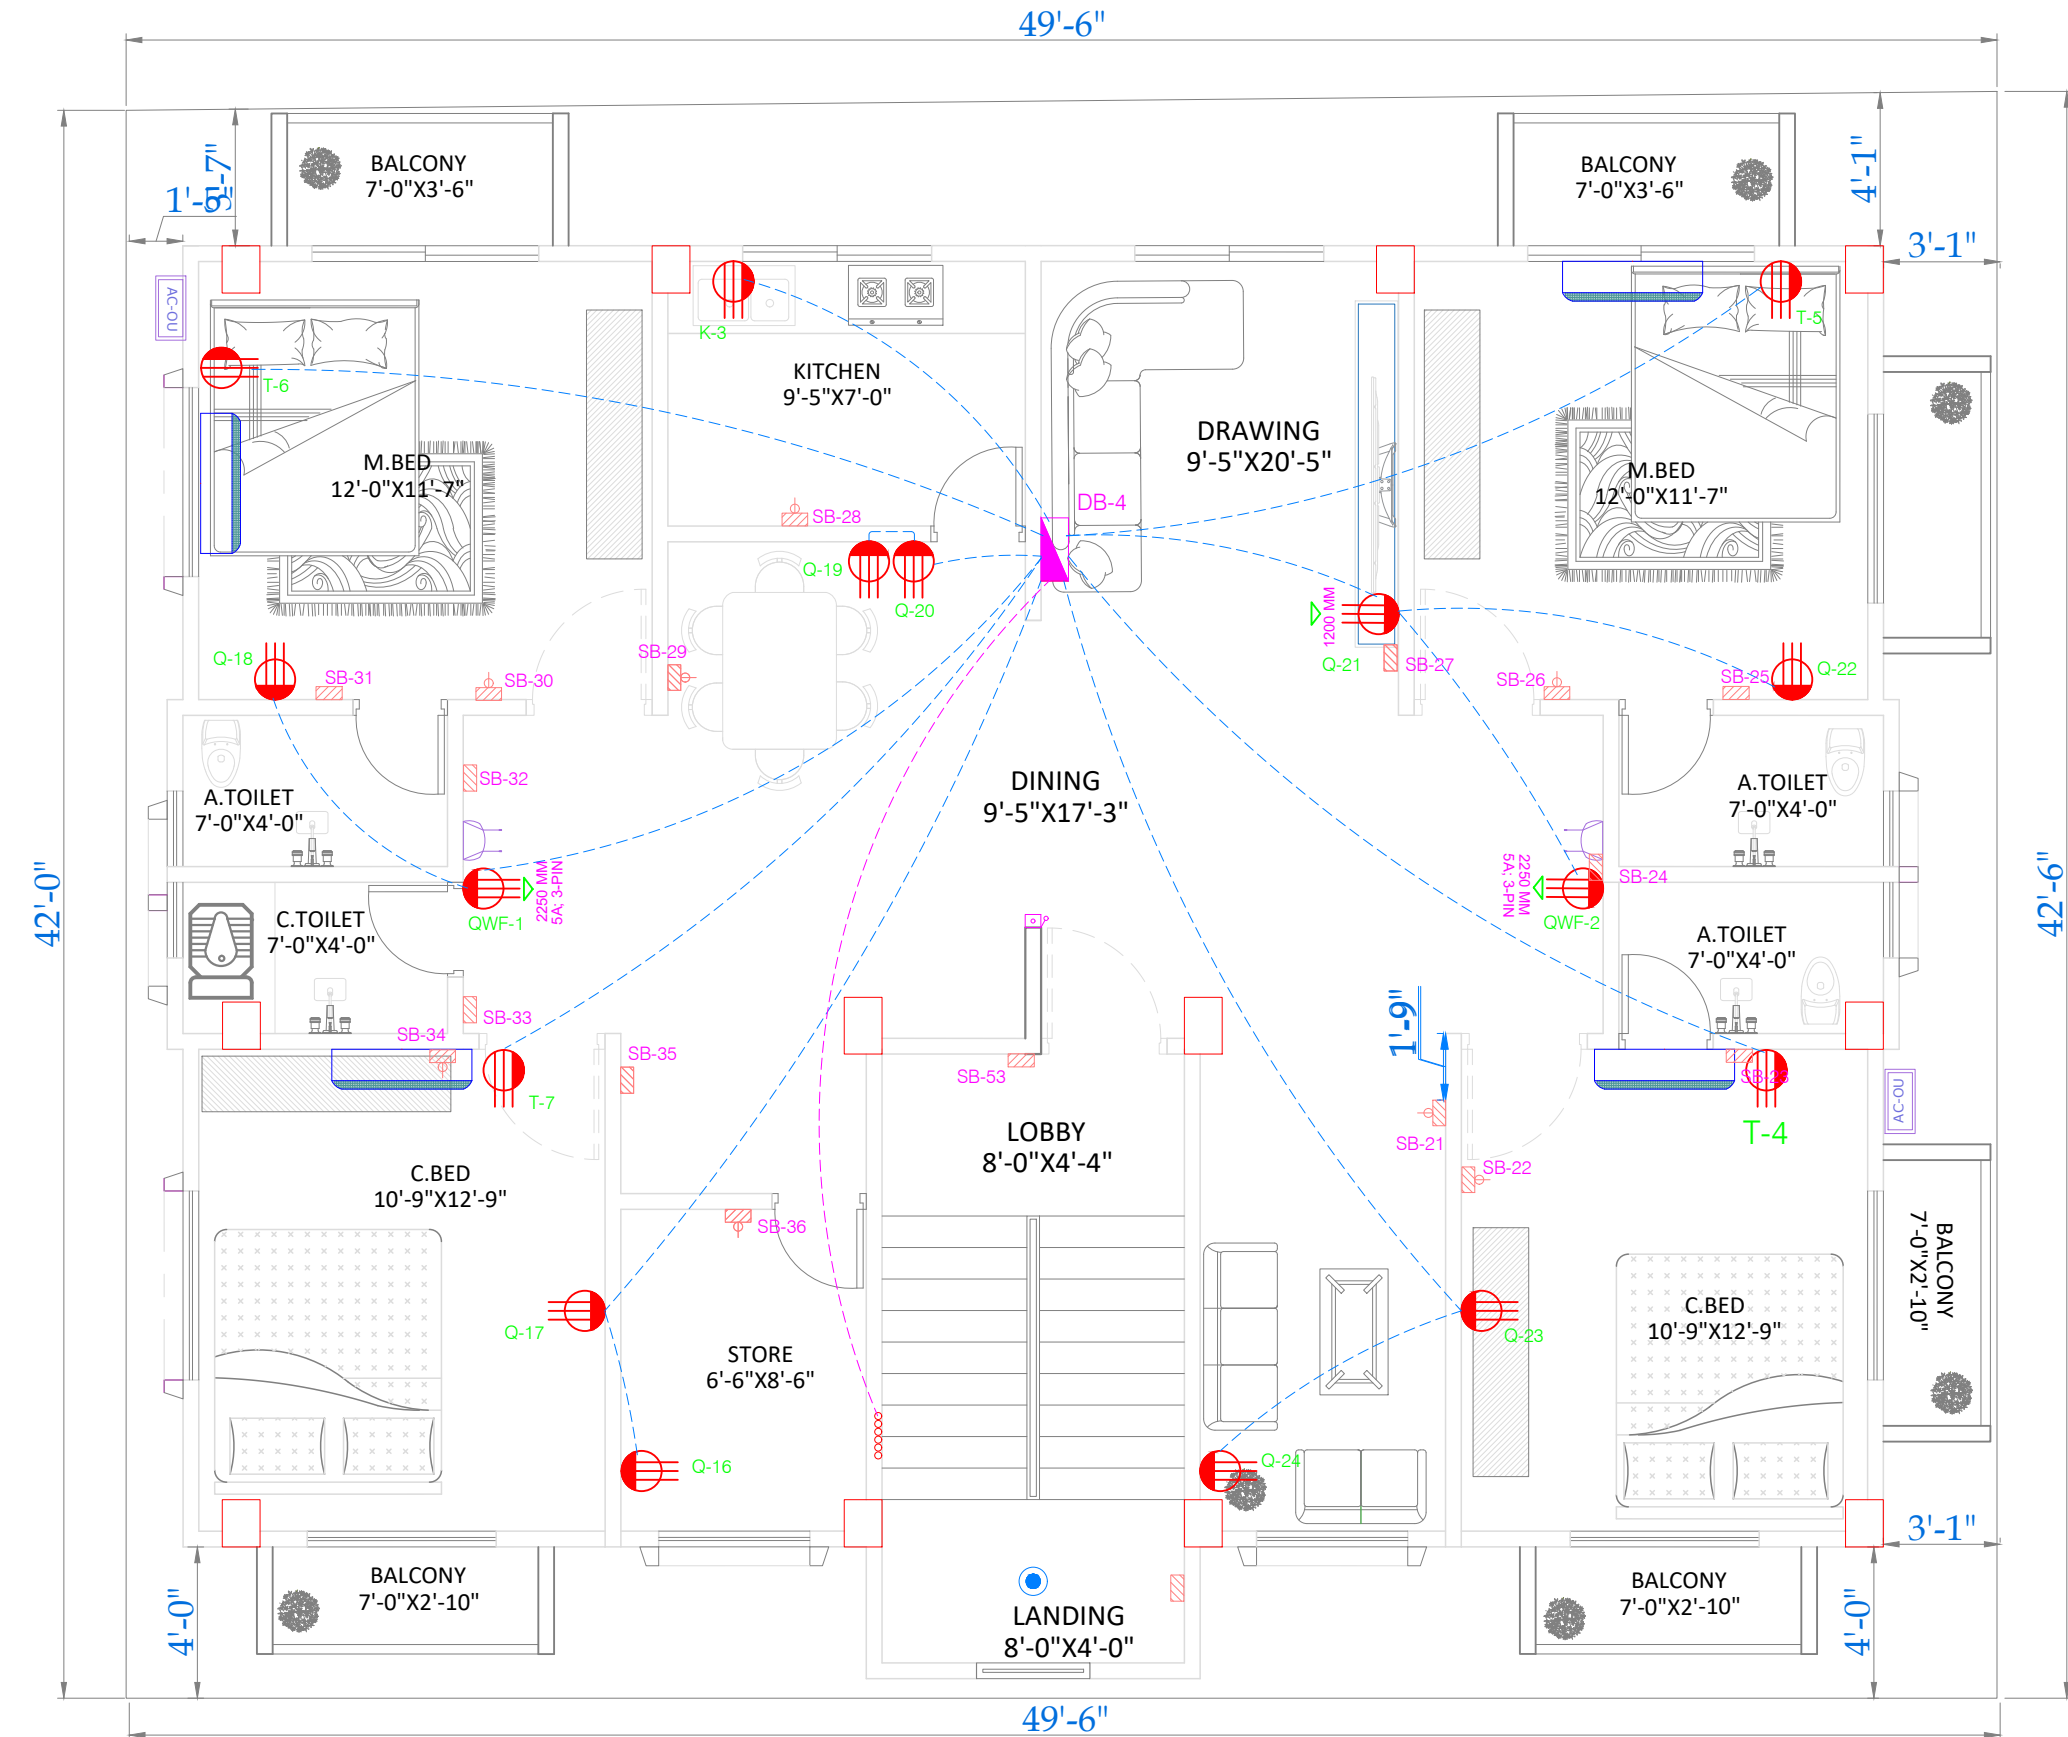


1ST FLOOR (1 UNIT) POWER CIRCUIT PLAN
SCALE 5":1'

PROJECT NAME			
G+4 STORIED RESIDENTIAL BUILDING AT HARINMARI, PALASHBARI MUNICIPALITY, GAIBANDHA			
CLIENT NAME			
MR. MD. REJAUL KARIM			
DRAWING TITLE			
Electrical Layout Plan.			
ENGINEER			
MD. RIYADUL ISLAM PRODHAN			
B. Sc in Civil Engg. NSU			
M.Sc in Civil Engg. AUST			
M.Sc in Soil Science. DU			
M.Sc in ESM. JU			
IEB. REG. NO: M-45122			
MAHBUB KARIM			
B. Sc in Civil Engg. NSU			
M. Sc in Civil Engg. BUET			
M.Sc in Civil Engg. CDU (AUSTRALIA)			
IEB. REG. NO: M-45123			
ABDULLAH-AL-FOYSAL			
B. Sc in EEE; EASTERN UNIVERSITY			
Diploma in Electrical; ICST			
IEB. REG. NO: PENDING			
APPROVED BY			
ELECTRICAL LAYOUT DRAWN BY			
ABDULLAH-AL-FOYSAL			
CONSULTANT			
Prodhan Design & Construction			
Address: 94/3, LEVEL-2, TALLABAGH, INDIRA ROAD, DHAKA-1215			
SITE OFFICE: M/S. TMRR ENTERPRISE, KALIBARI BAZAR, PALASHBARI MUNICIPALITY,GAIBANDHA.			
1	22/07/26	1ST,3RD,4TH FLOOR	
NO.	DATE	REVISION	BY
CAD BY:		SHEET NO:	
		15	
DATE:		SCALE:	
11/07/2026		5":1'	

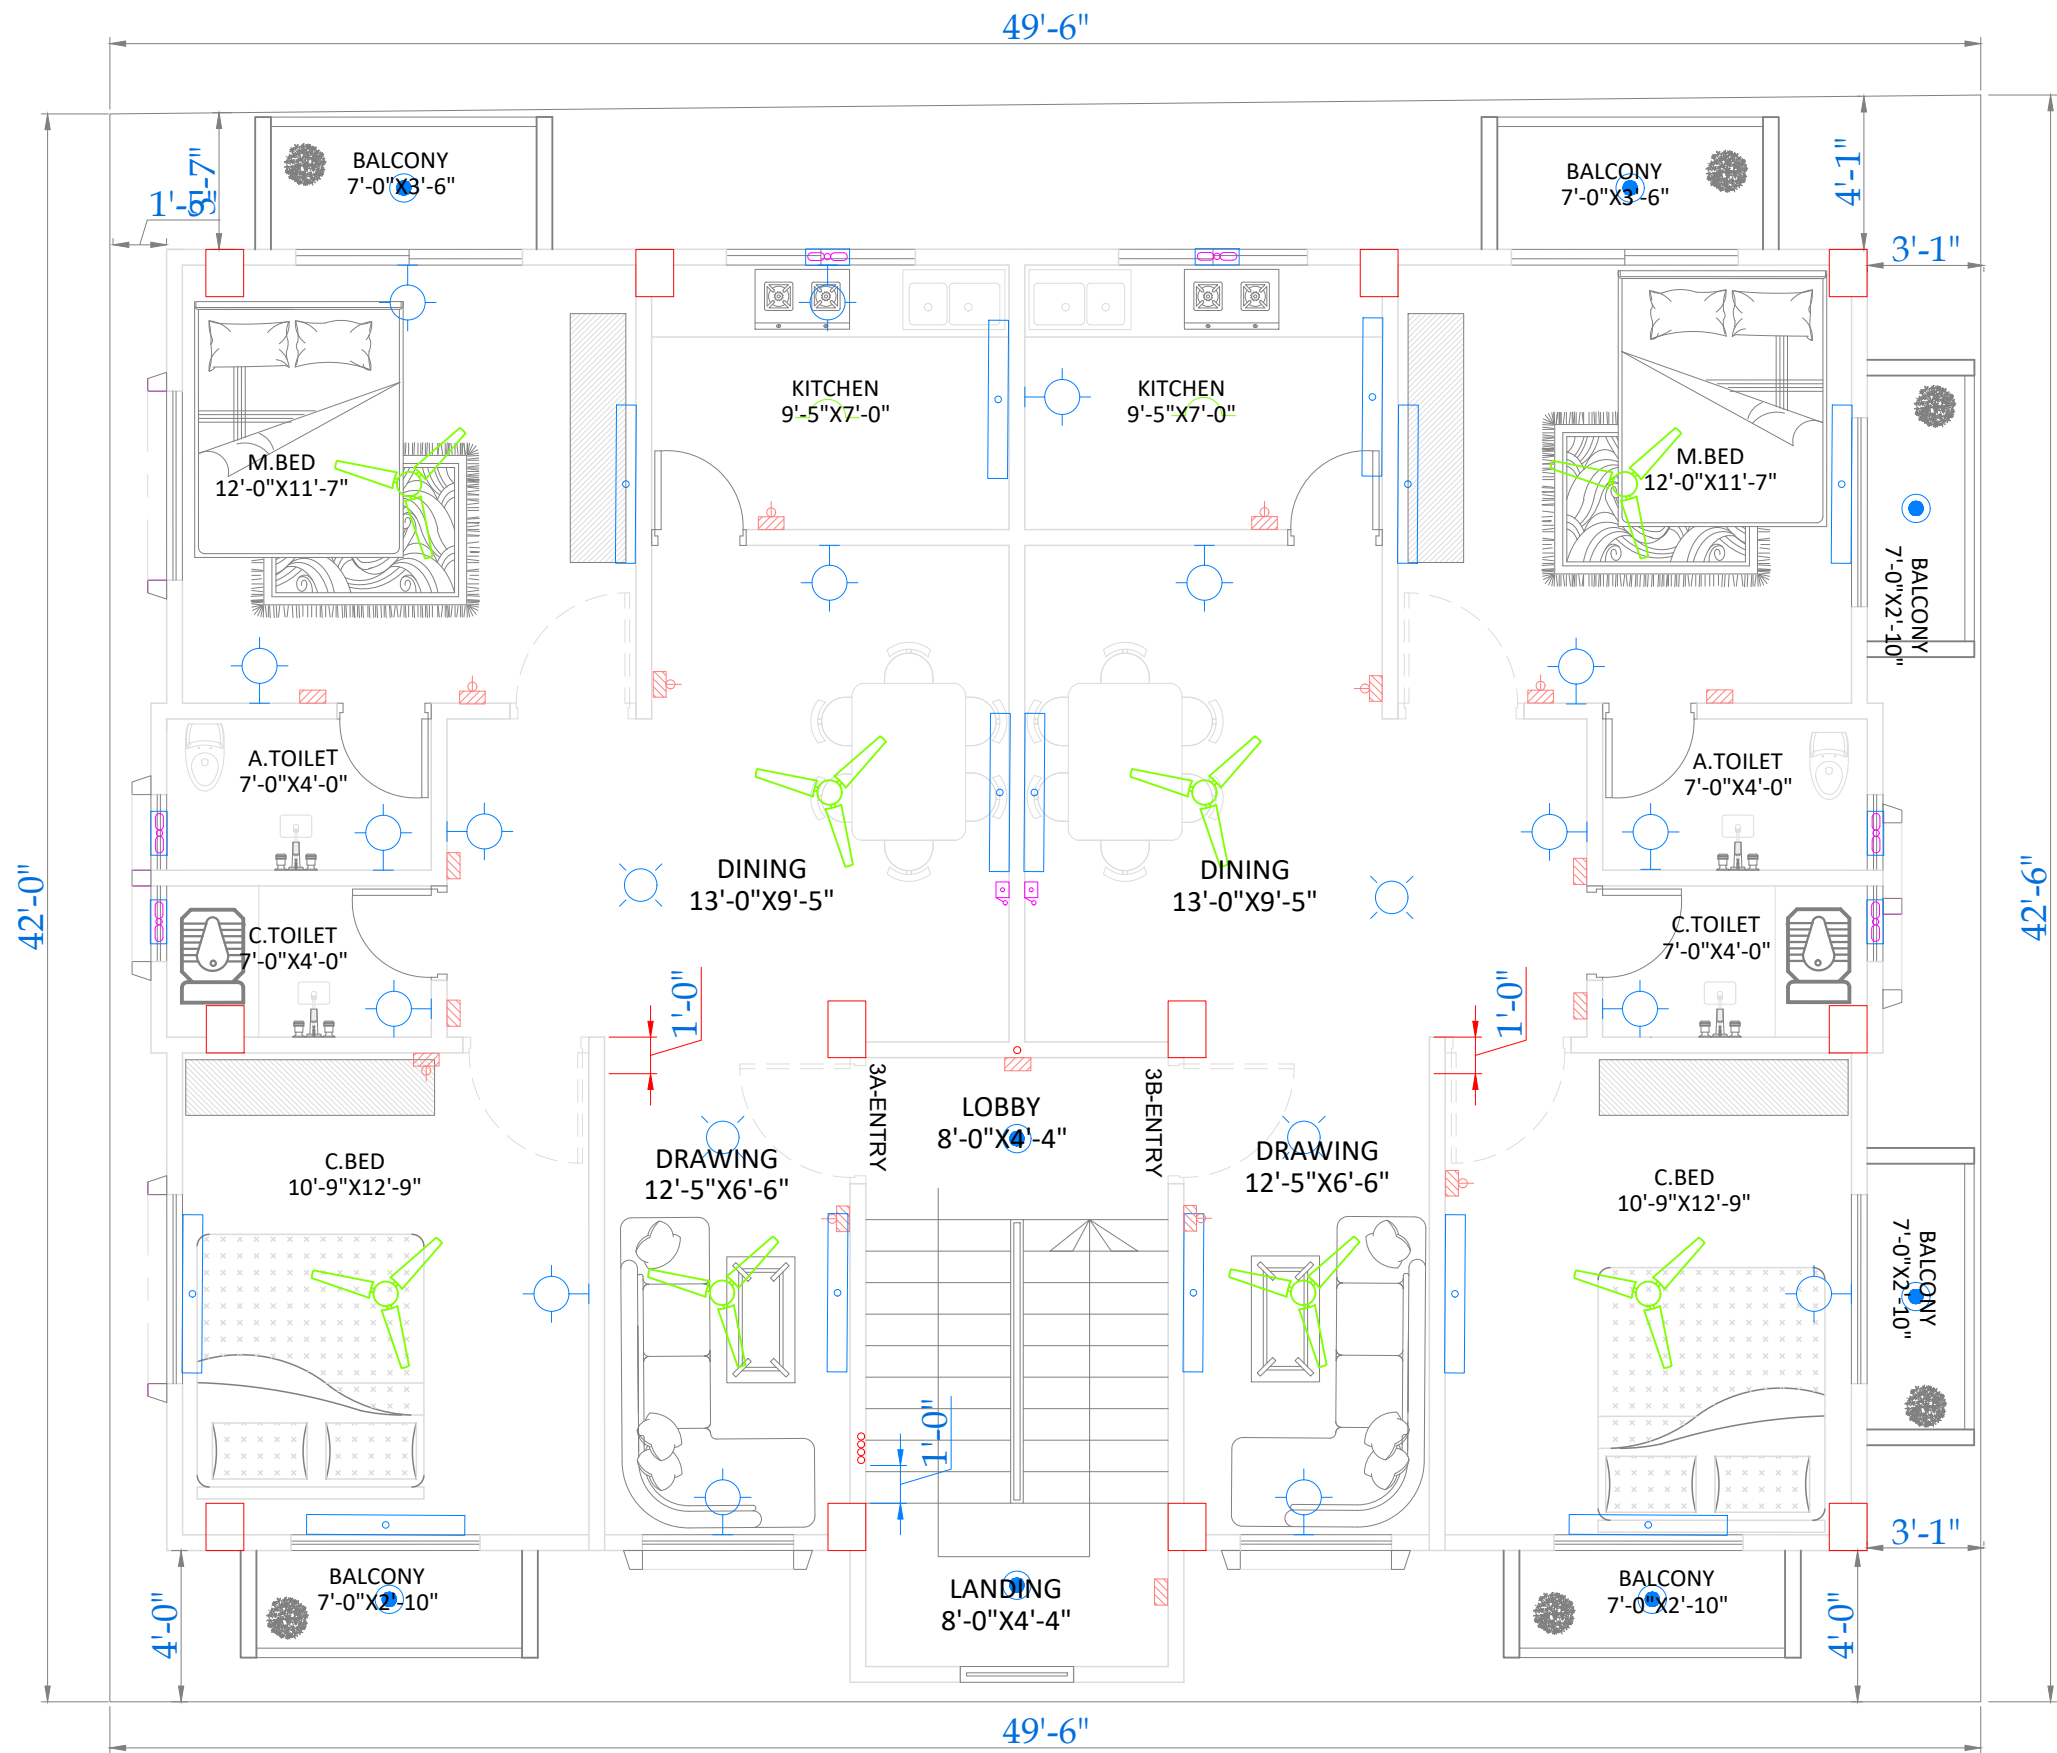


2ND& 3RD FLOOR FIXTURE PLAN
SCALE 5":1'

PROJECT NAME			
G+4 STORIED RESIDENTIAL BUILDING AT HARINMARI, PALASHBARI MUNICIPALITY, GAIBANDHA			
CLIENT NAME			
MR. MD. REJAUL KARIM			
DRAWING TITLE			
Electrical Layout Plan.			
ENGINEER			
MD. RIYADUL ISLAM PRODHAN			
B. Sc in Civil Engg. NSU			
M.Sc in Civil Engg. AUST			
M.Sc in Soil Science. DU			
M.Sc in ESM. JU			
IEB. REG. NO: M-45122			
MAHBUB KARIM			
B. Sc in Civil Engg. NSU			
M. Sc in Civil Engg. BUET			
M.Sc in Civil Engg. CDU (AUSTRALIA)			
IEB. REG. NO: M-45123			
ABDULLAH-AL-FOYSAL			
B. Sc in EEE; EASTERN UNIVERSITY			
Diploma in Electrical; ICST			
IEB. REG. NO: PENDING			
APPROVED BY			
ELECTRICAL LAYOUT DRAWN BY			
ABDULLAH-AL-FOYSAL			
CONSULTANT			
Prodhan Design & Construction			
Address: 94/3, LEVEL-2, TALLABAGH, INDIRA ROAD, DHAKA-1215			
SITE OFFICE: M/S. TMRR ENTERPRISE, KALIBARI BAZAR, PALASHBARI MUNICIPALITY,GAIBANDHA.			
1	22/07/26	1ST,3RD,4TH FLOOR	
NO.	DATE	REVISION	BY
CAD BY:		SHEET NO:	
		16	
DATE:		SCALE:	
11/07/2026		5":1'	

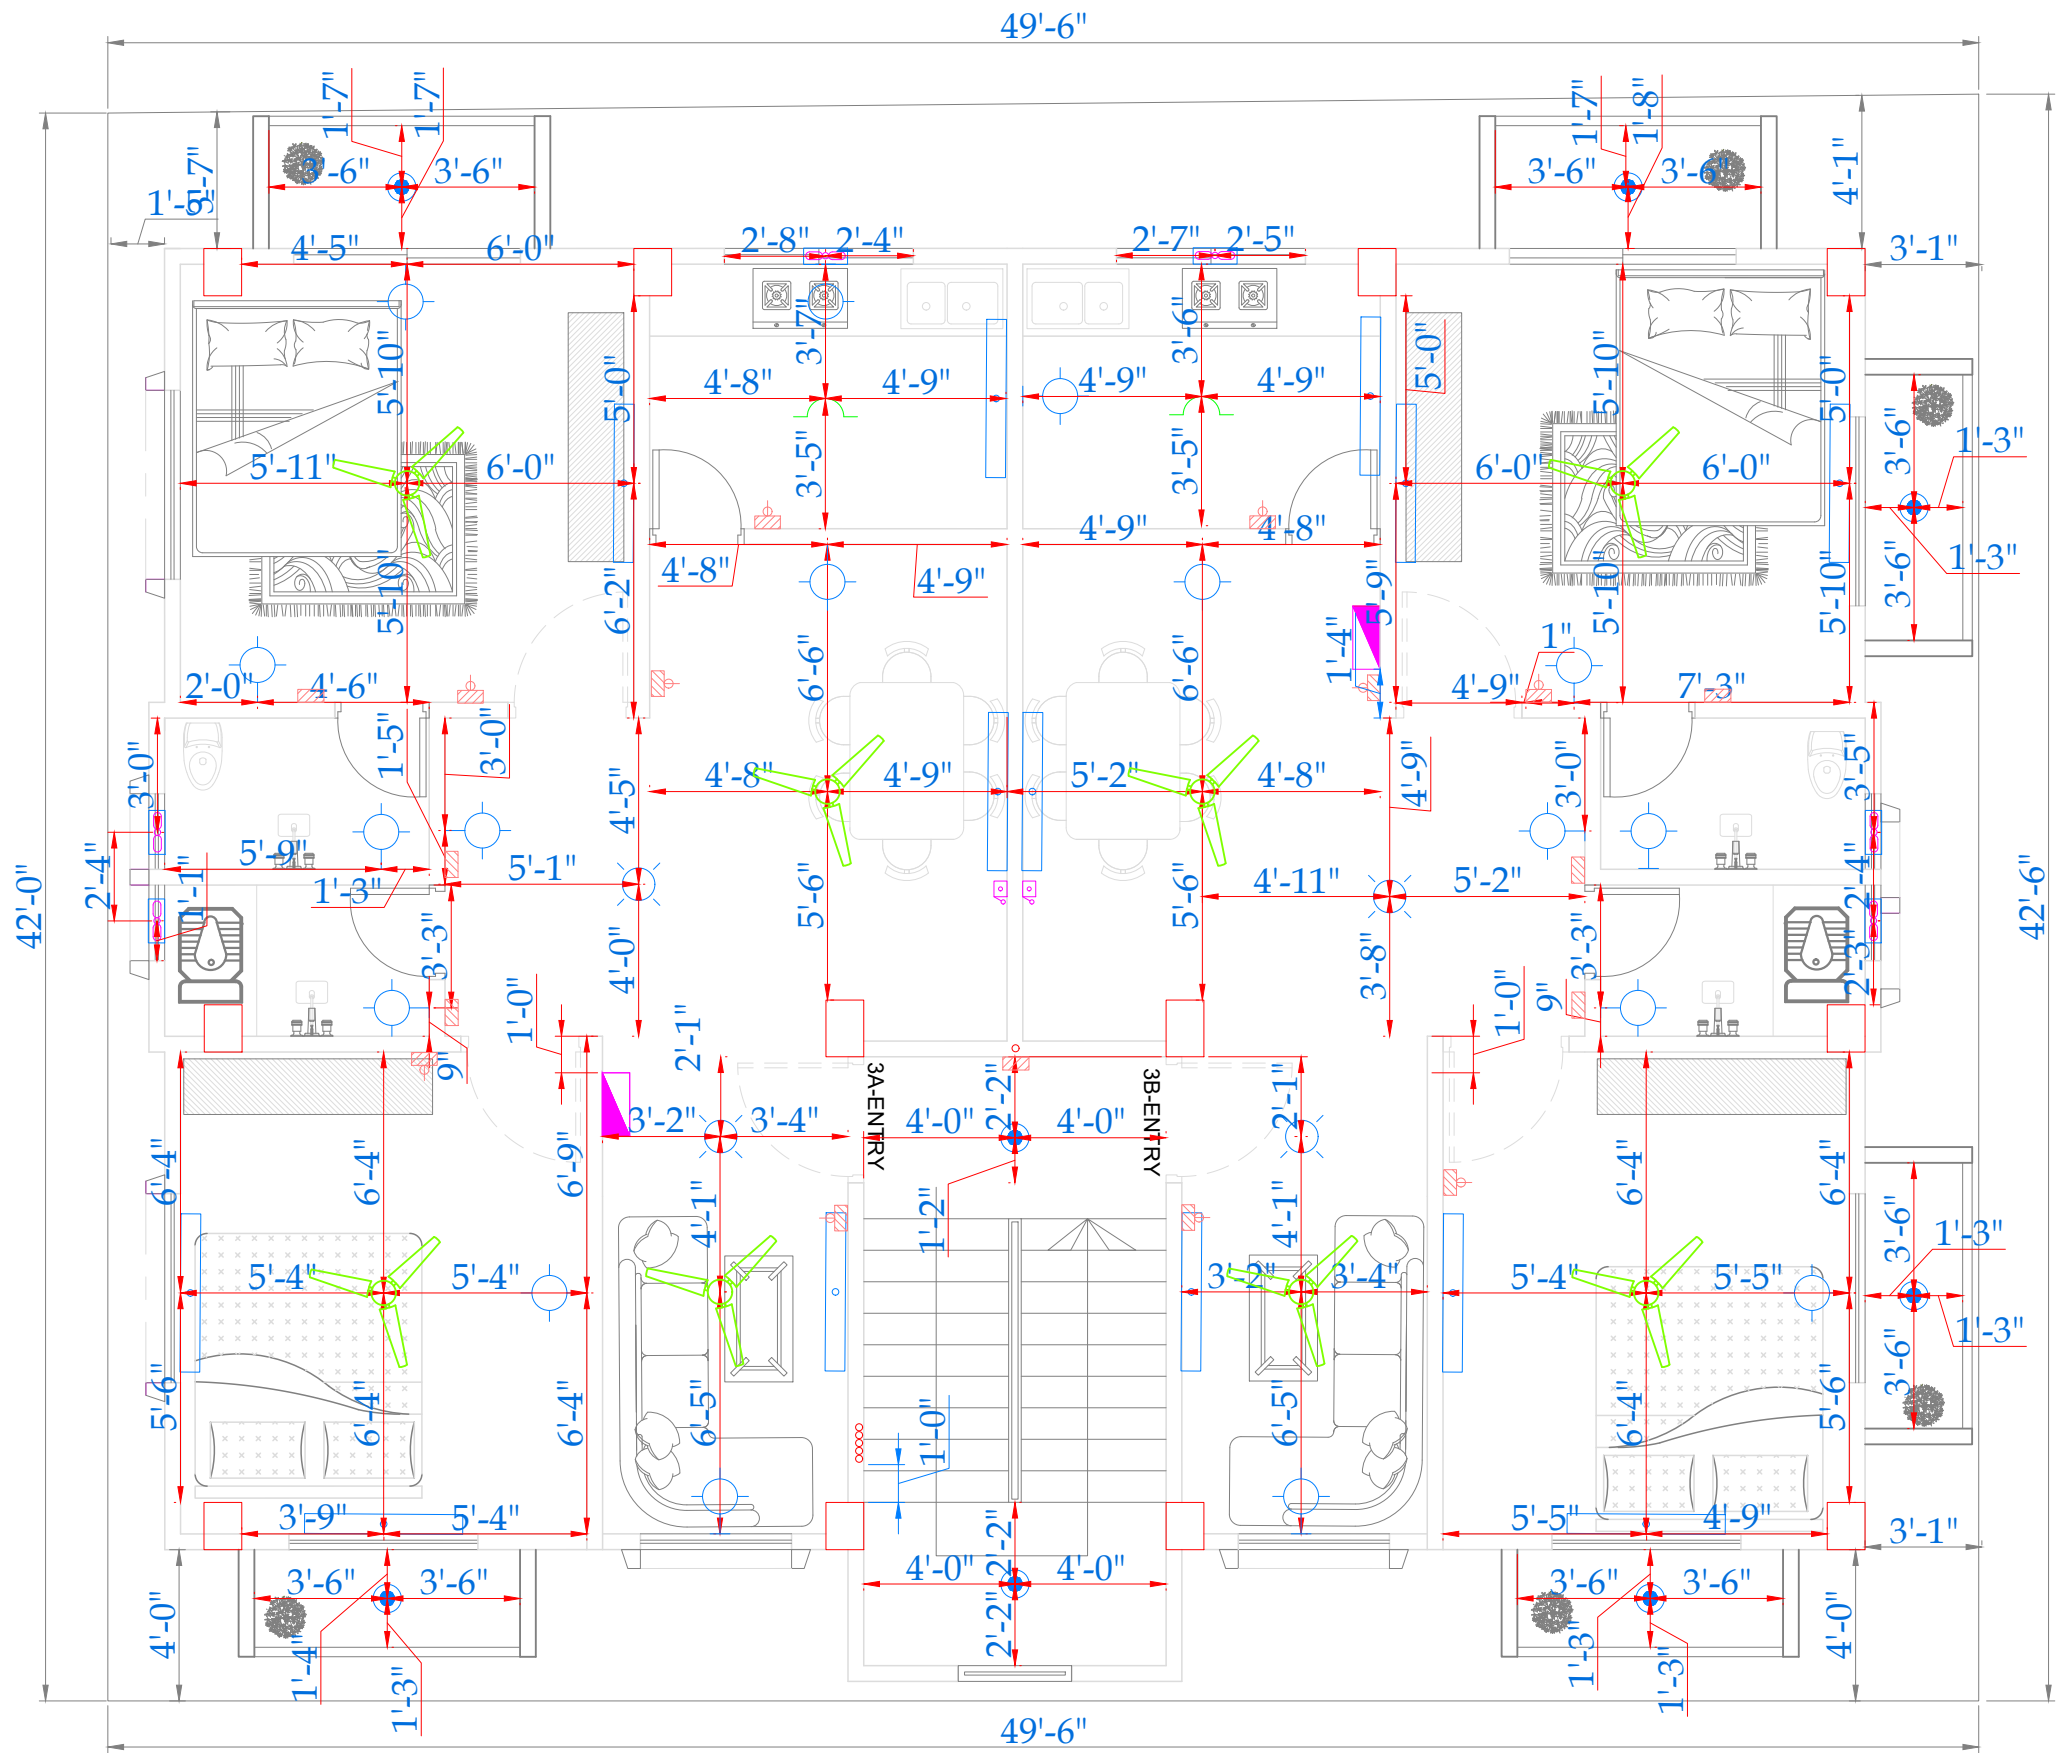

2ND & 3RD FLOOR FIXTURE DIMENSION PLAN
SCALE 5":1'

PROJECT NAME			
G+4 STORIED RESIDENTIAL BUILDING AT HARINMARI, PALASHBARI MUNICIPALITY, GAIBANDHA			
CLIENT NAME			
MR. MD. REJAUL KARIM			
DRAWING TITLE			
Electrical Layout Plan.			
ENGINEER			
MD. RIYADUL ISLAM PRODHAN			
B. Sc in Civil Engg. NSU			
M.Sc in Civil Engg. AUST			
M.Sc in Soil Science. DU			
M.Sc in ESM. JU			
IEB. REG. NO: M-45122			
MAHBUB KARIM			
B. Sc in Civil Engg. NSU			
M. Sc in Civil Engg. BUET			
M.Sc in Civil Engg. CDU (AUSTRALIA)			
IEB. REG. NO: M-45123			
ABDULLAH-AL-FOYSAL			
B. Sc in EEE; EASTERN UNIVERSITY			
Diploma in Electrical; ICST			
IEB. REG. NO: PENDING			
APPROVED BY			
ELECTRICAL LAYOUT DRAWN BY			
ABDULLAH-AL-FOYSAL			
CONSULTANT			
Prodhan Design & Construction			
Address: 94/3, LEVEL-2, TALLABAGH, INDIRA ROAD, DHAKA-1215			
SITE OFFICE: M/S. TMRR ENTERPRISE, KALIBARI BAZAR, PALASHBARI MUNICIPALITY,GAIBANDHA.			
1	22/07/26	1ST,3RD,4TH FLOOR	
NO.	DATE	REVISION	BY
CAD BY:		SHEET NO:	
		17	
DATE:		SCALE:	
11/07/2026		5":1'	

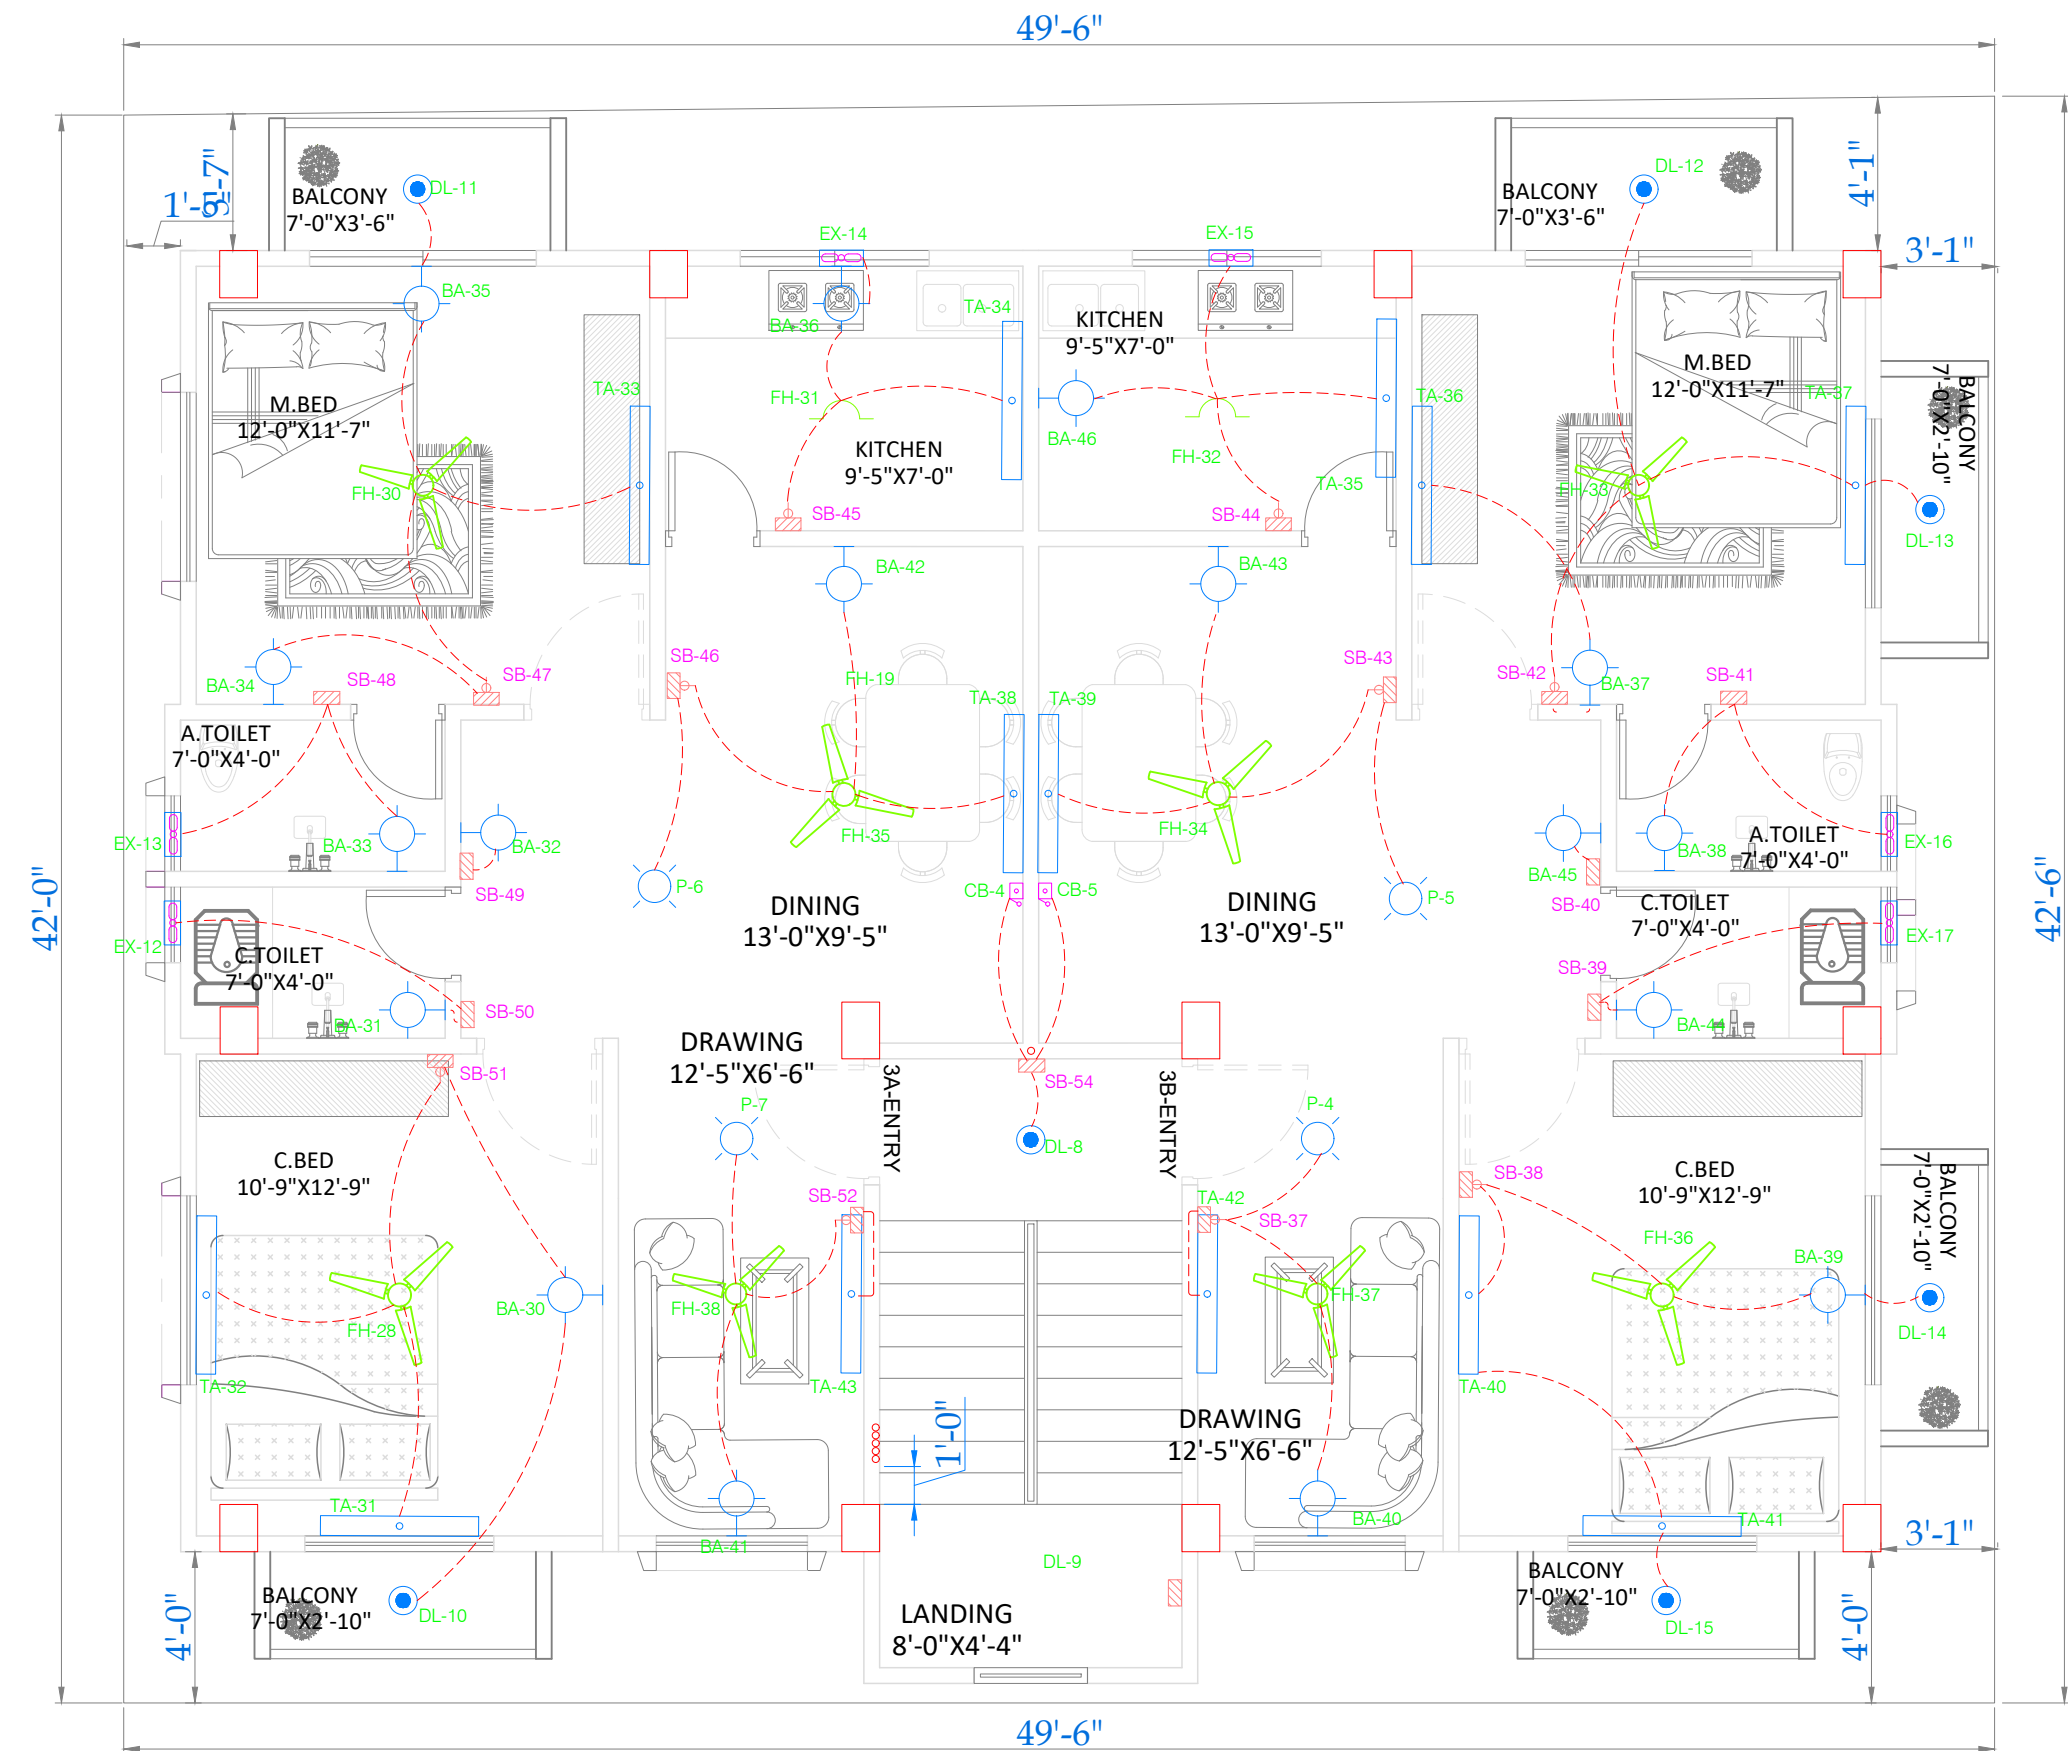

2ND & 3RD FLOOR LIGHTING FIXTURE COUNDUET PLAN
SCALE 5":1'

PROJECT NAME
G+4 STORIED RESIDENTIAL BUILDING AT
HARINMARI, PALASHBARI MUNICIPALITY,
GAIBANDHA

CLIENT NAME
MR. MD. REJAUL KARIM

DRAWING TITLE
Electrical Layout Plan.

ENGINEER
**MD. RIYADUL ISLAM
PRODHAN**

B. Sc in Civil Engg. NSU
M.Sc in Civil Engg. AUST
M.Sc in Soil Science. DU
M.Sc in ESM. JU
IEB. REG. NO: M-45122

MAHBUB KARIM

B. Sc in Civil Engg. NSU
M. Sc in Civil Engg. BUET
M.Sc in Civil Engg. CDU (AUSTRALIA)
IEB. REG. NO: M-45123

ABDULLAH-AL-FOYSAL

B. Sc in EEE; EASTERN UNIVERSITY
Diploma in Electrical; ICST
IEB. REG. NO: PENDING

APPROVED BY

ELECTRICAL LAYOUT DRAWN BY

ABDULLAH-AL-FOYSAL

CONSULTANT

Prodhan Design & Construction

Address: 94/3, LEVEL-2, TALLABAGH,
INDIRA ROAD, DHAKA-1215
SITE OFFICE: M/S. TMRR ENTERPRISE,
KALIBARI BAZAR, PALASHBARI
MUNICIPALITY,GAIBANDHA.

1	22/07/26	1ST,3RD,4TH FLOOR	
---	----------	-------------------	--

NO.	DATE	REVISION	BY
-----	------	----------	----


CAD BY:	SHEET NO:
---------	-----------

18

DATE:	SCALE:
-------	--------


11/07/2026

5":1'

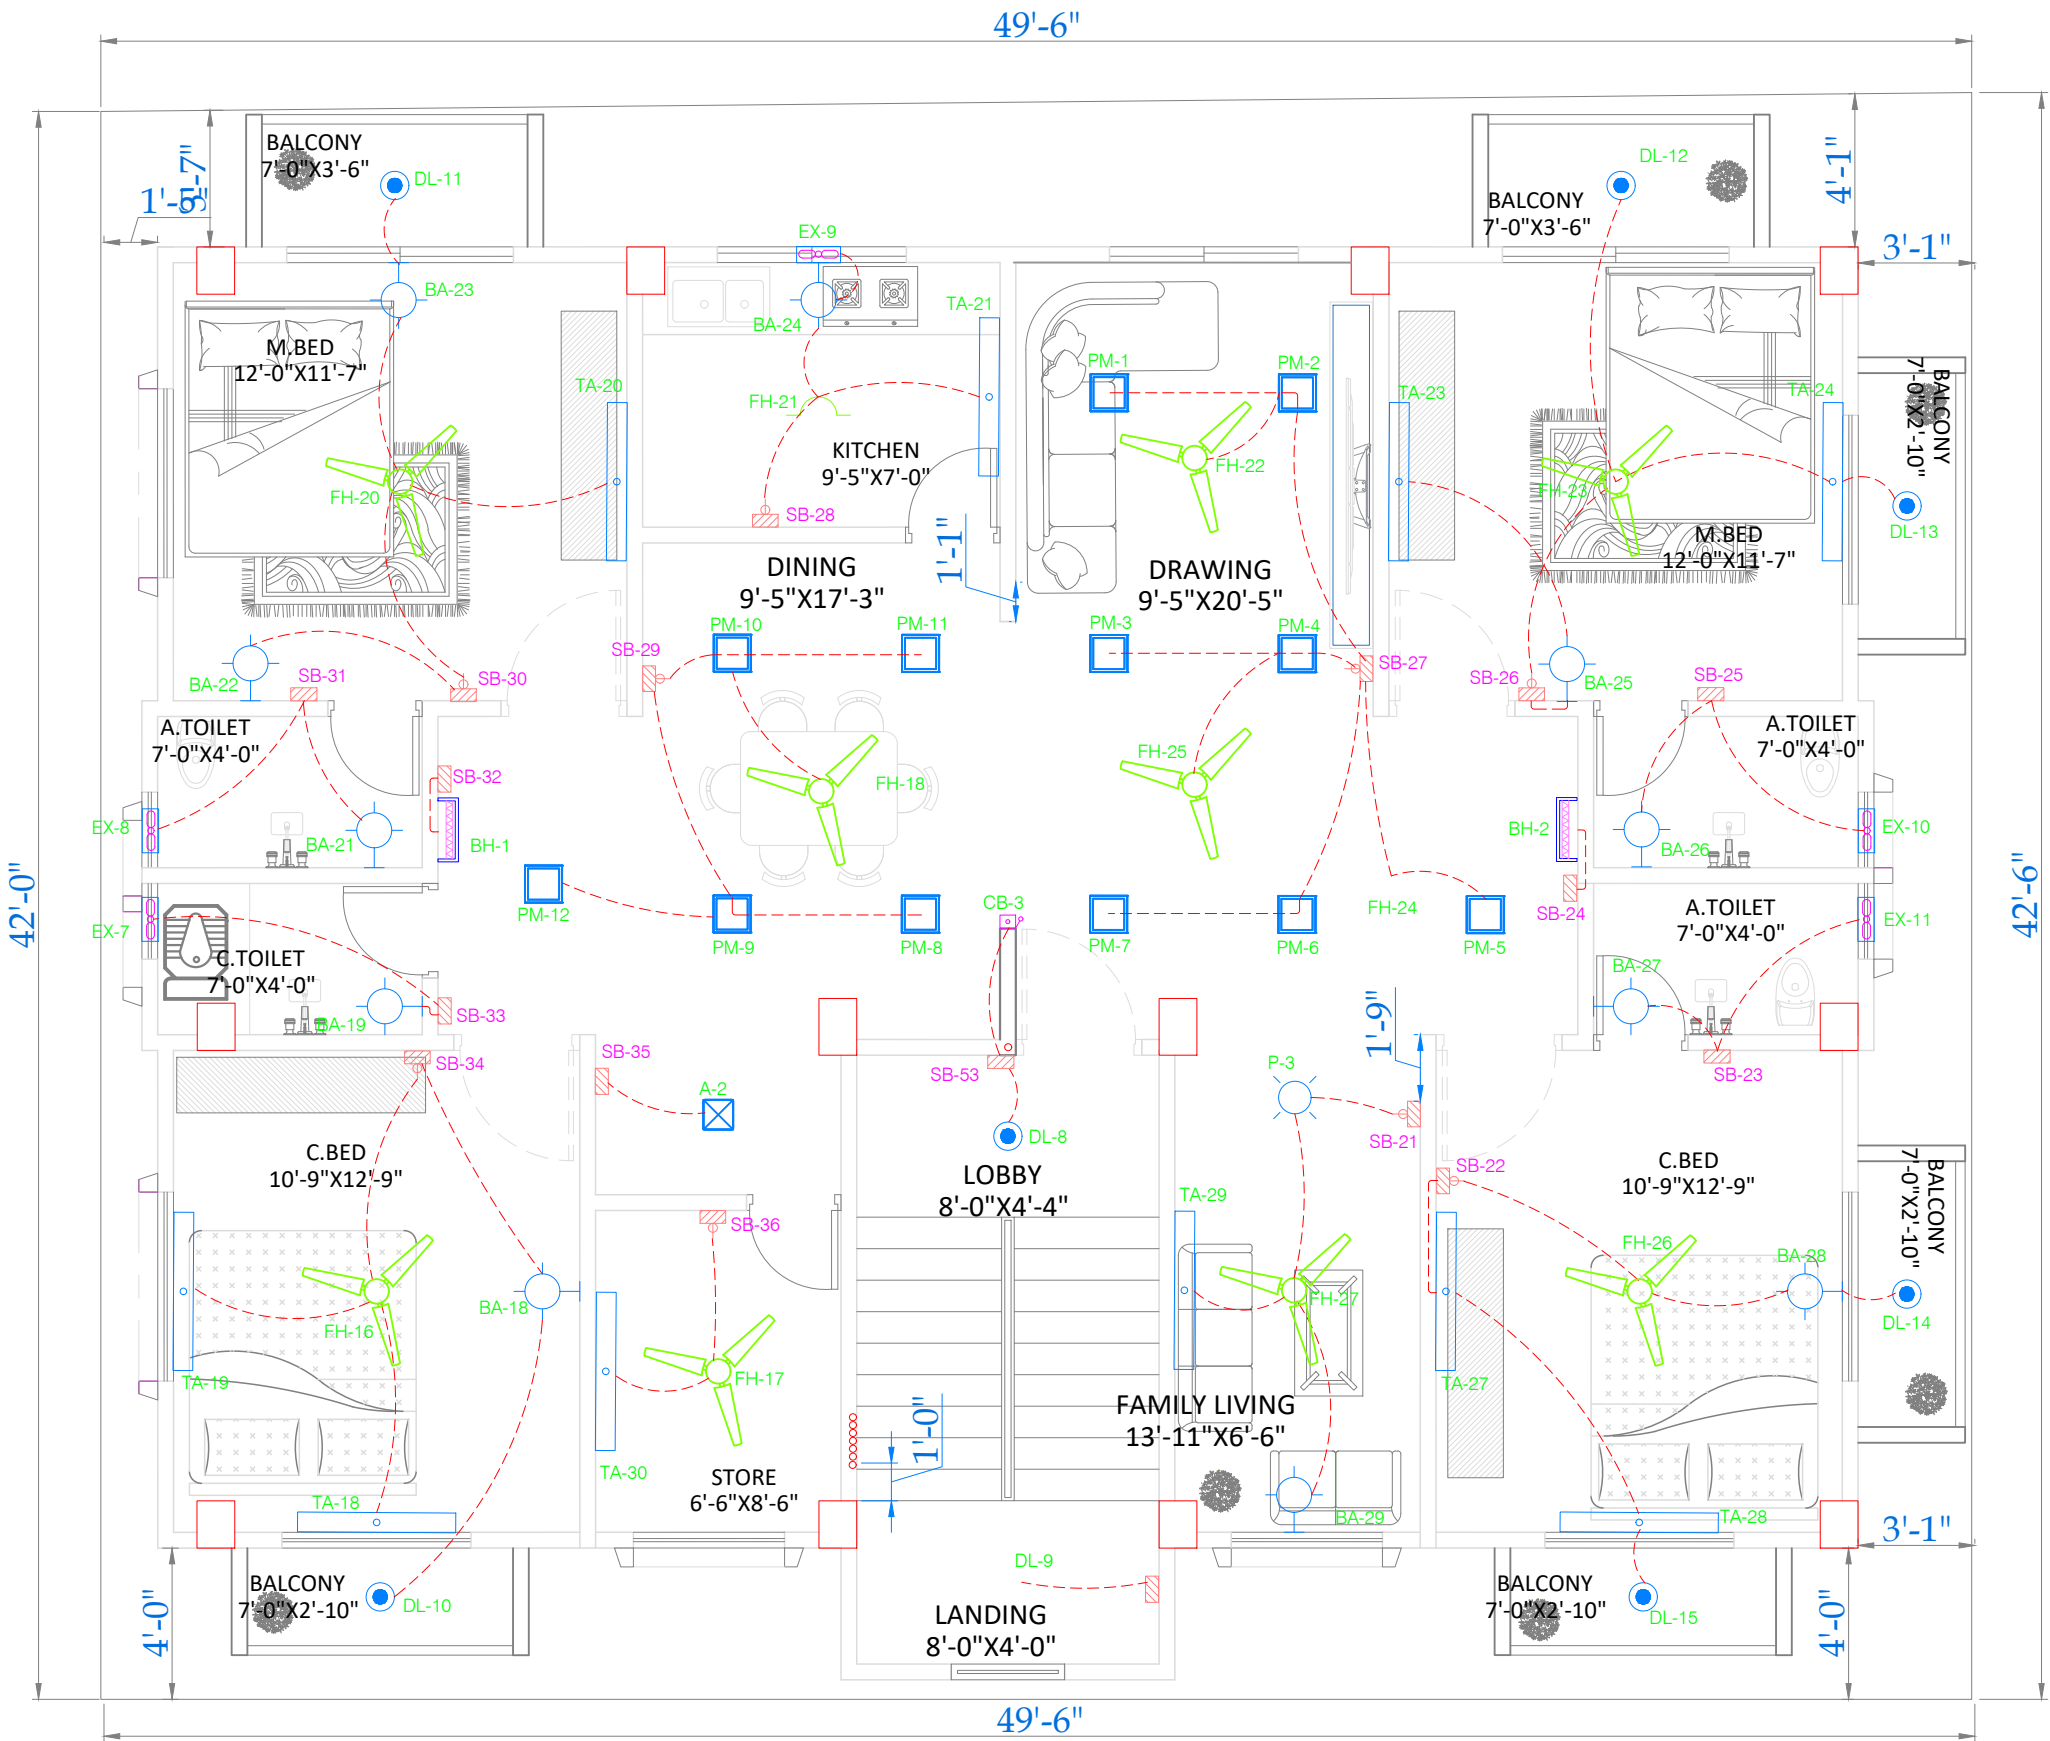

1ST FLOOR (1 UNIT) LIGHTING FIXTURE COUNDUET PLAN
SCALE 5":1'

PROJECT NAME			
G+4 STORIED RESIDENTIAL BUILDING AT HARINMARI, PALASHBARI MUNICIPALITY, GAIBANDHA			
CLIENT NAME			
MR. MD. REJAUL KARIM			
DRAWING TITLE			
Electrical Layout Plan.			
ENGINEER			
MD. RIYADUL ISLAM PRODHAN			
B. Sc in Civil Engg. NSU			
M.Sc in Civil Engg. AUST			
M.Sc in Soil Science. DU			
M.Sc in ESM. JU			
IEB. REG. NO: M-45122			
MAHBUB KARIM			
B. Sc in Civil Engg. NSU			
M. Sc in Civil Engg. BUET			
M.Sc in Civil Engg. CDU (AUSTRALIA)			
IEB. REG. NO: M-45123			
ABDULLAH-AL-FOYSAL			
B. Sc in EEE; EASTERN UNIVERSITY			
Diploma in Electrical; ICST			
IEB. REG. NO: PENDING			
APPROVED BY			
ELECTRICAL LAYOUT DRAWN BY			
ABDULLAH-AL-FOYSAL			
CONSULTANT			
Prodhan Design & Construction			
Address: 94/3, LEVEL-2, TALLABAGH, INDIRA ROAD, DHAKA-1215			
SITE OFFICE: M/S. TMRR ENTERPRISE, KALIBARI BAZAR, PALASHBARI MUNICIPALITY,GAIBANDHA.			
1	22/07/26	1ST,3RD,4TH FLOOR	
NO.	DATE	REVISION	BY
CAD BY:		SHEET NO:	
		19	
DATE:		SCALE:	
11/07/2026		5":1'	

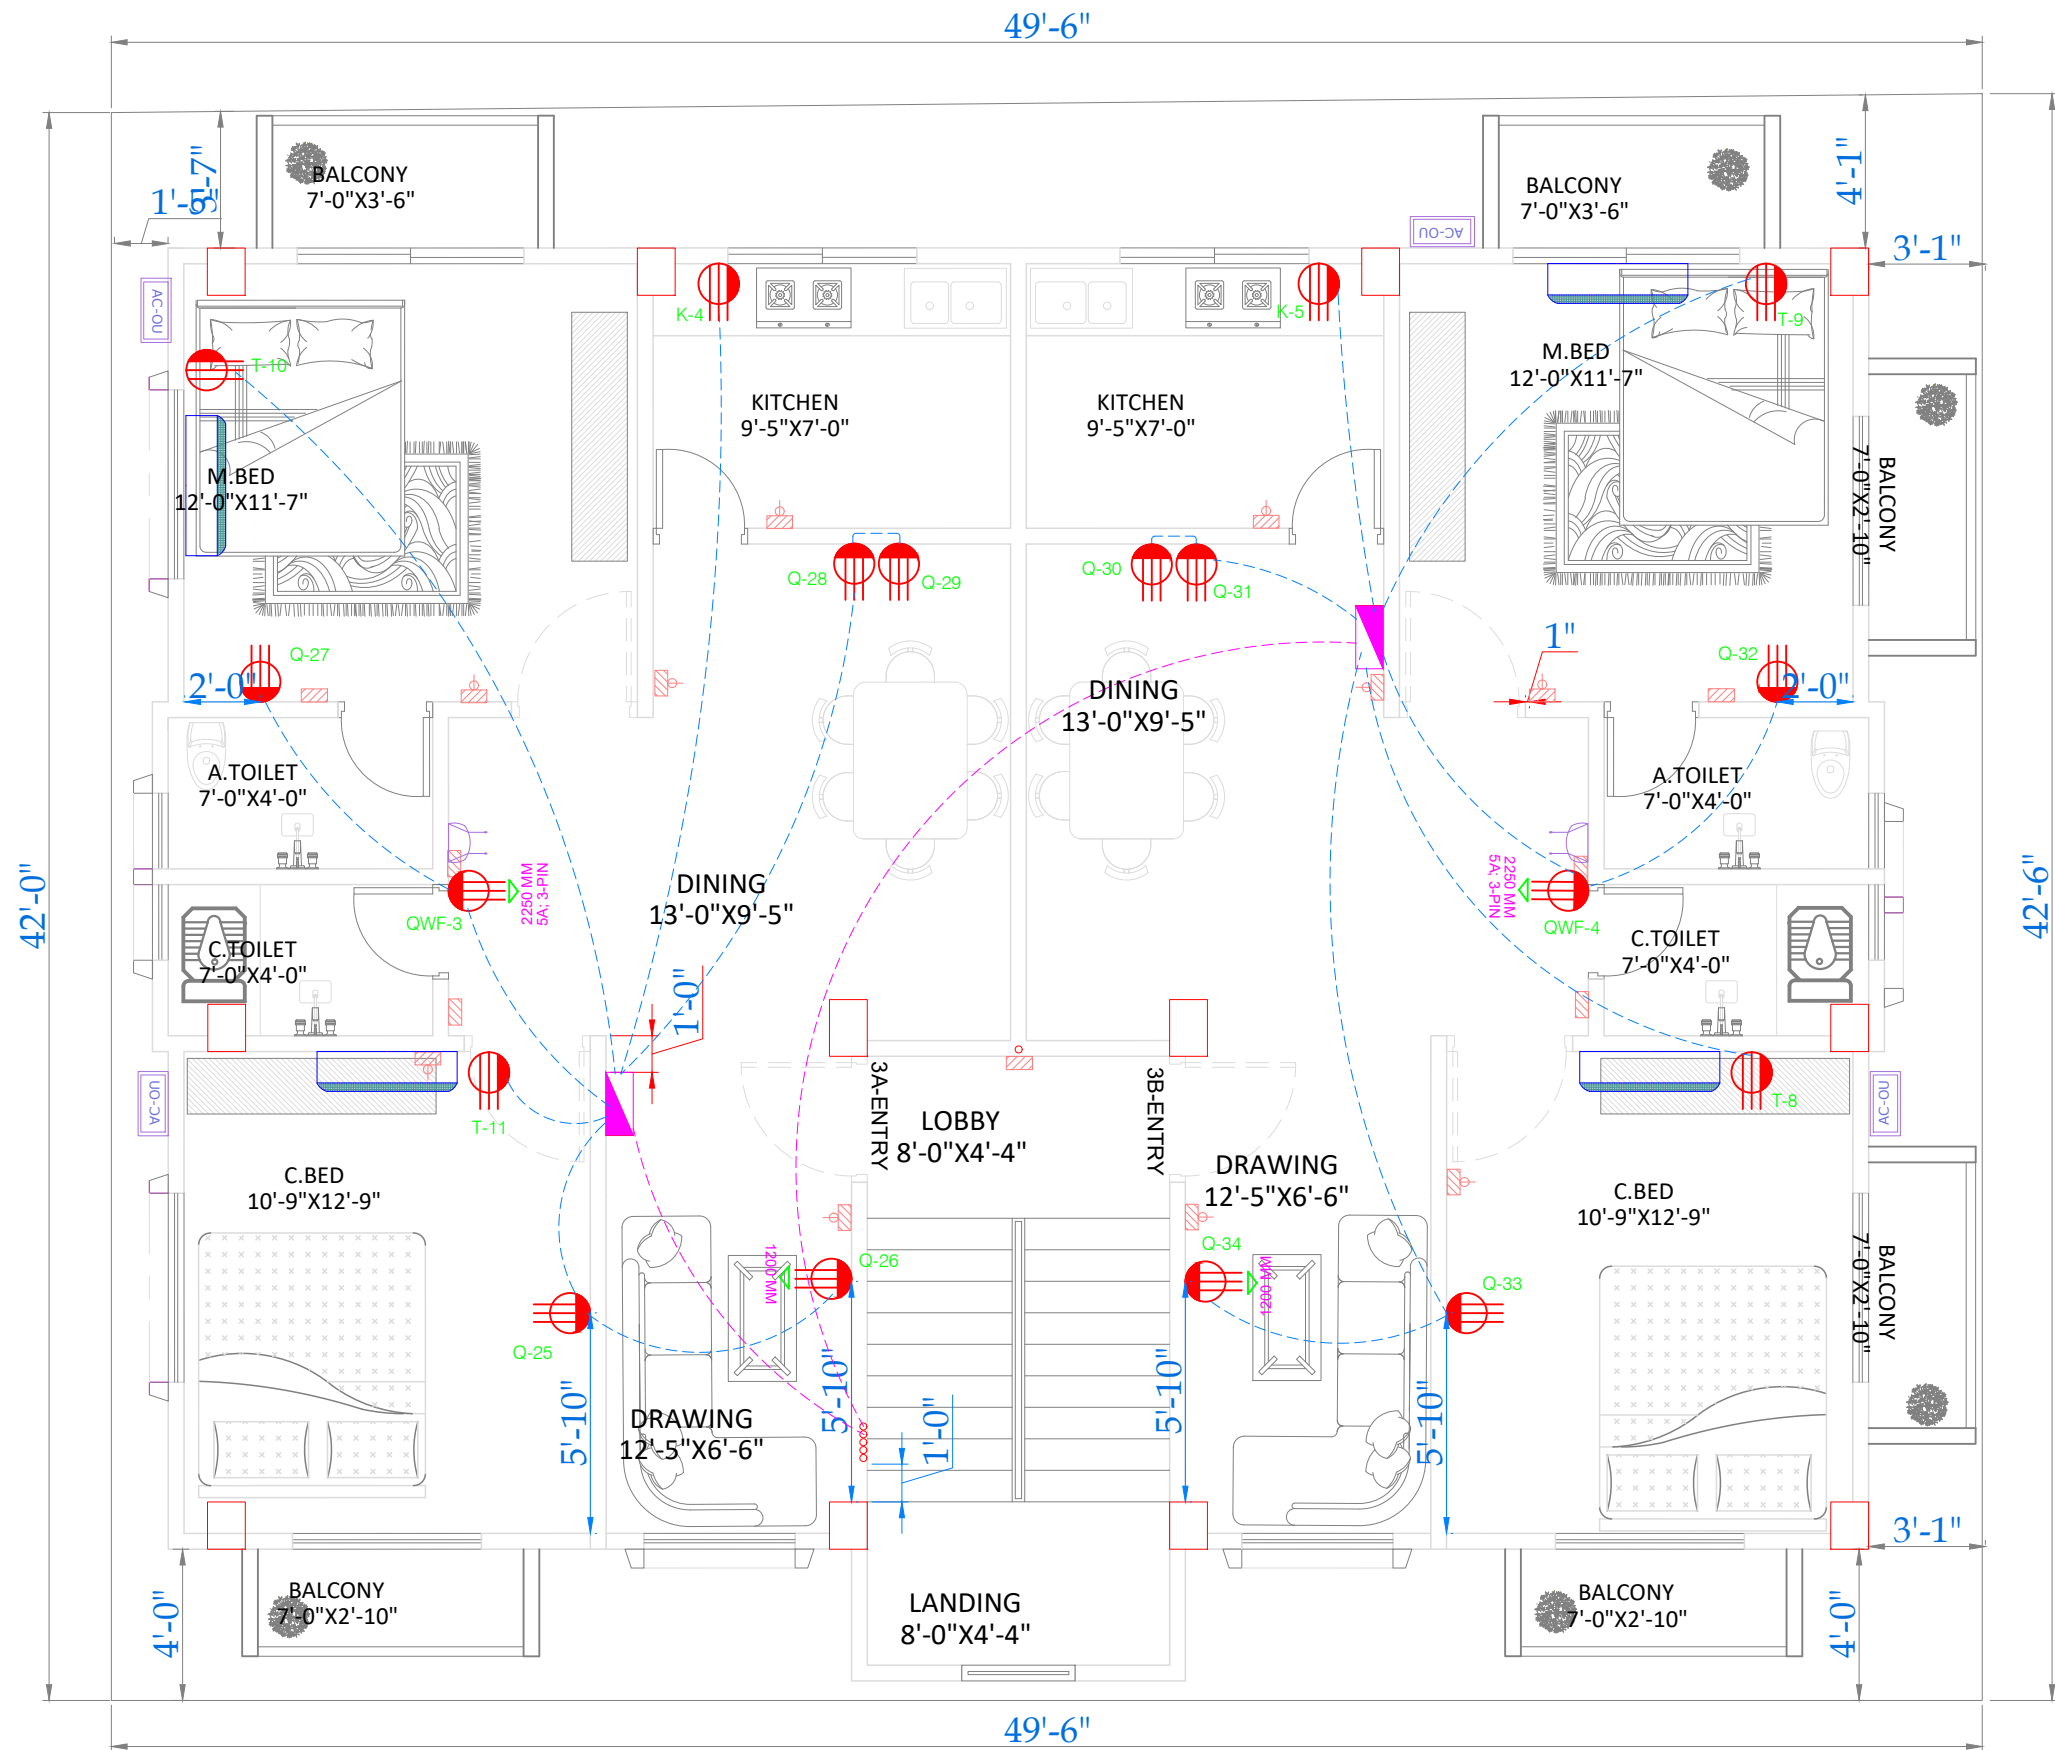

2ND & 3RD FLOOR POWER CIRCUIT PLAN
SCALE 5":1'

PROJECT NAME
G+4 STORIED RESIDENTIAL BUILDING AT
HARINMARI, PALASHBARI MUNICIPALITY,
GAIBANDHA

CLIENT NAME
MR. MD. REJAUL KARIM

DRAWING TITLE
Electrical Layout Plan.

ENGINEER
**MD. RIYADUL ISLAM
PRODHAN**
B. Sc in Civil Engg. NSU
M.Sc in Civil Engg. AUST
M.Sc in Soil Science. DU
M.Sc in ESM. JU
IEB. REG. NO: M-45122

MAHBUB KARIM
B. Sc in Civil Engg. NSU
M. Sc in Civil Engg. BUET
M.Sc in Civil Engg. CDU (AUSTRALIA)
IEB. REG. NO: M-45123

ABDULLAH-AL-FOYSAL
B. Sc in EEE; EASTERN UNIVERSITY
Diploma in Electrical; ICST
IEB. REG. NO: PENDING

APPROVED BY

ELECTRICAL LAYOUT DRAWN BY

ABDULLAH-AL-FOYSAL

CONSULTANT

Prodhan Design & Construction
Address: 94/3, LEVEL-2, TALLABAGH,
INDIRA ROAD, DHAKA-1215
SITE OFFICE: M/S. TMRR ENTERPRISE,
KALIBARI BAZAR, PALASHBARI
MUNICIPALITY,GAIBANDHA.

1	22/07/26	1ST,3RD,4TH FLOOR	
---	----------	-------------------	--

NO.	DATE	REVISION	BY
CAD BY:		SHEET NO: 20	
DATE: 11/07/2026		SCALE: 5":1'	