

ELECTRICAL DRAWINGS LIST OF G+5- STORIED RESIDENTIAL BUILDING.

S. NO.	DRAWINGS NO.	DRAWINGS DESCRIPTION	PAGE SIZE	
01	NCC-MFA-ED-02	MAIN DRAWING WITH FULL AREA DIMENSION	A3	
02	NCC-MFA-ED-03	LIGHT, FAN OUTLET DIMENSION LAYOUT OF GROUND; 1ST; 3RD FLOOR	A3	
03	NCC-MFA-ED-04		A3	
04	NCC-MFA-ED-05	LIGHT, FAN OUTLET AND CONDUIT LAYOUT OF GROUND; 1ST; 3RD FLOOR	A3	
05	NCC-MFA-ED-06	LIGHT, FAN OUTLET AND ELECTRICAL CIRCUIT LAYOUT OF GROUND; 1ST; 3RD FLOOR	A3	
06	NCC-MFA-ED-07	POWER OUTLET & CONDUIT LAYOUT OF GROUND FLOOR	A3	
07	NCC-MFA-ED-08	INTERNET & CCTV OUTLET AND CONDUIT LAYOUT OF GROUND FLOOR	A3	
08	NCC-MFA-ED-09	POWER OUTLET & CONDUIT LAYOUT OF 1ST FLOOR	A3	
09	NCC-MFA-ED-10	INTERNET & CCTV OUTLET AND CONDUIT LAYOUT OF 1ST FLOOR	A3	
10	NCC-MFA-ED-11	LIGHT, FAN OUTLET DIMENSION LAYOUT OF 2ND FLOOR	A3	
11	NCC-MFA-ED-12	LIGHT, FAN OUTLET PLAN LAYOUT OF 2ND FLOOR	A3	
12	NCC-MFA-ED-13	LIGHT, FAN OUTLET AND CONDUIT LAYOUT OF 2ND FLOOR	A3	
13	NCC-MFA-ED-14	LIGHT, FAN OUTLET AND ELECTRICAL CIRCUIT LAYOUT OF 2ND FLOOR	A3	
14	NCC-MFA-ED-15	POWER OUTLET & CONDUIT LAYOUT OF 2ND FLOOR	A3	
15	NCC-MFA-ED-16	CCTV OUTLET AND CONDUIT LAYOUT OF 2ND FLOOR	A3	
16	NCC-MFA-ED-17	INTERNET OUTLET AND CONDUIT LAYOUT OF 2ND FLOOR	A3	
17	NCC-MFA-ED-18	POWER OUTLET & CONDUIT LAYOUT OF 3RD FLOOR	A3	
18	NCC-MFA-ED-19	INTERNET & CCTV OUTLET AND CONDUIT LAYOUT OF 3RD FLOOR	A3	
19	NCC-MFA-ED-20	LIGHT, FAN OUTLET DIMENSION LAYOUT OF ROOF FLOOR	A3	
20	NCC-MFA-ED-21	LIGHT, FAN OUTLET PLAN LAYOUT OF ROOF FLOOR	A3	
21	NCC-MFA-ED-22	LIGHT, FAN OUTLET AND CONDUIT LAYOUT OF ROOF FLOOR	A3	
22	NCC-MFA-ED-23	LIGHT, FAN OUTLET AND ELECTRICAL CIRCUIT LAYOUT OF ROOF FLOOR	A3	
23	NCC-MFA-ED-24	POWER OUTLET & CONDUIT LAYOUT OF ROOF FLOOR	A3	
24	NCC-MFA-ED-25	CCTV OUTLET AND CONDUIT LAYOUT OF ROOF FLOOR	A3	
25	NCC-MFA-ED-26	SINGLE LINE DIAGRAM OF MDB GROUND FLOOR	A3	
26	NCC-MFA-ED-27	SINGLE LINE DIAGRAM OF SDB-1 & SDB-2 AT GROUND FLOOR	A3	
27	NCC-MFA-ED-28	SINGLE LINE DIAGRAM OF SDB-3 & SDB-4 AT 1ST FLOOR	A3	
28	NCC-MFA-ED-29	SINGLE LINE DIAGRAM OF SDB-5 FLOOR AT 2ND FLOOR	A3	
29	NCC-MFA-ED-30	SINGLE LINE DIAGRAM OF SDB-6 & SDB-7 AT 3RD FLOOR	A3	
30	NCC-MFA-ED-31	SINGLE LINE DIAGRAM OF SDB-8 & SDB-9 AT ROOF FLOOR		

ELECTRICAL LEGEND

	DB	DISTRIBUTION BOARD
	MDB	MAIN DISTRIBUTION BOARD
	SB-2P	SWITCH BOARD AT 1350 mm
	SB	SWITCH BOARD AT 1350 mm
	P	05A, 250V, SWITCHED SOCKET (TYPE-P)
	Q	13A, 250V, UNIVERSAL 3-PIN SWITCHED SOCKET
	T	15A, 250V, UNIVERSAL 3-PIN SWITCHED SOCKET
	BA	BRACKET LIGHT FITTINGS WITH 1x12W LED LAMP
	BH	BATHROOM MIRROR LED LIGHT FITTING
	SP	SPOT LIGHT FITTING WITH 1x6W LED LAMP
	TA	SURFACE TYPE LIGHT FITTING 1x18W LED T5 LAMP
	FH	FAN HOOK
	EX.FAN	AC CAPACITOR TYPE WALL MOUNTED EXHAUST FAN
	F	56 INCH SWEEP CEILING FAN
	CB	CALLING BELL
	TDB	TELEPHONE DISTRIBUTION BOARD
	TV	TELEVISION OUTLET
	DM CCTV	DOME TYPE CCTV CAMERA OUTLET
	B CCTV	BULLET TYPE CCTV CAMERA OUTLET
	IN-R	INTERNET ROUTER OUTLET
	JUNCTION BOX	JUNCTION BOX
	CONCEALED CABLE ROUTE	
	CABLE ROUTE THROUGH FLOOR	

NOTES:

1. UNLESS OTHERWISE SPECIFIED, THE CONDUIT SIZE SHALL BE 3/4" INNER DIA.

LIST OF FIXTURE	SYMBOL	HEIGHT FROM FFL
SWITCH, FAN REGULATOR	SB	1350mm
WALL BRACKET & TUBE LIGHT	BA, TA	2400mm
CEILING FAN	F	2600mm
05A SOCKET OUTLET	P	1350mm
13A SOCKET OUTLET	Q	250mm

Rev. no.	Date:	Description
PROJECT:		
Mostofa Bhaban		
CLIENT:		
CONSULTANT:		
JOB TITLE :		
DRAWING TITLE : Mostofa Bhaban, Electrical DRAWING		
OWNER'S SIGNATURE :		
TEAM LEADER :		
ELECTRICAL ENGINEER : ABDULLAH-AL-FOYSAL		
CHECKED BY:	CAD BY:	SHEET NO: 04
DATE: NOV-2025	SCALE: 1:50	

EXECUTIVE AGENCY :	NAME OF WORK :				APPROVED BY	
			SUPERINTENDING ENGINEER EED	PROJECT DIRECTOR OF ESTABLISHMENT OF ISLAMIC ARABIC UNIVERSITY	CHIEF ENGINEER EED	VICE CHANCELLOR ISLAMIC ARABIC UNIVERSITY



Rev. no.	Date:	Description
PROJECT: Mostofa Bhaban		
CLIENT:		
CONSULTANT:		
JOB TITLE :		
DRAWING TITLE : Mostofa Bhaban, Electrical DRAWING		
OWNER'S SIGNATURE :		
TEAM LEADER :		
ELECTRICAL ENGINEER : ABDULLAH-AL-FOYSAL		
CHECKED BY:	CAD BY:	SHEET NO: 03
DATE: NOV-2025	SCALE: 1:50	

EXECUTIVE AGENCY :	NAME OF WORK :				APPROVED BY
			SUPERINTENDING ENGINEER EED	PROJECT DIRECTOR OF ESTABLISHMENT OF ISLAMIC ARABIC UNIVERSITY	CHIEF ENGINEER EED
					VICE CHANCELLOR ISLAMIC ARABIC UNIVERSITY



LIST OF FIXTURE	SYMBOL	HEIGHT FROM FFL
SWITCH, FAN REGULATOR	SB	1350mm
WALL BRACKET & TUBE LIGHT	BA, TA	2400mm
CEILING FAN	F	2600mm
05A SOCKET OUTLET	P	1350mm
13A SOCKET OUTLET	Q	250mm

TEAM LEADER :		
ELECTRICAL ENGINEER :		
ABDULLAH-AL-FOYSAL		
CHECKED BY :	CAD BY :	SHEET NO: 04
DATE: NOV-2025	SCALE: 1:50	

EXECUTIVE AGENCY :	NAME OF WORK :				APPROVED BY	
				SUPERINTENDING ENGINEER EED	PROJECT DIRECTOR OF ESTABLISHMENT OF ISLAMIC ARABIC UNIVERSITY	CHIEF ENGINEER EED
						VICE CHANCELLOR ISLAMIC ARABIC UNIVERSITY



SCALE: 1:50
AREA: 950 SQM

1. UNLESS OTHERWISE SPECIFIED, THE CONDUIT SIZE SHALL BE 3/4" INNER DIA.

CHECKED BY:	CAD BY:	SHEET NO: 05
DATE: NOV-2025	SCALE: 1:50	

EXECUTIVE AGENCY :	NAME OF WORK :				APPROVED BY
			SUPERINTENDING ENGINEER EED	PROJECT DIRECTOR OF ESTABLISHMENT OF ISLAMIC ARABIC UNIVERSITY	CHIEF ENGINEER EED
					VICE CHANCELLOR ISLAMIC ARABIC UNIVERSITY



LIST OF FIXTURE	SYMBOL	HEIGHT FROM FFL
SWITCH, FAN REGULATOR	SB	1350mm
WALL BRACKET & TUBE LIGHT	BA, TA	2400mm
CEILING FAN	F	2600mm
05A SOCKET OUTLET	P	1350mm
13A SOCKET OUTLET	Q	250mm

Rev. no.	Date:	Description
PROJECT: Mostofa Bhaban		
CLIENT:		
CONSULTANT:		
JOB TITLE :		
DRAWING TITLE : Mostofa Bhaban, Electrical DRAWING		
OWNER'S SIGNATURE :		
TEAM LEADER :		
ELECTRICAL ENGINEER : ABDULLAH-AL-FOYSAL		
CHECKED BY:	CAD BY:	SHEET NO: 06
DATE: NOV-2025	SCALE: 1:50	

EXECUTIVE AGENCY :	NAME OF WORK :				APPROVED BY	
			SUPERINTENDING ENGINEER EED	PROJECT DIRECTOR OF ESTABLISHMENT OF ISLAMIC ARABIC UNIVERSITY	CHIEF ENGINEER EED	VICE CHANCELLOR ISLAMIC ARABIC UNIVERSITY



LIST OF FIXTURE	SYMBOL	HEIGHT FROM FFL
SWITCH, FAN REGULATOR	SB	1350mm
WALL BRACKET & TUBE LIGHT	BA, TA	2400mm
CEILING FAN	F	2600mm
05A SOCKET OUTLET	P	1350mm
13A SOCKET OUTLET	Q	250mm

Rev. no.	Date:	Description
PROJECT: Mostofa Bhaban		
CLIENT:		
CONSULTANT:		
JOB TITLE :		
DRAWING TITLE : Mostofa Bhaban, Electrical DRAWING		
OWNER'S SIGNATURE :		
TEAM LEADER :		
ELECTRICAL ENGINEER : ABDULLAH-AL-FOYSAL		
CHECKED BY:	CAD BY:	SHEET NO: 07
DATE: NOV-2025	SCALE: 1:50	

EXECUTIVE AGENCY :	NAME OF WORK :				APPROVED BY
			SUPERINTENDING ENGINEER EED	PROJECT DIRECTOR OF ESTABLISHMENT OF ISLAMIC ARABIC UNIVERSITY	CHIEF ENGINEER EED
					VICE CHANCELLOR ISLAMIC ARABIC UNIVERSITY



LIST OF FIXTURE	SYMBOL	HEIGHT FROM FFL
SWITCH, FAN REGULATOR	SB	1350mm
WALL BRACKET & TUBE LIGHT	BA, TA	2400mm
CEILING FAN	F	2600mm
05A SOCKET OUTLET	P	1350mm
13A SOCKET OUTLET	Q	250mm

Rev. no.	Date:	Description
PROJECT:		
Mostofa Bhaban		
CLIENT:		
CONSULTANT:		
JOB TITLE :		
DRAWING TITLE : Mostofa Bhaban, Electrical DRAWING		
OWNER'S SIGNATURE :		
TEAM LEADER :		
ELECTRICAL ENGINEER :		
ABDULLAH-AL-FOYSAL		
CHECKED BY:	CAD BY:	SHEET NO: 08
DATE: NOV-2025	SCALE: 1:50	

EXECUTIVE AGENCY :	NAME OF WORK :				APPROVED BY	
			SUPERINTENDING ENGINEER EED	PROJECT DIRECTOR OF ESTABLISHMENT OF ISLAMIC ARABIC UNIVERSITY	CHIEF ENGINEER EED	VICE CHANCELLOR ISLAMIC ARABIC UNIVERSITY



NOTES:

1. UNLESS OTHERWISE SPECIFIED, THE CONDUIT SIZE SHALL BE 3/4" INNER DIA.

Rev. no.	Date:	Description
PROJECT: Mostofa Bhaban; MIAZI ROAD; 13 NO WARD; CIRCUIT HOUSE; MOHIPAL FENI		
CLIENT: MD. OMAR FARUK		
CONSULTANT:		
JOB TITLE :		
DRAWING TITLE : Mostofa Bhaban, Electrical DRAWING		
OWNER'S SIGNATURE :		
TEAM LEADER :		
ELECTRICAL ENGINEER : ABDULLAH-AL-FOYSAL		
CHECKED BY: REZAUL KARIM	CAD BY: FOYSAL	SHEET NO: 09
DATE: NOV-2025	SCALE: 1:50	

EXECUTIVE AGENCY :	NAME OF WORK :				APPROVED BY	
			SUPERINTENDING ENGINEER EED	PROJECT DIRECTOR	CHIEF ENGINEER EED	VICE CHANCELLOR ISLAMIC ARABIC UNIVERSITY



EXECUTIVE AGENCY :	NAME OF WORK :				APPROVED BY		TEAM LEADER :				
							ELECTRICAL ENGINEER : ABDULLAH-AL-FOYSAL				
			SUPERINTENDING ENGINEER EED	PROJECT DIRECTOR OF ESTABLISHMENT OF ISLAMIC ARABIC UNIVERSITY	CHIEF ENGINEER EED	VICE CHANCELLOR ISLAMIC ARABIC UNIVERSITY			CHECKED BY:	CAD BY:	SHEET NO: 10
									DATE: NOV-2025	SCALE: 1:50	



SCALE: 1:50
AREA: 950 SQM

Rev. no.	Date:	Description
PROJECT: Mostofa Bhaban		
CLIENT: 		
CONSULTANT: 		
JOB TITLE : SINGLE LINE DIAGRAM OF 4TH FLOOR MDB-G TO DB 8 & 9		
DRAWING TITLE : Mostofa Bhaban, Electrical DRAWING		
OWNER'S SIGNATURE : 		
TEAM LEADER : 		
ELECTRICAL ENGINEER : ABDULLAH-AL-FOYSAL		
CHECKED BY:	CAD BY:	SHEET NO: 11
DATE: NOV-2025	SCALE: 1:50	

EXECUTIVE AGENCY :	NAME OF WORK :				APPROVED BY
			SUPERINTENDING ENGINEER EED	PROJECT DIRECTOR OF ESTABLISHMENT OF ISLAMIC ARABIC UNIVERSITY	CHIEF ENGINEER EED
					VICE CHANCELLOR ISLAMIC ARABIC UNIVERSITY



EXECUTIVE AGENCY :	NAME OF WORK :				APPROVED BY	
			SUPERINTENDING ENGINEER EED	PROJECT DIRECTOR OF ESTABLISHMENT OF ISLAMIC ARABIC UNIVERSITY	CHIEF ENGINEER EED	VICE CHANCELLOR ISLAMIC ARABIC UNIVERSITY



Rev. no.	Date:	Description
PROJECT: Mostofa Bhaban		
CLIENT:		
CONSULTANT:		
JOB TITLE :		
DRAWING TITLE : Mostofa Bhaban, Electrical DRAWING		
OWNER'S SIGNATURE :		
TEAM LEADER :		
ELECTRICAL ENGINEER : ABDULLAH-AL-FOYSAL		
CHECKED BY:	CAD BY:	SHEET NO: 13
DATE: NOV-2025	SCALE: 1:50	

EXECUTIVE AGENCY :	NAME OF WORK :				APPROVED BY	
				SUPERINTENDING ENGINEER EED	PROJECT DIRECTOR OF ESTABLISHMENT OF ISLAMIC ARABIC UNIVERSITY	CHIEF ENGINEER EED
						VICE CHANCELLOR ISLAMIC ARABIC UNIVERSITY



EXECUTIVE AGENCY :	NAME OF WORK :				APPROVED BY	
				SUPERINTENDING ENGINEER EED	PROJECT DIRECTOR OF ESTABLISHMENT OF ISLAMIC ARABIC UNIVERSITY	CHIEF ENGINEER EED
						VICE CHANCELLOR ISLAMIC ARABIC UNIVERSITY



EXECUTIVE AGENCY :	NAME OF WORK :				APPROVED BY
			SUPERINTENDING ENGINEER EED	PROJECT DIRECTOR OF ESTABLISHMENT OF ISLAMIC ARABIC UNIVERSITY	CHIEF ENGINEER EED
					VICE CHANCELLOR ISLAMIC ARABIC UNIVERSITY



ELECTRICAL LEGEND	
	DB DISTRIBUTION BOARD
	MDB MAIN DISTRIBUTION BOARD
	SB-2P SWITCH BOARD AT 1350 mm
	SB SWITCH BOARD AT 1350 mm
	P 05A, 250V, SWITCHED SOCKET (TYPE-P)
	P 13A, 250V, UNIVERSAL 3-PIN SWITCHED SOCKET
	T 15A, 250V, UNIVERSAL 3-PIN SWITCHED SOCKET
	BA BRACKET LIGHT FITTINGS WITH 1x12W LED LAMP
	BH BATHROOM MIRROR LED LIGHT FITTING
	SP SPOT LIGHT FITTING WITH 1x6W LED LAMP
	TA SURFACE TYPE LIGHT FITTING 1x18W LED T5 LAMP
	FH FAN HOOK
	EX.FAN AC CAPACITOR TYPE WALL MOUNTED EXHAUST FAN
	F 56 INCH SWEEP CEILING FAN
	CB CALLING BELL
	TDB TELEPHONE DISTRIBUTION BOARD
	TV TELEVISION OUTLET
	DM CCTV DOME TYPE CCTV CAMERA OUTLET
	B CCTV BULLET TYPE CCTV CAMERA OUTLET
	IN-R INTERNET ROUTER OUTLET
	JUNCTION BOX
	CONCEALED CABLE ROUTE
	CABLE ROUTE THROUGH FLOOR
NOTES:	
1. UNLESS OTHERWISE SPECIFIED, THE CONDUIT SIZE SHALL BE 3/4" INNER DIA.	

LIST OF FIXTURE	SYMBOL	HEIGHT FROM FFL
SWITCH, FAN REGULATOR	SB	1350mm
WALL BRACKET & TUBE LIGHT	BA, TA	2400mm
CEILING FAN	F	2600mm
05A SOCKET OUTLET	P	1350mm
13A SOCKET OUTLET	Q	250mm

Rev. no.	Date:	Description
PROJECT: Mostofa Bhaban		
CLIENT:		
CONSULTANT:		
JOB TITLE :		
DRAWING TITLE : Mostofa Bhaban, Electrical DRAWING		
OWNER'S SIGNATURE :		
TEAM LEADER :		
ELECTRICAL ENGINEER : ABDULLAH-AL-FOYSAL		
CHECKED BY:	CAD BY:	SHEET NO: 16
DATE: NOV-2025	SCALE: 1:50	

EXECUTIVE AGENCY :	NAME OF WORK :				APPROVED BY	
				SUPERINTENDING ENGINEER EED	PROJECT DIRECTOR OF ESTABLISHMENT OF ISLAMIC ARABIC UNIVERSITY	CHIEF ENGINEER EED
						VICE CHANCELLOR ISLAMIC ARABIC UNIVERSITY



Rev. no.	Date:	Description
PROJECT:		
Mostofa Bhaban		
CLIENT:		
CONSULTANT:		
JOB TITLE :		
DRAWING TITLE : Mostofa Bhaban, Electrical DRAWING		
OWNER'S SIGNATURE :		
TEAM LEADER :		
ELECTRICAL ENGINEER :		
ABDULLAH-AL-FOYSAL		
CHECKED BY:	CAD BY:	SHEET NO: 18
DATE: NOV-2025	SCALE: 1:100	

EXECUTIVE AGENCY :	NAME OF WORK :				APPROVED BY
			SUPERINTENDING ENGINEER EED	PROJECT DIRECTOR OF ESTABLISHMENT OF ISLAMIC ARABIC UNIVERSITY	CHIEF ENGINEER EED
					VICE CHANCELLOR ISLAMIC ARABIC UNIVERSITY



LIST OF FIXTURE	SYMBOL	HEIGHT FROM FFL
SWITCH, FAN REGULATOR	SB	1350mm
WALL BRACKET & TUBE LIGHT	BA, TA	2400mm
CEILING FAN	F	2600mm
05A SOCKET OUTLET	P	1350mm
13A SOCKET OUTLET	Q	250mm

Rev. no.	Date:	Description
PROJECT:		
Mostofa Bhaban		
CLIENT:		
CONSULTANT:		
JOB TITLE :		
DRAWING TITLE : Mostofa Bhaban, Electrical DRAWING		
OWNER'S SIGNATURE :		

EXECUTIVE AGENCY :	NAME OF WORK :				APPROVED BY		TEAM LEADER :		
							ELECTRICAL ENGINEER : ABDULLAH-AL-FOYSAL		
							CHECKED BY:	CAD BY:	SHEET NO: 19
							DATE: NOV-2025	SCALE: 1:50	
			SUPERINTENDING ENGINEER EED	PROJECT DIRECTOR OF ESTABLISHMENT OF ISLAMIC ARABIC UNIVERSITY	CHIEF ENGINEER EED	VICE CHANCELLOR ISLAMIC ARABIC UNIVERSITY			



AREA: 950 SQM

TEAM LEADER :		
ELECTRICAL ENGINEER : ABDULLAH-AL-FOYSAL		
CHECKED BY :	CAD BY :	SHEET NO: 21
DATE: NOV-2025	SCALE: 1:50	

EXECUTIVE AGENCY :	NAME OF WORK :				APPROVED BY
			SUPERINTENDING ENGINEER EED	PROJECT DIRECTOR OF ESTABLISHMENT OF ISLAMIC ARABIC UNIVERSITY	CHIEF ENGINEER EED
					VICE CHANCELLOR ISLAMIC ARABIC UNIVERSITY



AREA: 950 SQM

EXECUTIVE AGENCY :	NAME OF WORK :				APPROVED BY
			SUPERINTENDING ENGINEER EED	PROJECT DIRECTOR OF ESTABLISHMENT OF ISLAMIC ARABIC UNIVERSITY	CHIEF ENGINEER EED
					VICE CHANCELLOR ISLAMIC ARABIC UNIVERSITY



SCALE: 1:50
AREA: 950 SQM

EXECUTIVE AGENCY :	NAME OF WORK :				APPROVED BY		TEAM LEADER :
							ELECTRICAL ENGINEER : ABDULLAH-AL-FOYSAL
							CHECKED BY: CAD BY: SHEET NO: 23
							DATE: NOV-2025 SCALE: 1:50




SCALE: 1:100
AREA: 950 SQM

ELECTRICAL SYMBOLS	
	DB DISTRIBUTION BOARD
	MDB MAIN DISTRIBUTION BOARD
	SB-2P SWITCH BOARD AT 1350 mm
	SB SWITCH BOARD AT 1350 mm
	P 05A, 250V, SWITCHED SOCKET (TYPE-P)
	Q 13A, 250V, UNIVERSAL 3-PIN SWITCHED SOCKET
	T 15A, 250V, UNIVERSAL 3-PIN SWITCHED SOCKET
	BA BRACKET LIGHT FITTINGS WITH 1x12W LED LAMP
	BH BATHROOM MIRROR LED LIGHT FITTING
	SP SPOT LIGHT FITTING WITH 1x6W LED LAMP
	TA SURFACE TYPE LIGHT FITTING 1x18W LED T5 LAMP
	FH FAN HOOK
	EX.FAN AC CAPACITOR TYPE WALL MOUNTED EXHAUST FAN
	F 56 INCH SWEEP CEILING FAN
	CB CALLING BELL
	TDB TELEPHONE DISTRIBUTION BOARD
	TV TELEVISION OUTLET
	DM CCTV DOME TYPE CCTV CAMERA OUTLET
	B CCTV BULLET TYPE CCTV CAMERA OUTLET
	IN-R INTERNET ROUTER OUTLET
	JUNCTION BOX
	CONCEALED CABLE ROUTE
	CABLE ROUTE THROUGH FLOOR
NOTES:	
1. UNLESS OTHERWISE SPECIFIED, THE CONDUIT SIZE SHALL BE 3/4" INNER DIA.	

LIST OF FIXTURE	SYMBOL	HEIGHT FROM FFL
SWITCH, FAN REGULATOR	SB	1350mm
WALL BRACKET & TUBE LIGHT	BA, TA	2400mm
CEILING FAN	F	2600mm
05A SOCKET OUTLET	P	1350mm
13A SOCKET OUTLET	Q	250mm

Rev. no.	Date:	Description
PROJECT: Mostofa Bhaban		
CLIENT: 		
CONSULTANT: 		
JOB TITLE : POWER SOCKETS PLAN OF 4TH FLOOR		
DRAWING TITLE : Mostofa Bhaban, Electrical DRAWING		
OWNER'S SIGNATURE : 		
TEAM LEADER : 		
ELECTRICAL ENGINEER : ABDULLAH-AL-FOYSAL		
CHECKED BY:	CAD BY:	SHEET NO: 24
DATE: NOV-2025	SCALE: 1:50	

EXECUTIVE AGENCY :	NAME OF WORK :				APPROVED BY
			SUPERINTENDING ENGINEER EED	PROJECT DIRECTOR OF ESTABLISHMENT OF ISLAMIC ARABIC UNIVERSITY	CHIEF ENGINEER EED
					VICE CHANCELLOR ISLAMIC ARABIC UNIVERSITY

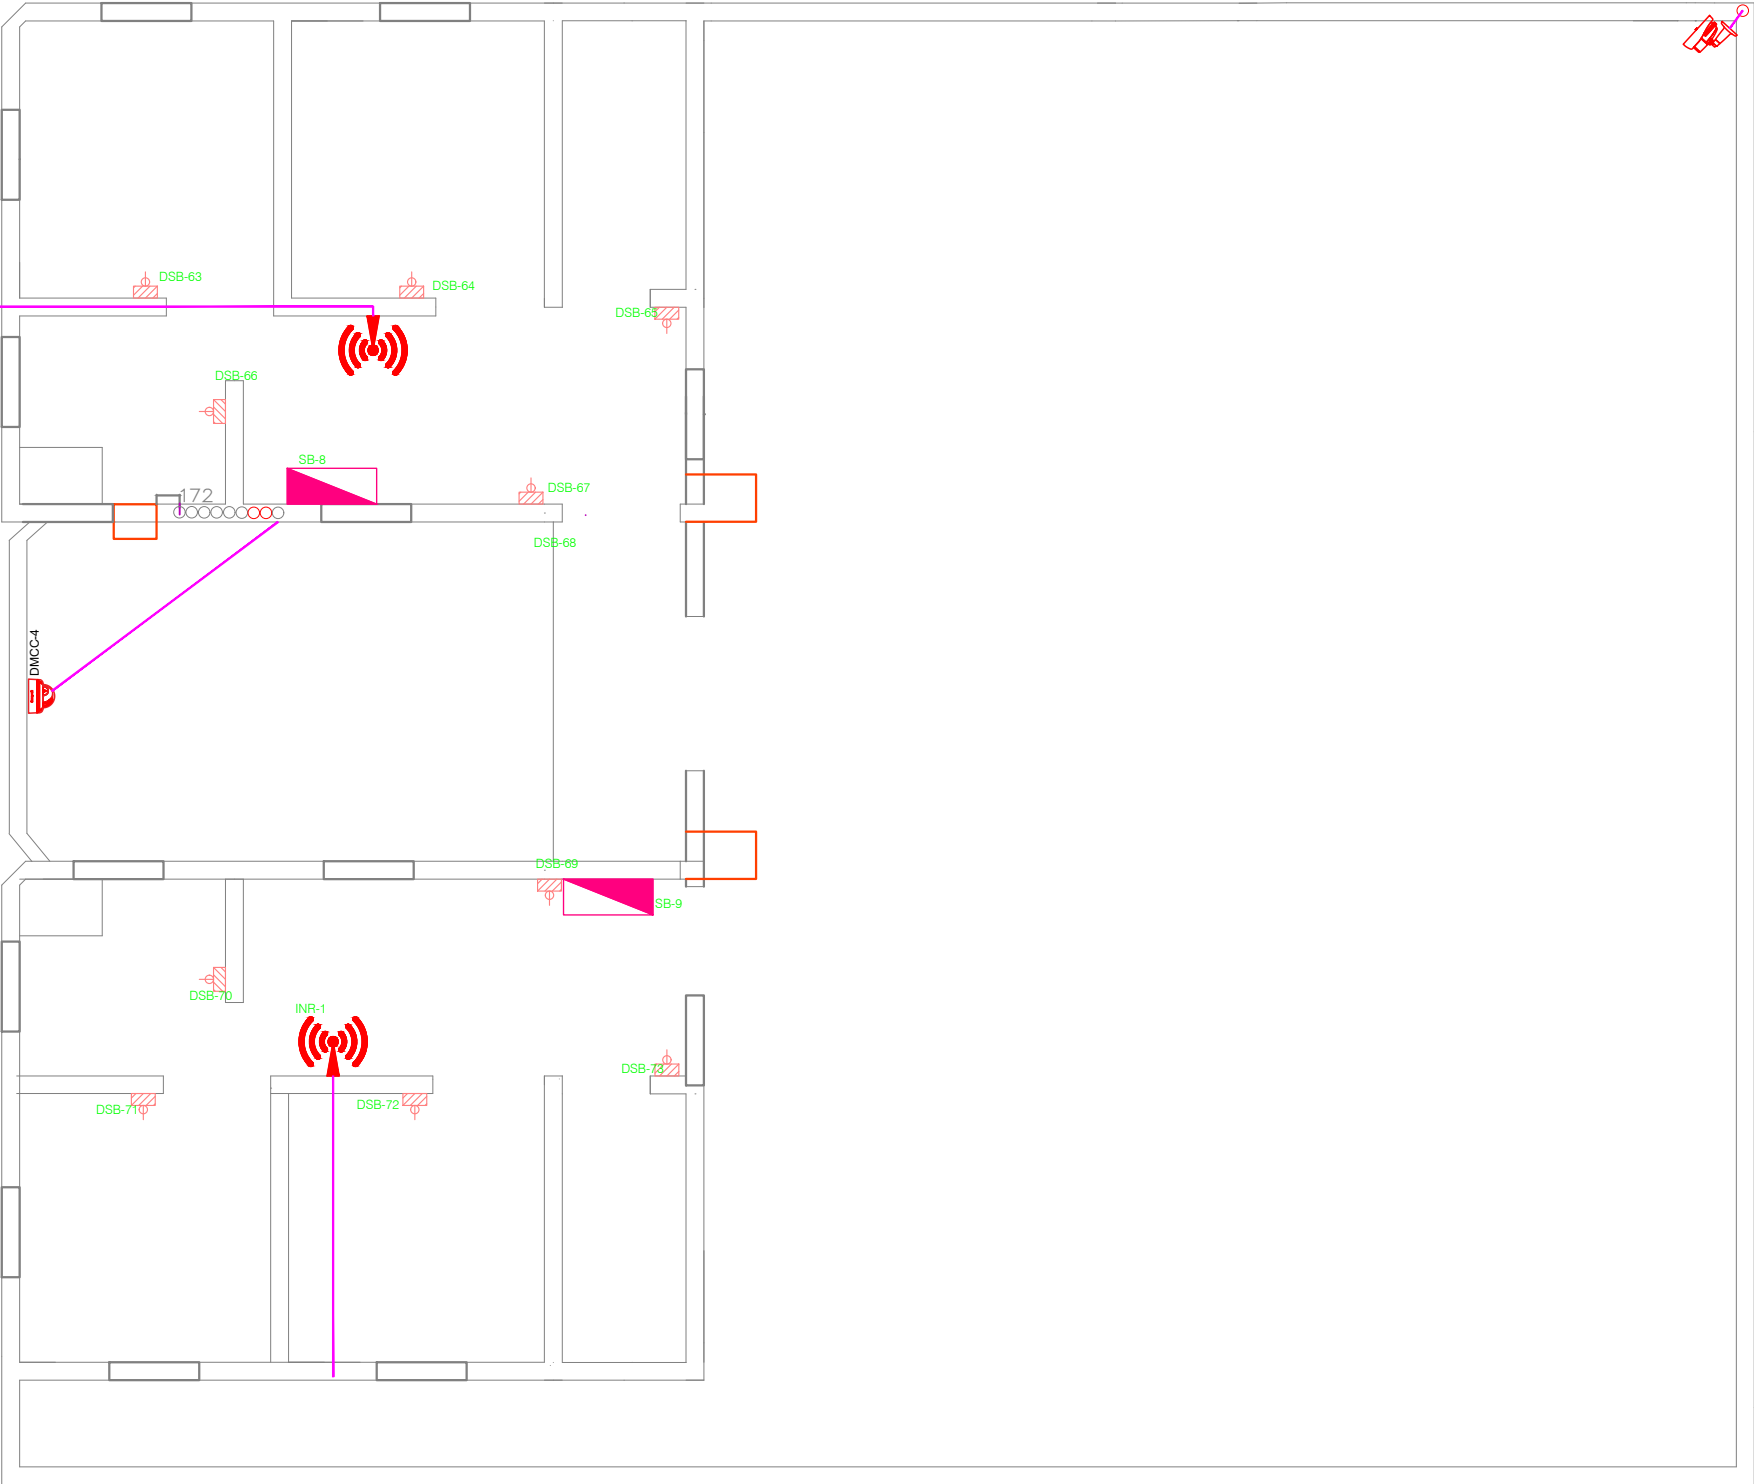

INTERNET & CCTV OUTLET AND CONDUIT LAYOUT OF ROOF FLOOR

SCALE: 1:50
AREA: 950 SQM

ELECTRICAL LEGEND

- | | | |
|--|--------------|--|
| | DB | DISTRIBUTION BOARD |
| | MDB | MAIN DISTRIBUTION BOARD |
| | SB-2P | SWITCH BOARD AT 1350 mm |
| | SB | SWITCH BOARD AT 1350 mm |
| | P | 05A, 250V, SWITCHED SOCKET (TYPE-P) |
| | Q | 13A, 250V, UNIVERSAL 3-PIN SWITCHED SOCKET |
| | T | 15A, 250V, UNIVERSAL 3-PIN SWITCHED SOCKET |
| | BA | BRACKET LIGHT FITTINGS WITH 1x12W LED LAMP |
| | BH | BATHROOM MIRROR LED LIGHT FITTING |
| | SP | SPOT LIGHT FITTING WITH 1x6W LED LAMP |
| | TA | SURFACE TYPE LIGHT FITTING 1x18W LED T5 LAMP |
| | FH | FAN HOOK |
| | EX.FAN | AC CAPACITOR TYPE WALL MOUNTED EXHAUST FAN |
| | F | 56 INCH SWEEP CEILING FAN |
| | CB | CALLING BELL |
| | TDB | TELEPHONE DISTRIBUTION BOARD |
| | TV | TELEVISION OUTLET |
| | DM CCTV | DOME TYPE CCTV CAMERA OUTLET |
| | B CCTV | BULLET TYPE CCTV CAMERA OUTLET |
| | IN-R | INTERNET ROUTER OUTLET |
| | JUNCTION BOX | JUNCTION BOX |

- CONCEALED CABLE ROUTE
— CABLE ROUTE THROUGH FLOOR


NOTES:

1. UNLESS OTHERWISE SPECIFIED, THE CONDUIT SIZE SHALL BE 3/4" INNER DIA.

LIST OF FIXTURE	SYMBOL	HEIGHT FROM FFL
SWITCH, FAN REGULATOR	SB	1350mm
WALL BRACKET & TUBE LIGHT	BA, TA	2400mm
CEILING FAN	F	2600mm
05A SOCKET OUTLET	P	1350mm
13A SOCKET OUTLET	Q	250mm

Rev. no.	Date:	Description
PROJECT:		
Mostofa Bhakan		
CLIENT:		
CONSULTANT:		
JOB TITLE :CCTV (ELV) PLAN OF 4TH FLOOR		
DRAWING TITLE : Mostofa Bhakan, Electrical DRAWING		
OWNER'S SIGNATURE :		
TEAM LEADER :		
ELECTRICAL ENGINEER : ABDULLAH-AL-FOYSAL		
CHECKED BY:	CAD BY:	SHEET NO: 25
DATE: NOV-2025	SCALE: 1:100	

EXECUTIVE AGENCY :	NAME OF WORK :				APPROVED BY	
			SUPERINTENDING ENGINEER EED	PROJECT DIRECTOR OF ESTABLISHMENT OF ISLAMIC ARABIC UNIVERSITY	CHIEF ENGINEER EED	VICE CHANCELLOR ISLAMIC ARABIC UNIVERSITY

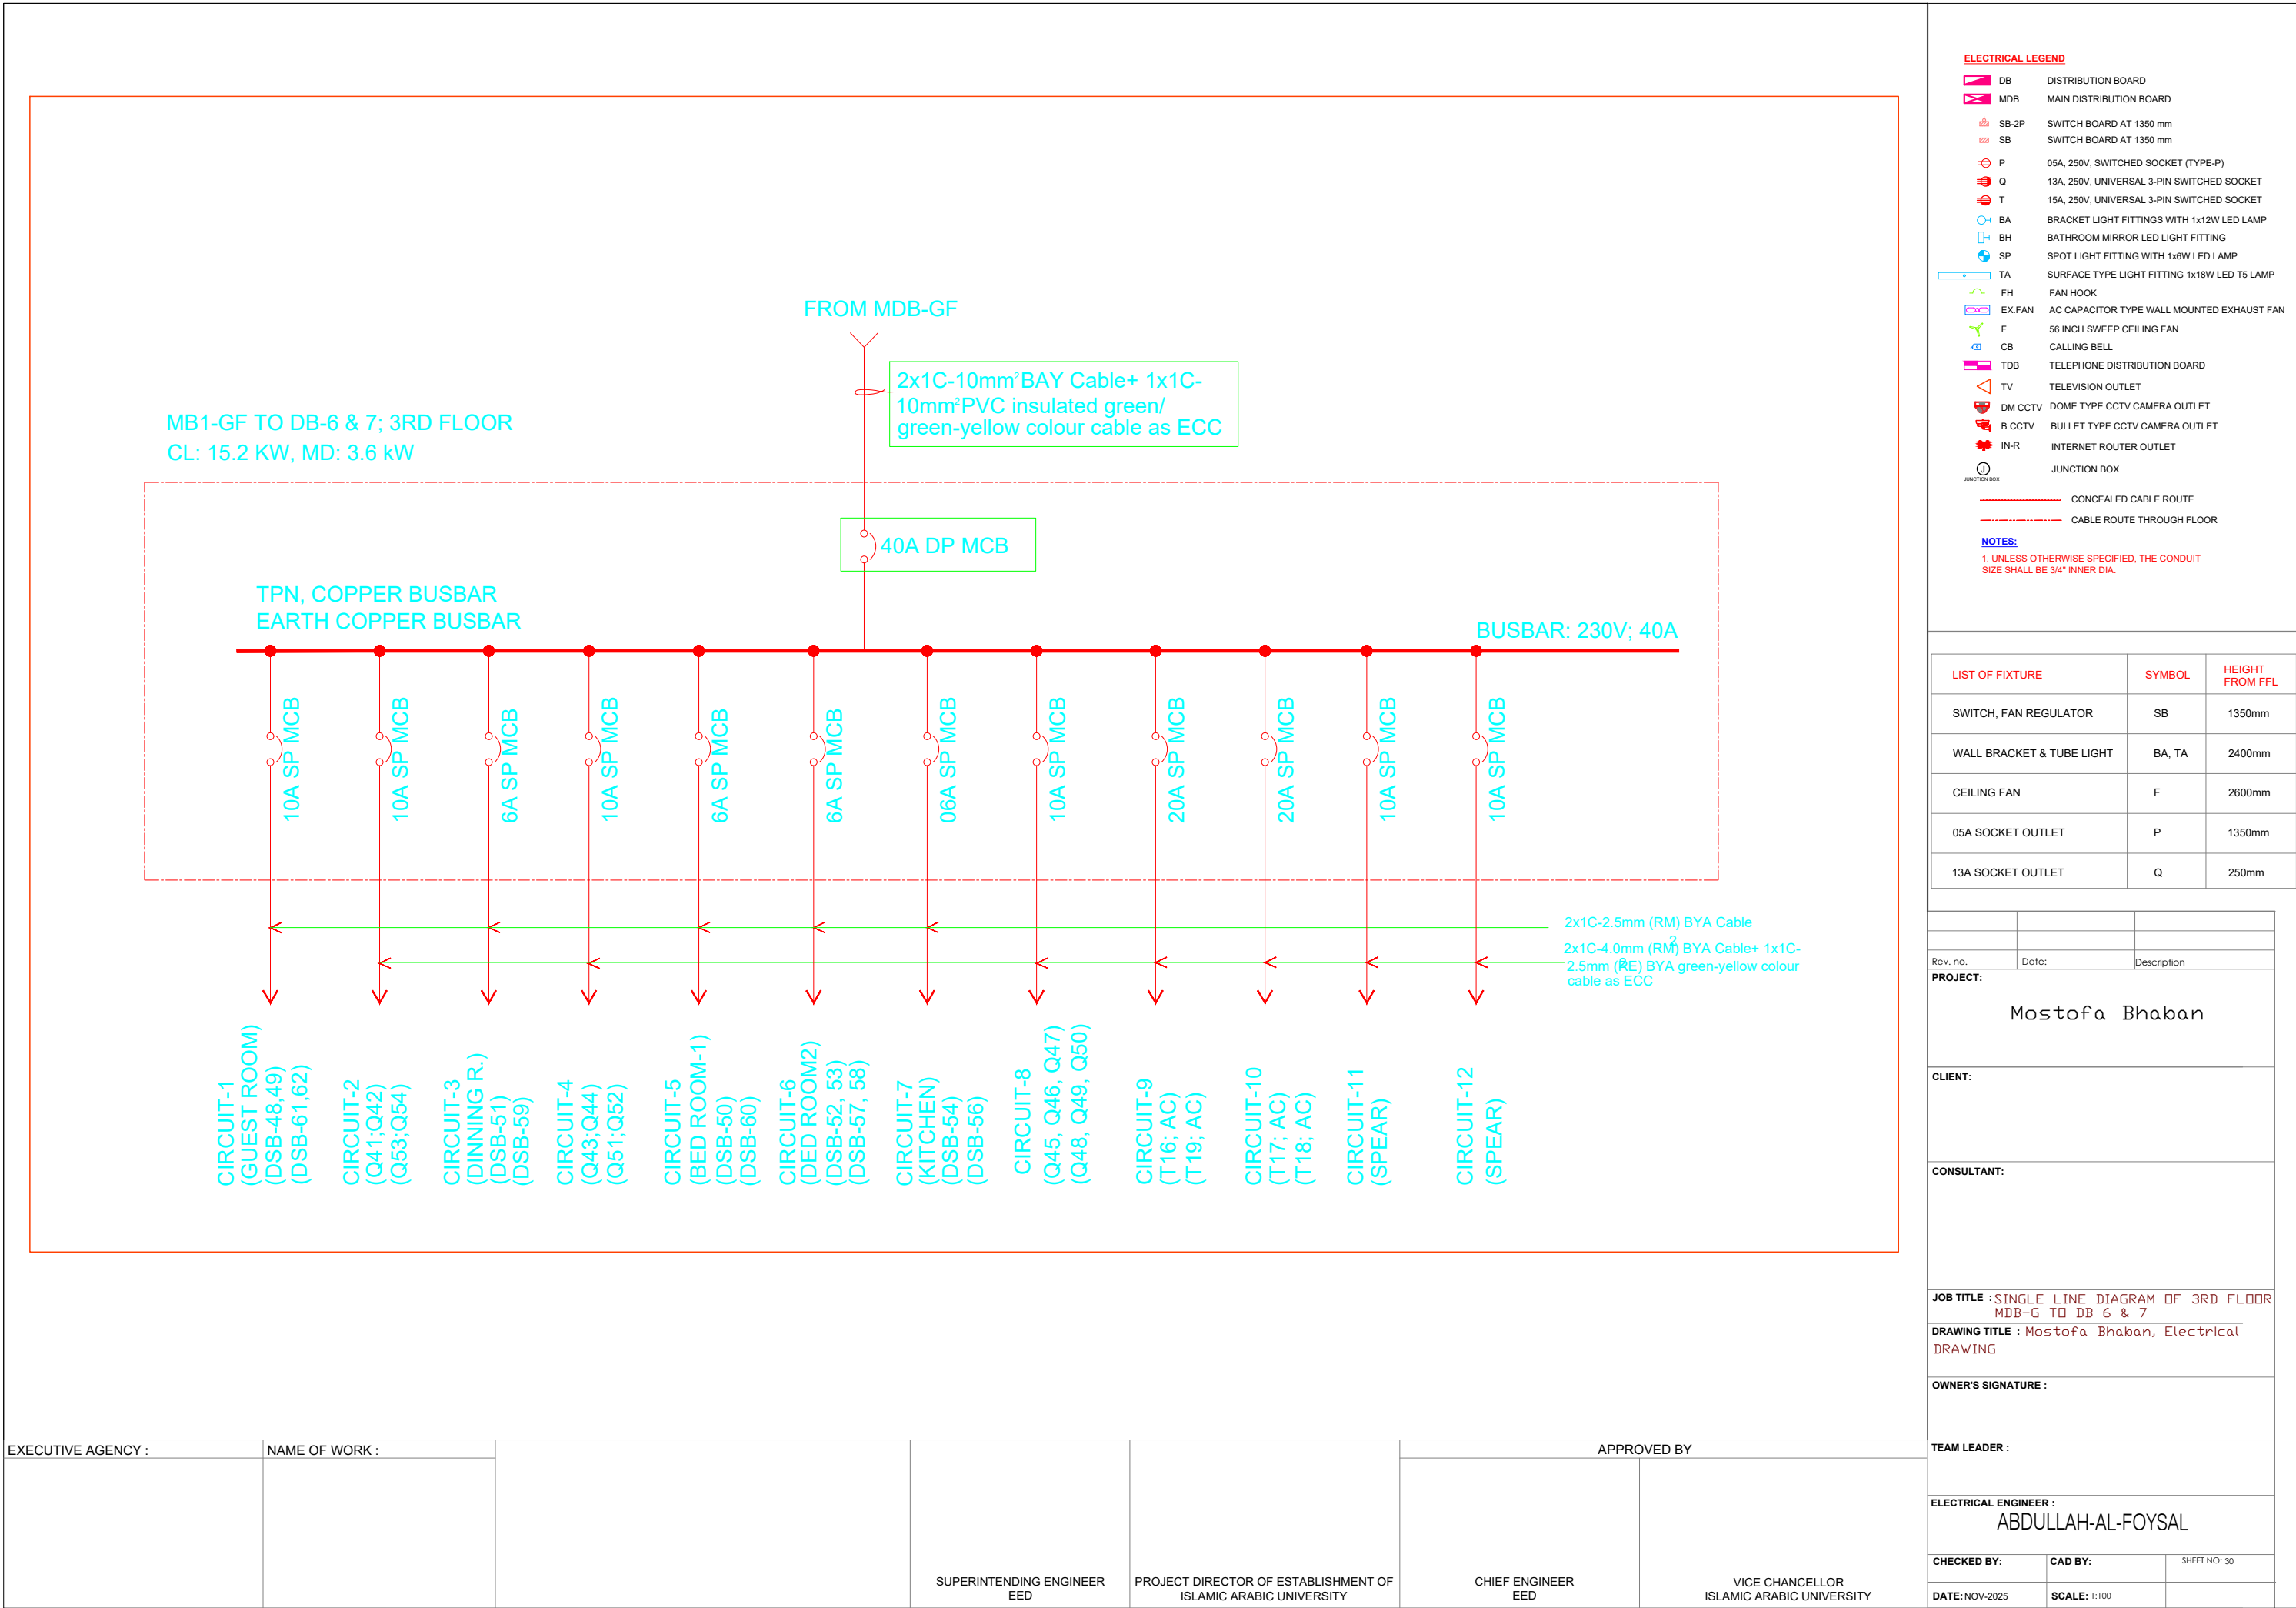



SCALE: 1:100
AREA: 950 SQM

LIST OF FIXTURE	SYMBOL	HEIGHT FROM FFL
SWITCH, FAN REGULATOR	SB	1350mm
WALL BRACKET & TUBE LIGHT	BA, TA	2400mm
CEILING FAN	F	2600mm
05A SOCKET OUTLET	P	1350mm
13A SOCKET OUTLET	Q	250mm

JOB TITLE : SINGLE LINE DIAGRAM OF 4TH FLOOR MDB-G TO DB 8 & 9
DRAWING TITLE : Mostofa Bhaban, Electrical DRAWING

OWNER'S SIGNATURE :		
TEAM LEADER :		
ELECTRICAL ENGINEER : ABDULLAH-AL-FOYSAL		
CHECKED BY:	CAD BY:	SHEET NO: 32
DATE: NOV-2025	SCALE: 1:50	

EXECUTIVE AGENCY :	NAME OF WORK :				APPROVED BY	
			SUPERINTENDING ENGINEER EED	PROJECT DIRECTOR OF ESTABLISHMENT OF ISLAMIC ARABIC UNIVERSITY	CHIEF ENGINEER EED	VICE CHANCELLOR ISLAMIC ARABIC UNIVERSITY